

Дом · единая книга проекта P82

Размеры новой геометрии. Номинальные контрольные грани; не монтажный чертёж.

Состав и порядок

Сначала размерные планы, мебель и отделка; затем 25 видов 3D, включая дополнительные ракурсы гостиной и обеих спален; далее инженерные схемы, задания по фундаменту, каркасу, кровле, фасадам и обмеры для предварительной оценки.

Включены последние изменения

Дом 11560 × 8160 мм с расширением на запад и восток. Светлая широкая обшивка с читаемой фактурой; оливковые акценты. В лаундже длинный диван F61 у северного стекла вместо четырёх стульев. Четыре южных стула, стол, печь, ниши и кухня сохранены.

Где смотреть новые решения

A207 — лаундж с диваном и нишей для инструмента; A412 — высоты дивана и отделка; A302–A304 — текущие 57 позиций мебели. M106 — свет над той же расстановкой. Все старые северные стулья исключены из текущих планов и визуалов.

Файлы для пересылки

Полная книга PDF; отдельный PDF с планами и данными строителям; HTML с встроенными рисунками; ZIP с этими файлами, SVG, CSV, данными модели и редактируемой 3D-сценой. Код и прежние выпуски в пересылаемый архив не включены.

Граница готовности

Для согласования и предварительной оценки, не для стройки или заказа. Изделия, рабочие КР/КД, расчёты, составы стен и кровли, электрика, отопление, дымоход и пожарные узлы не утверждены. Технические указатели P02/P45 сохранены; P82 не подменяет профессиональную проверку.

Площади после расширения и область перерасчёта

Размеры новой геометрии. Номинальные контрольные грани; не монтажный чертёж.


Зона	До, м²	Теперь, м²	Прирост, м²
Внешний контур	89.43	94.33	4.9
Кухня, столовая и гостиная	30.1	32.31	2.21
Прихожая и хозяйственный шкаф	6.1	6.1	0
Гостевой санузел и постирочная	5.34	5.89	0.55
Основной санузел	3.65	4.1	0.46
Основная спальня	13.54	14.62	1.08
Вторая спальня	11.16	11.16	0
Лаундж	41.16	41.16	0
Контуров всех террас	97.69	100.93	3.24

Пересобраны все текущие планы, фасады, оболочка, координатные ведомости, инженерные схемы и визуалы. Разница площадей вычислена по полигонам; внутренние зоны не включают полосы перегородок и все пороги.

Не выполнены и не имитируются: расчёты прочности/осадок/устойчивости, подбор арматуры и сечений, теплопотери, гидравлика, освещённость и селективность защит. Листы В101–В108 и В201–В204 передают исходные данные и требования к этим работам.

Стены и проёмы: все наружные простенки

Размеры новой геометрии. Номинальные контрольные грани; не монтажный чертёж.

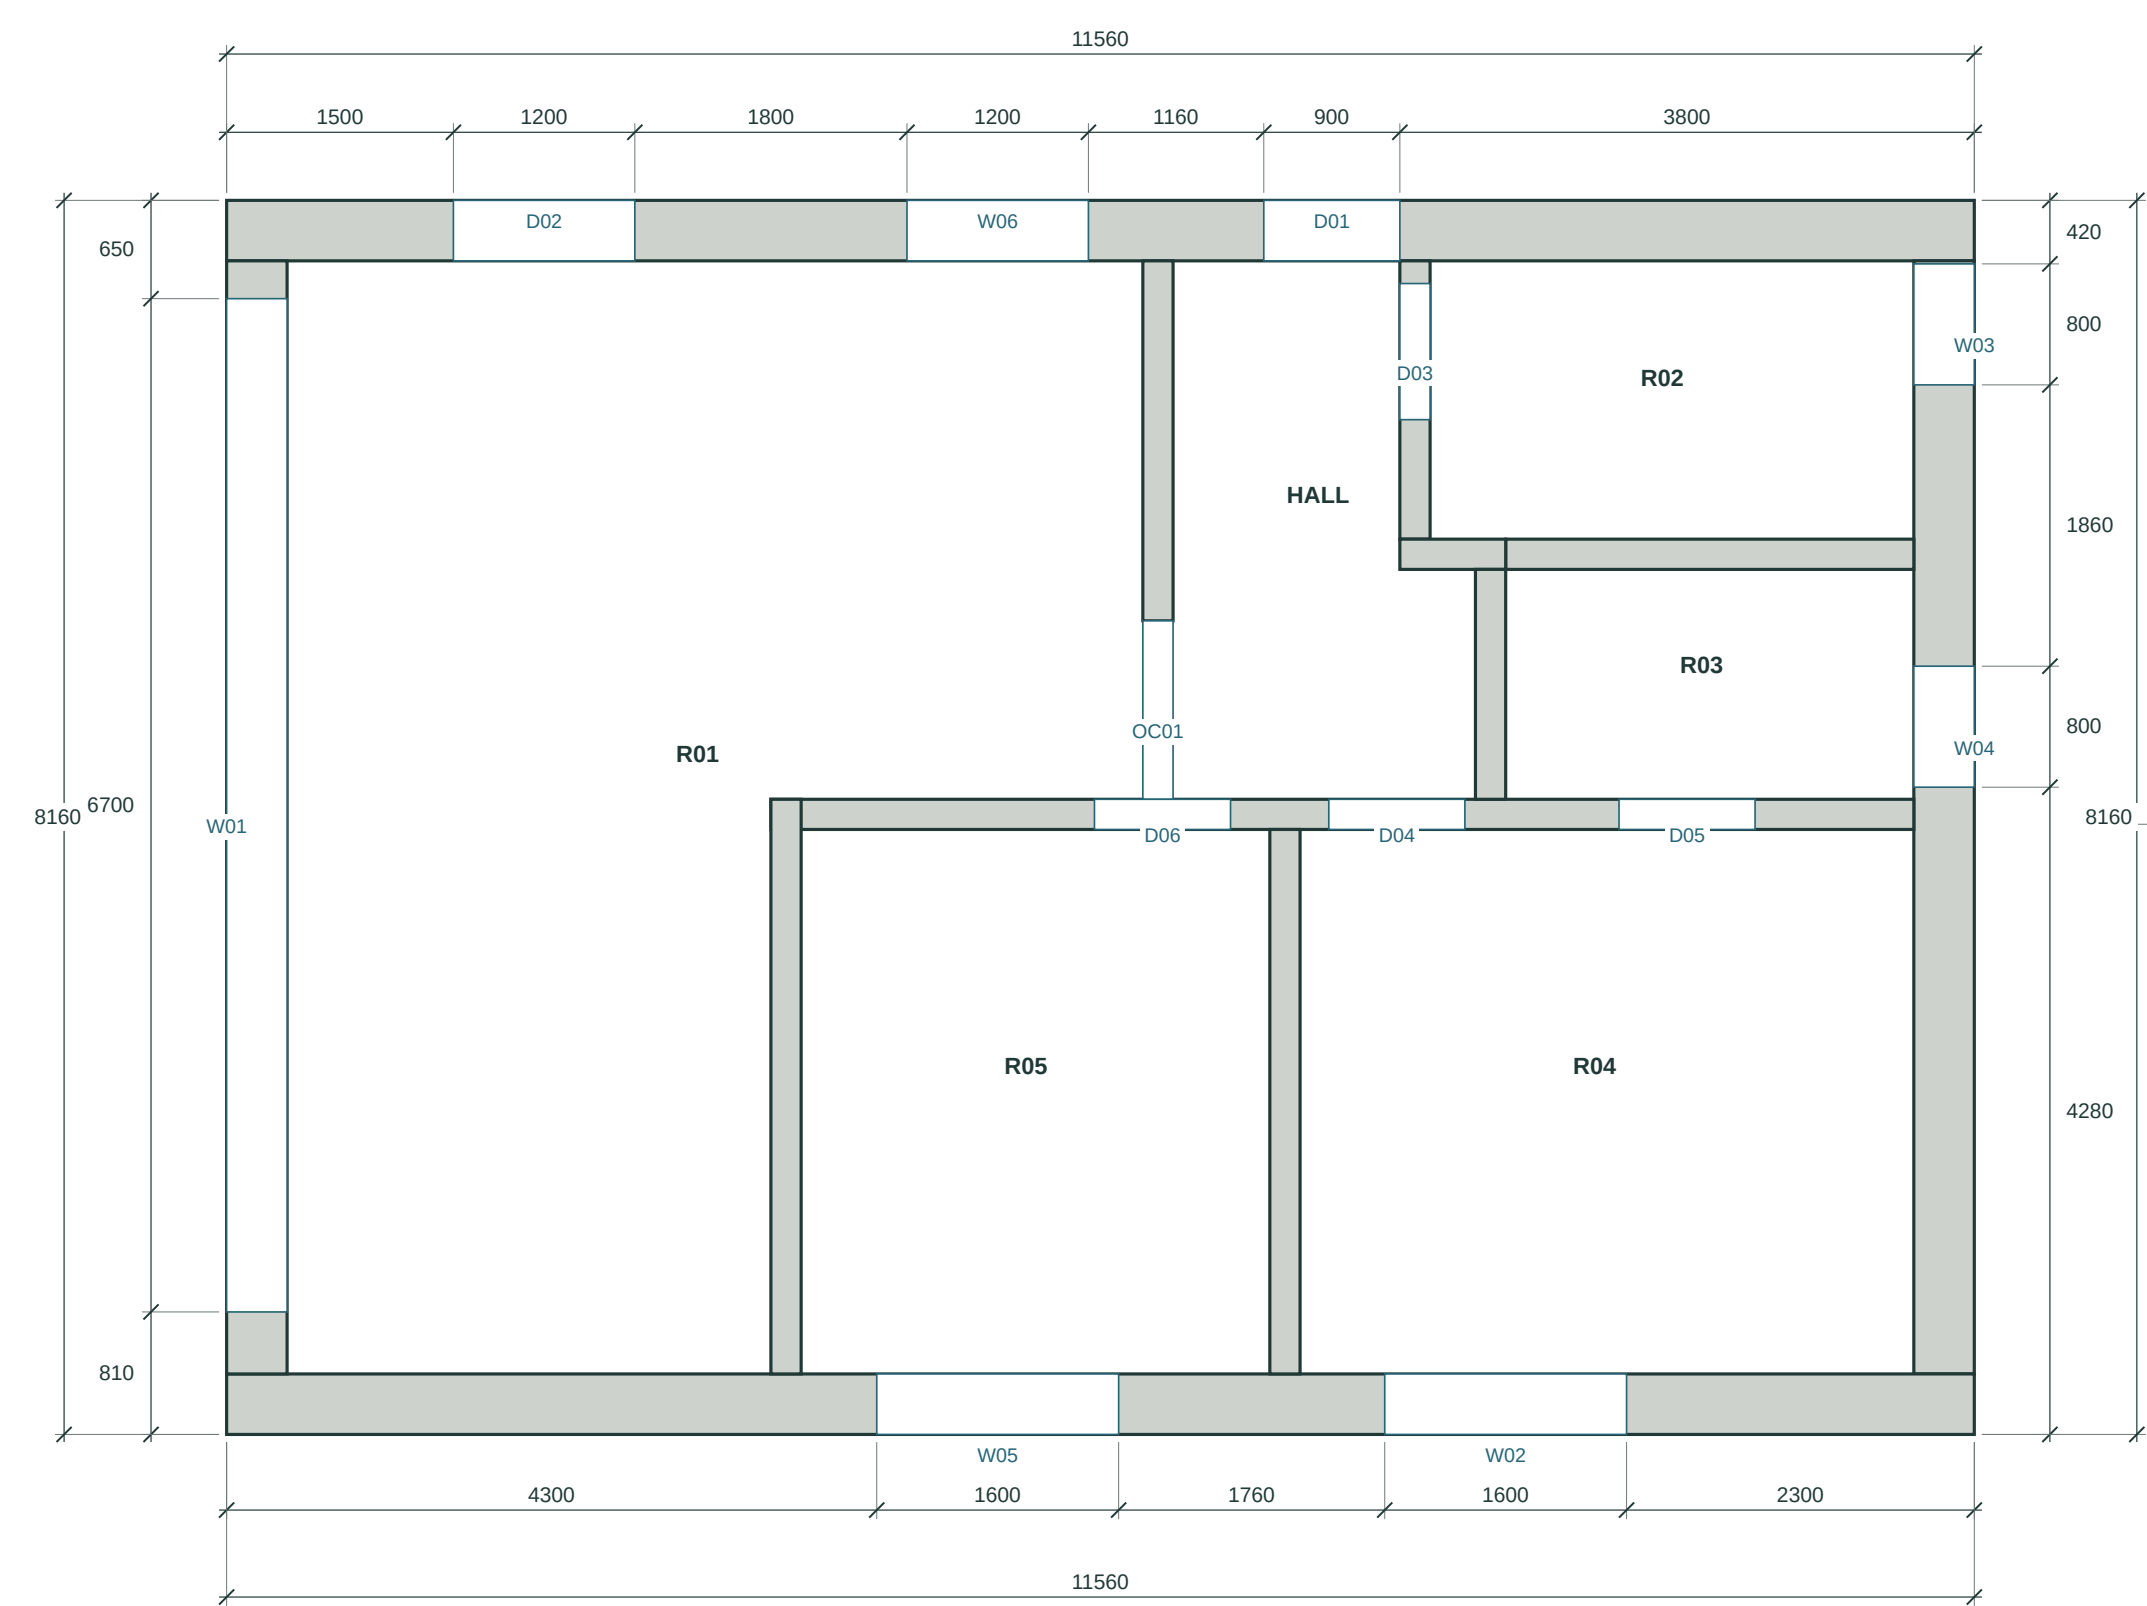

Новое расширение

Запад: −300 мм. Восток: +300 мм. Внешний габарит 11560 × 8160. Внутренние перегородки закреплены в прежней системе.

Начало координат

X=0/Y=0 — прежний северо-западный угол. Новый западный край X=−300; восточный X=11260. Север сверху; озеро слева.

Что размерено


Каждый участок наружной стены и номинальный проём. Внутренние простенки отдельно на A201–A207. Размеры — миллиметры.

Стены / проёмы

400 и 200 — контрольные толщины модели, не сечения дерева. D — дверь; W — окно; OC — открытая связь. Коробки, монтажные проёмы и чистый проход не определены.

Перегородки: привязки, толщины и длины

Размеры новой геометрии. Номинальные контрольные грани; не монтажный чертёж.

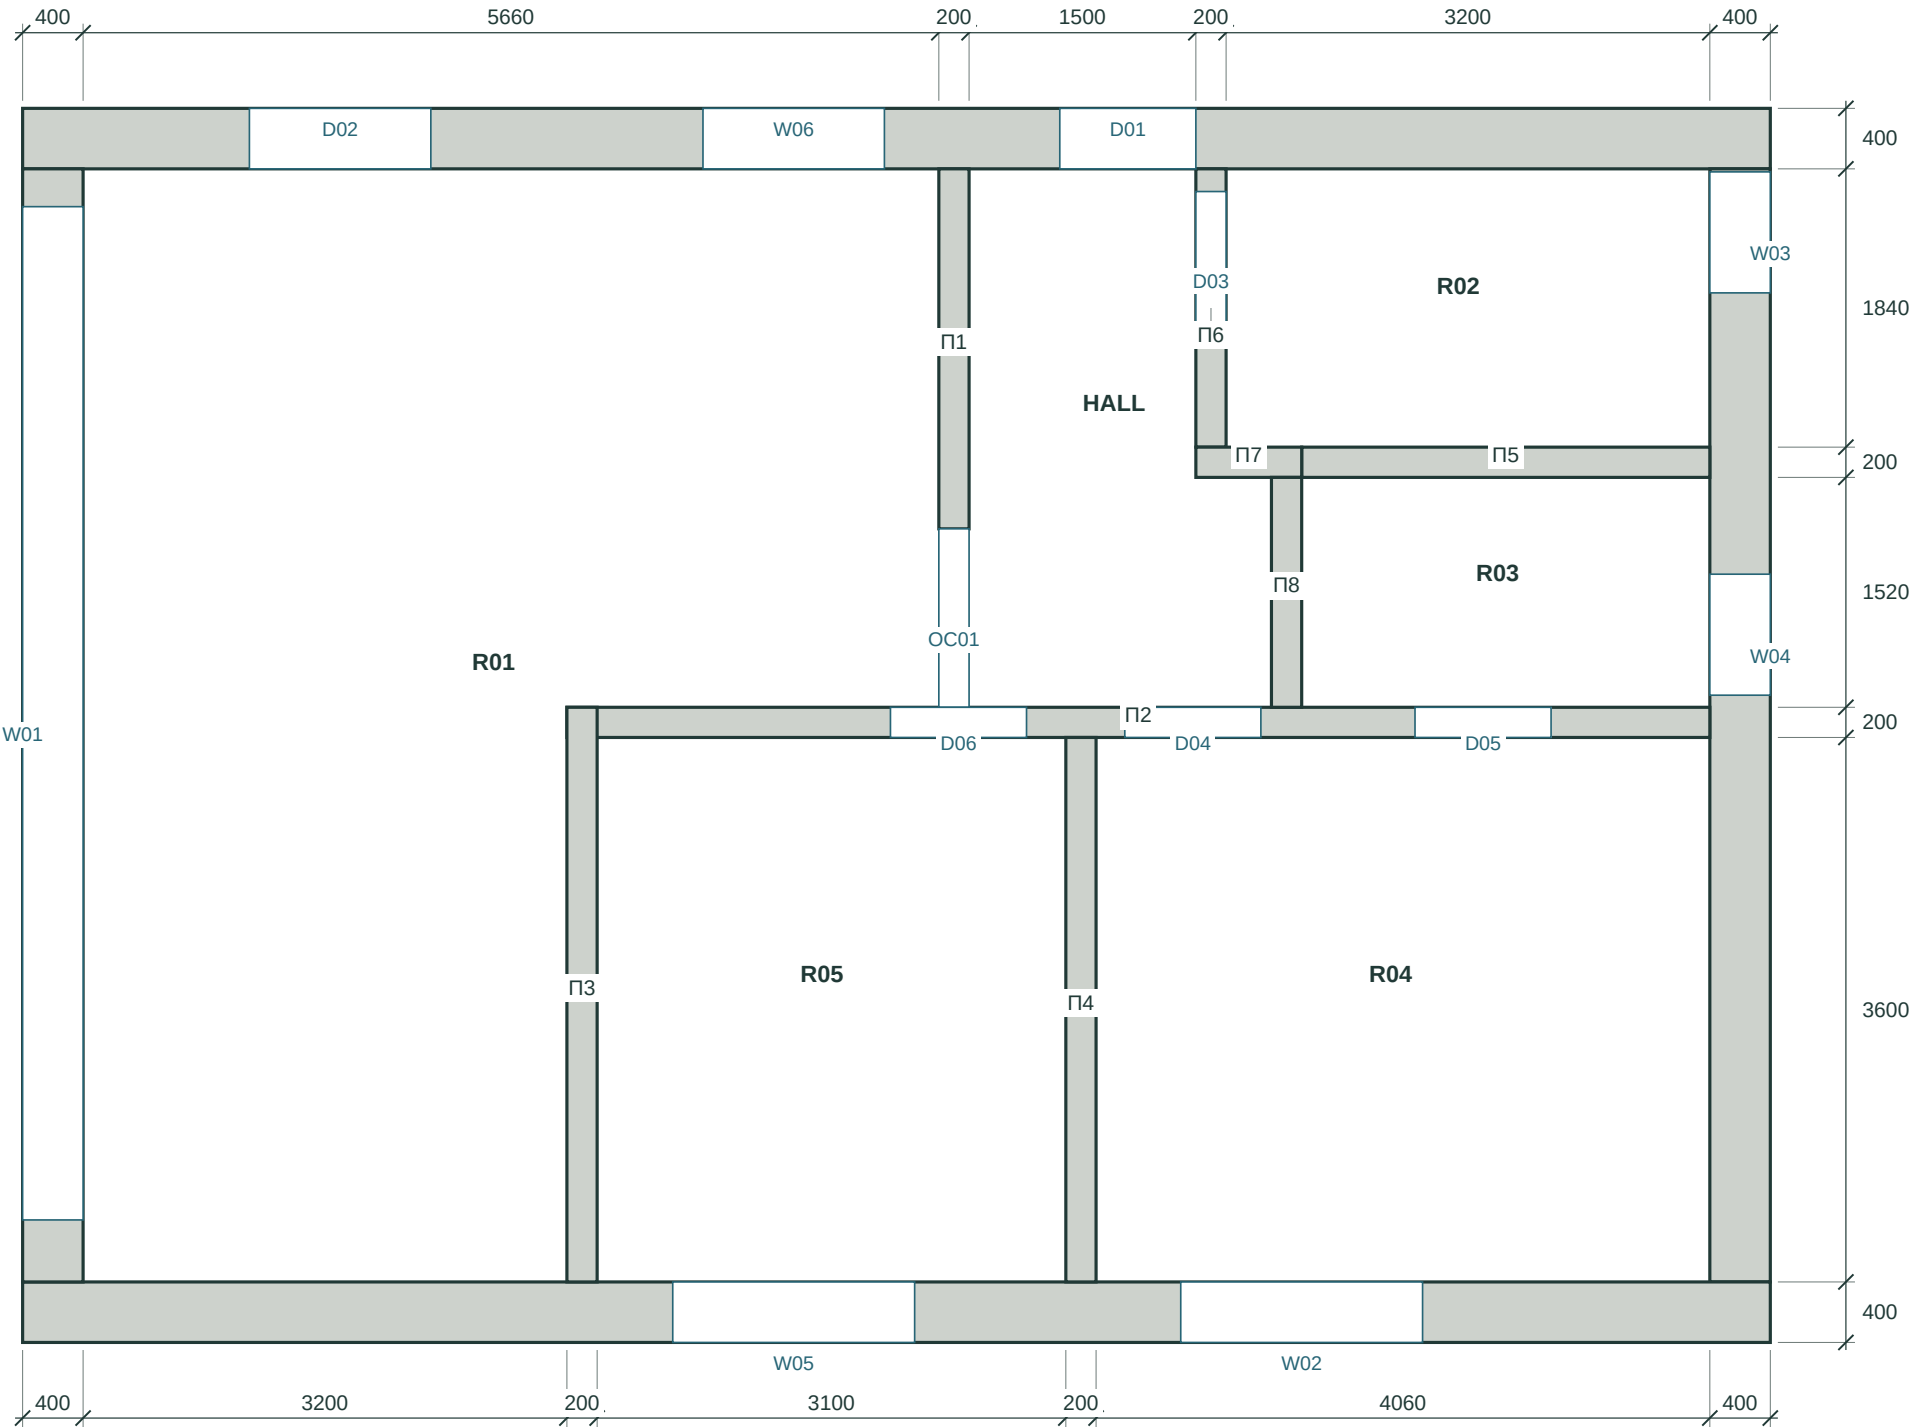

Контрольные полосы П1–П8

П1: X=5760; Y=400
Габарит X / Y: 200 / 2380

П2: X=3300; Y=3960
Габарит X / Y: 7560 / 200

П3: X=3300; Y=3960
Габарит X / Y: 200 / 3800

П4: X=6600; Y=4160
Габарит X / Y: 200 / 3600

П5: X=8160; Y=2240
Габарит X / Y: 2700 / 200

П6: X=7460; Y=400
Габарит X / Y: 200 / 1840

П7: X=7460; Y=2240
Габарит X / Y: 700 / 200


П8: X=7960; Y=2440
Габарит X / Y: 200 / 1520

X/Y — от прежнего начала координат. Длины полос включают пересечения: объёмы и площади считать по объединению, не суммой прямоугольников.

До новой восточной стены продлены WB02 и P04. Все остальные внутренние контрольные грани сохранены.

Общая планировка с мебелью после расширения

Размеры новой геометрии. Номинальные контрольные грани; не монтажный чертёж.

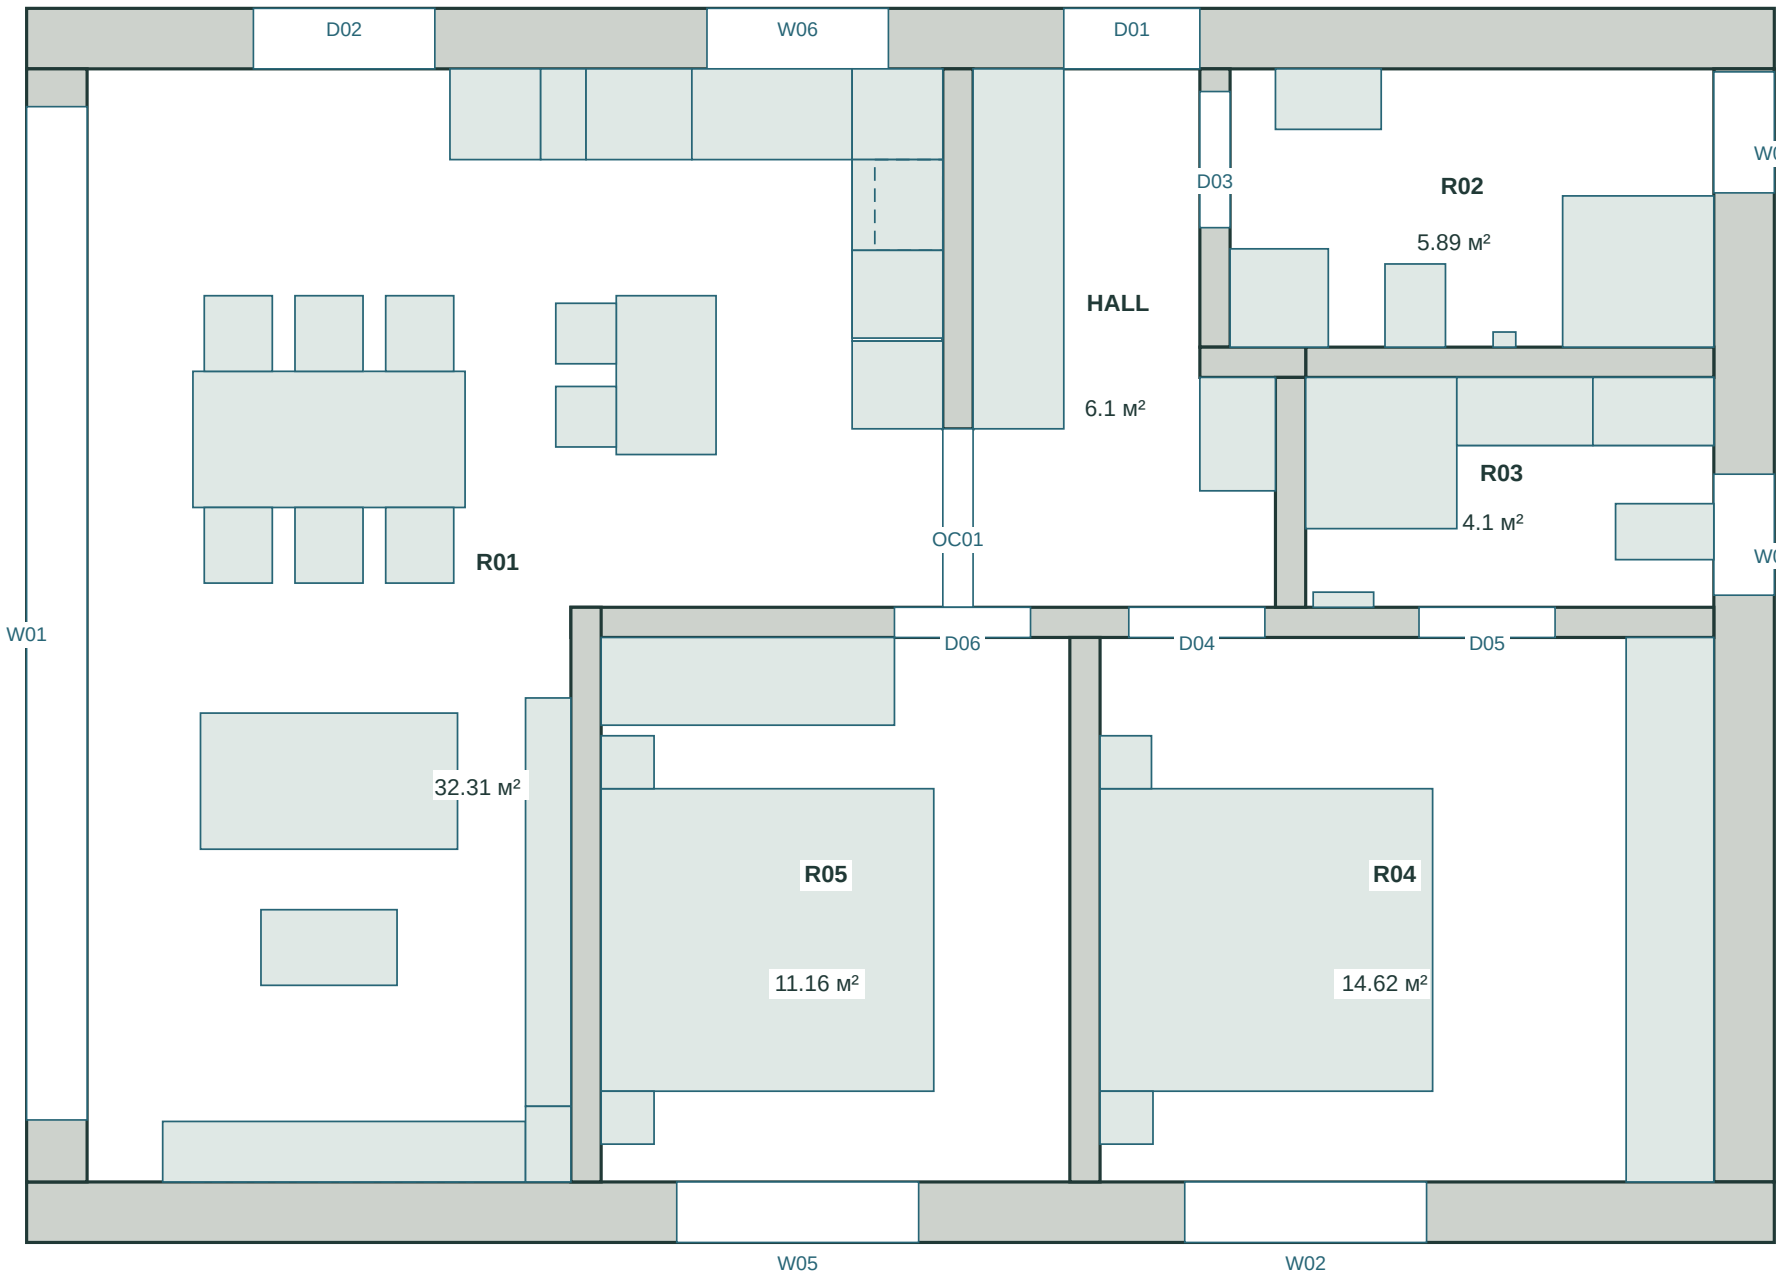

Дополнительное пространство

Прибавка между контрольными гранями: гостиная +2,208 м²; гостевой с/у +0,552; основной с/у +0,456; мастер-спальня +1,080.

Что осталось на месте

Прихожая, спальня 2, кухня, основные внутренние перегородки и обе двери из дома в лаундж. Свободную мебель не растягивали.

Привязано к новой стене


Душ гостевого с/у, унитаз основного с/у и гардероб мастер-спальни сдвинуты на восток на 300. Тумба и столешница основного с/у продлены на 300.

Где подробные размеры

A201–A207 — увеличенные виды комнат. A302–A304 — ведомость всех предметов: размеры, положение и высотная информация. CSV/JSON приложены отдельно.

Оболочка: контуры дома, крыши и террасы

Размеры новой геометрии. Номинальные контрольные грани; не монтажный чертёж.

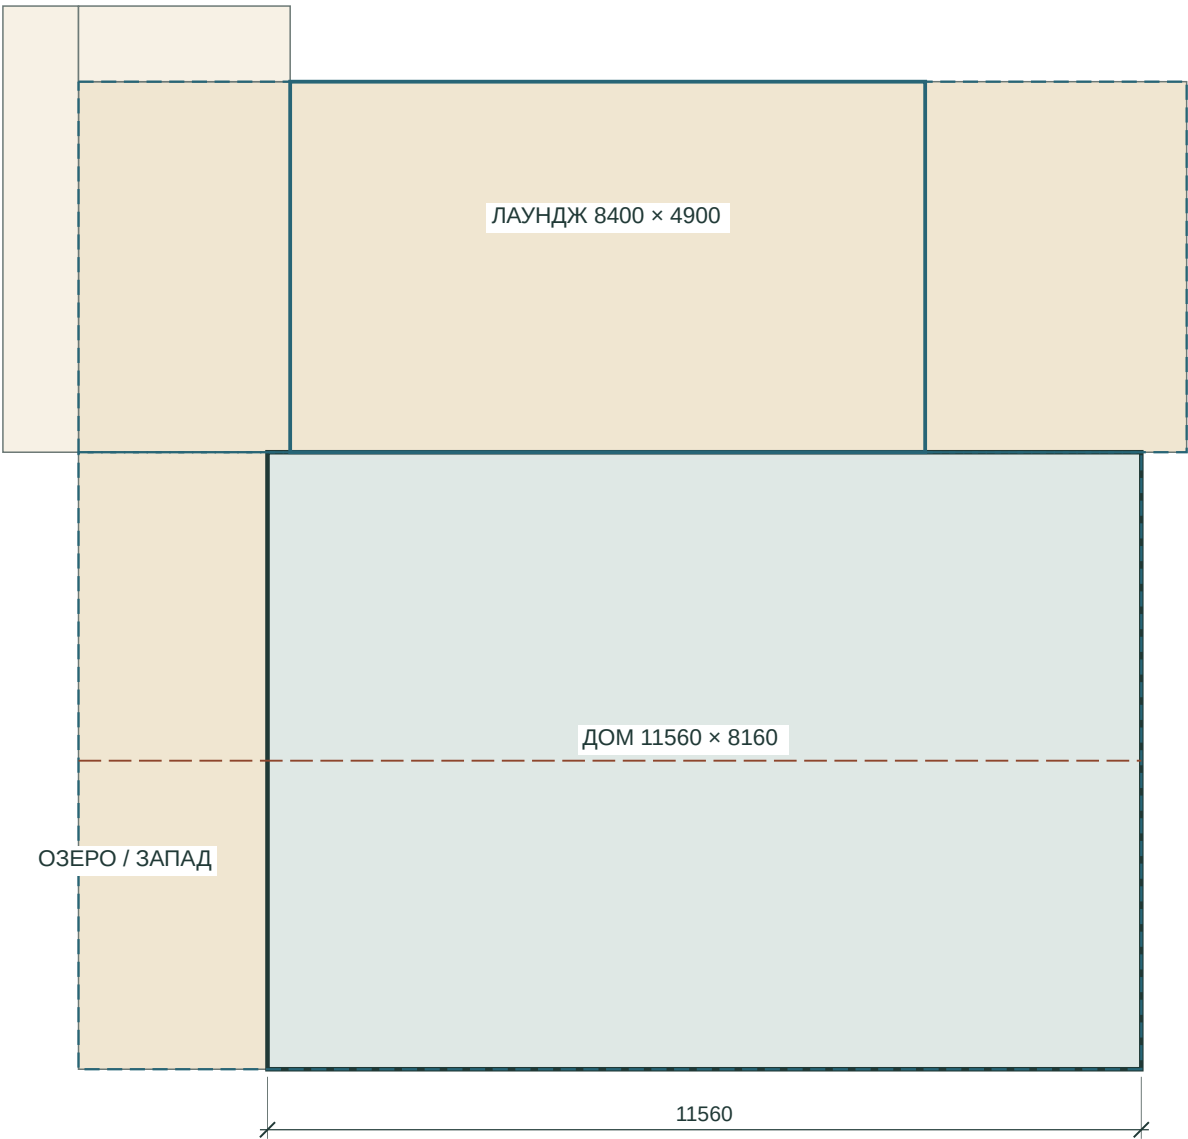

Вылеты — предложение

Сохранены относительно новых наружных стен: запад 2500, восток навеса 600. Это геометрия Р76, не расчёт несущих элементов.

Основная крыша

Проекция 14060 × 8160. Конёк Y=4080. Графические уровни 3300/5000 сохранены. Площадь покрытия не равна проекции.

Фундамент и каркас


Передан новый внешний контур. Опоры, пролёты, нагрузки, сечения, армирование и деформации требуют расчёта конструктора.

Лаундж и дымоход

Лаундж и печь не сдвинуты. Ось дымохода — конёк: 4480 по плану. Высота трубы и проходка не утверждены.

Кухня, столовая и гостиная: стены и мебель

Размеры новой геометрии. Номинальные контрольные грани; не монтажный чертёж.

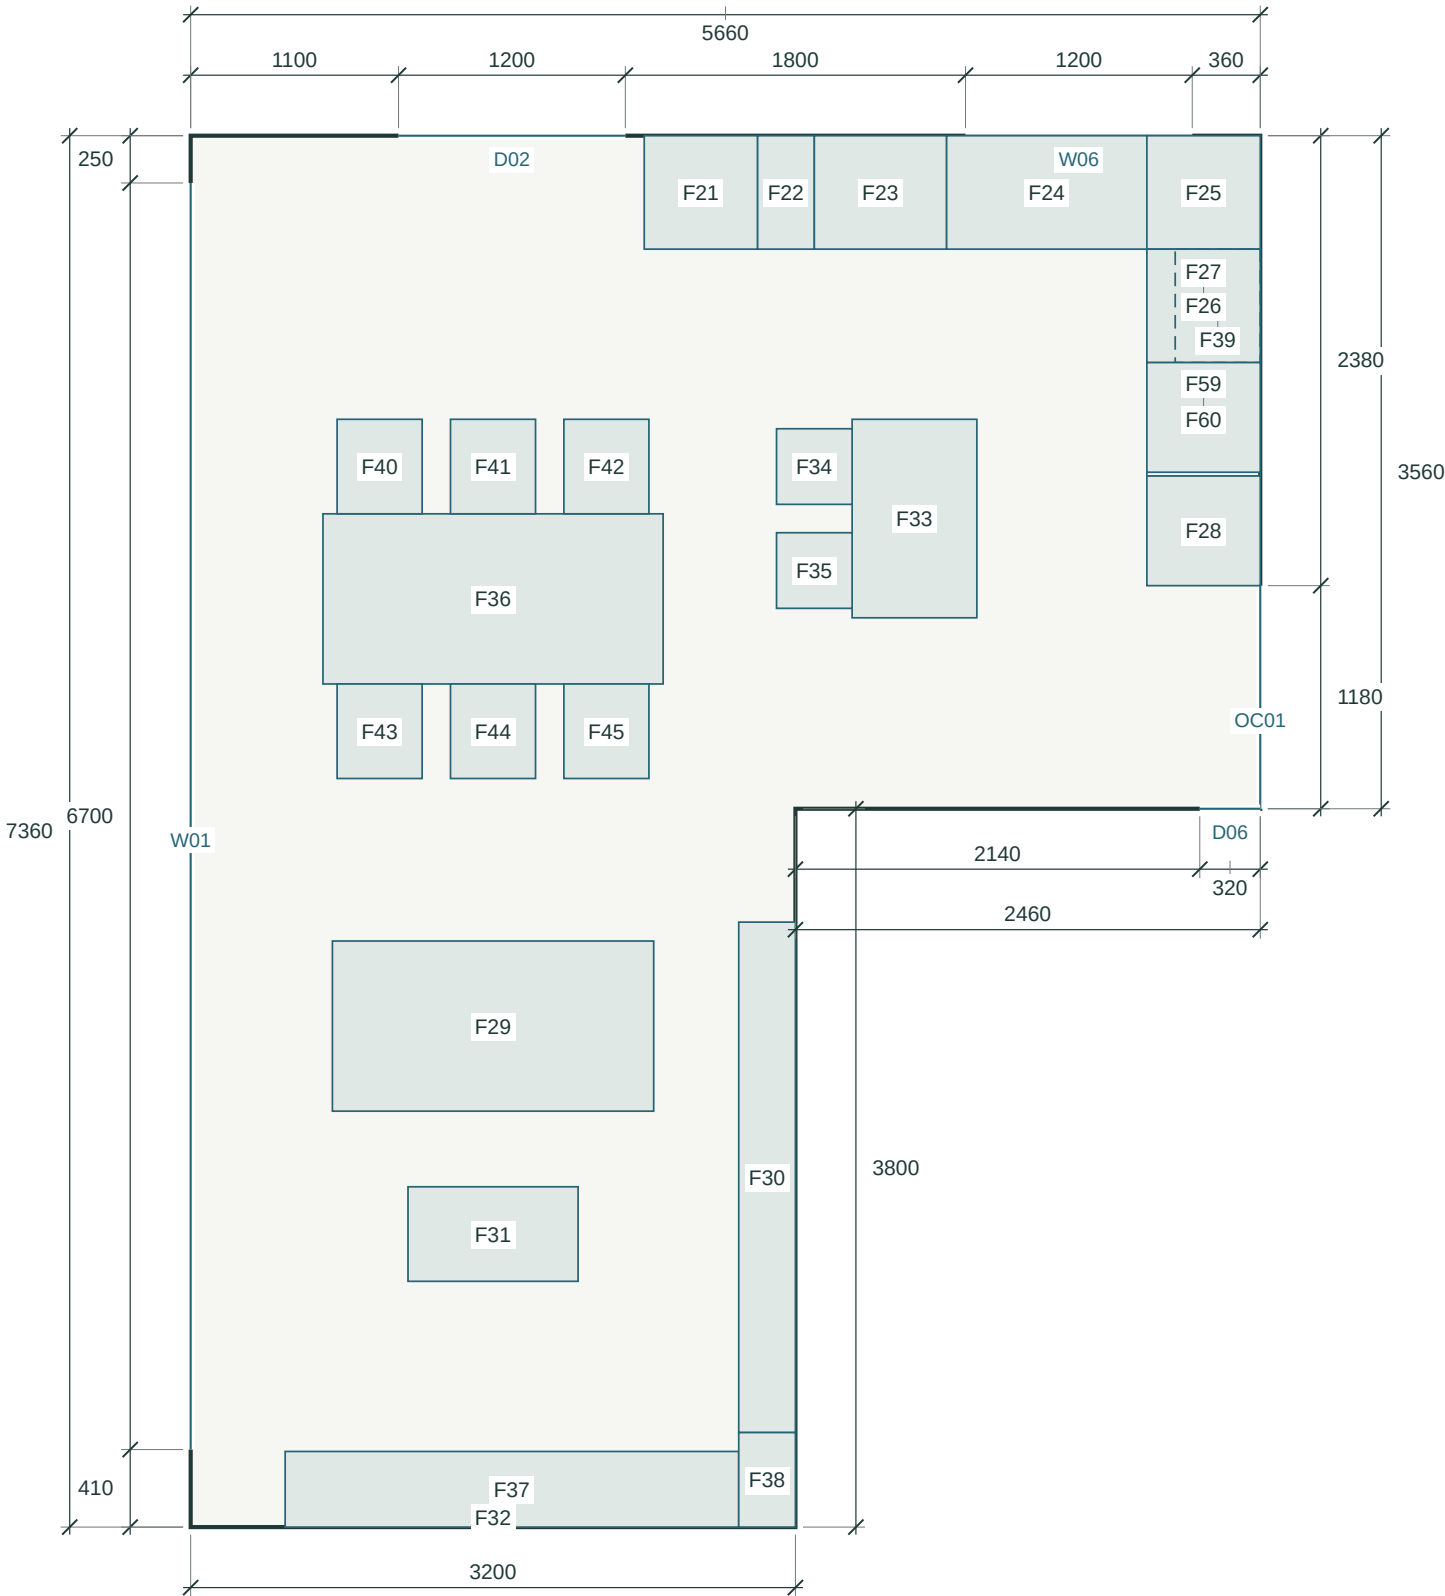

ID · габарит X × Y · ΔX / ΔY


- F21 · 600 × 600 · 2400 / 0**
ПОСУДОМОЙКА 600
- F22 · 300 × 600 · 3000 / 0**
СОРТИРОВКА 300
- F23 · 700 × 600 · 3300 / 0**
МОЙКА 700
- F24 · 1060 × 600 · 4000 / 0**
ПОДГОТОВКА 1060
- F25 · 600 × 600 · 5060 / 0**
УГОЛ 600
- F26 · 600 × 600 · 5060 / 600**
ВАРОЧНАЯ 600
- F27 · 600 × 600 · 5060 / 600**
ДУХОВКА ПОД ВАРОЧНОЙ
- F28 · 600 × 580 · 5060 / 1800**
ХОЛОДИЛЬНИК 600
- F29 · 1700 × 900 · 750 / 4260**
ДИВАН 1700
- F30 · 300 × 2700 · 2900 / 4160**
Шкаф 2700×300 · раздвижные фасады
- F31 · 900 × 500 · 1150 / 5560**
ЖУРН. СТОЛ
- F33 · 660 × 1050 · 3500 / 1500**
PREP-ОСТРОВ 660×1050
- F34 · 400 × 400 · 3100 / 1550**
БАРНЫЙ СТУЛ 1
- F35 · 400 × 400 · 3100 / 2100**
БАРНЫЙ СТУЛ 2

Полная ведомость всех предметов: A302–A304 и CSV. ΔX/ΔY — от верхнего левого угла контура комнаты до верхнего левого угла предмета. Это привязки, не нормативные проходы.

Расположение свободного дивана и стола сохранено; новые 300 мм находятся у западного остекления.

Прихожая и хозяйственный шкаф: стены и мебель

Размеры новой геометрии. Номинальные контрольные грани; не монтажный чертёж.

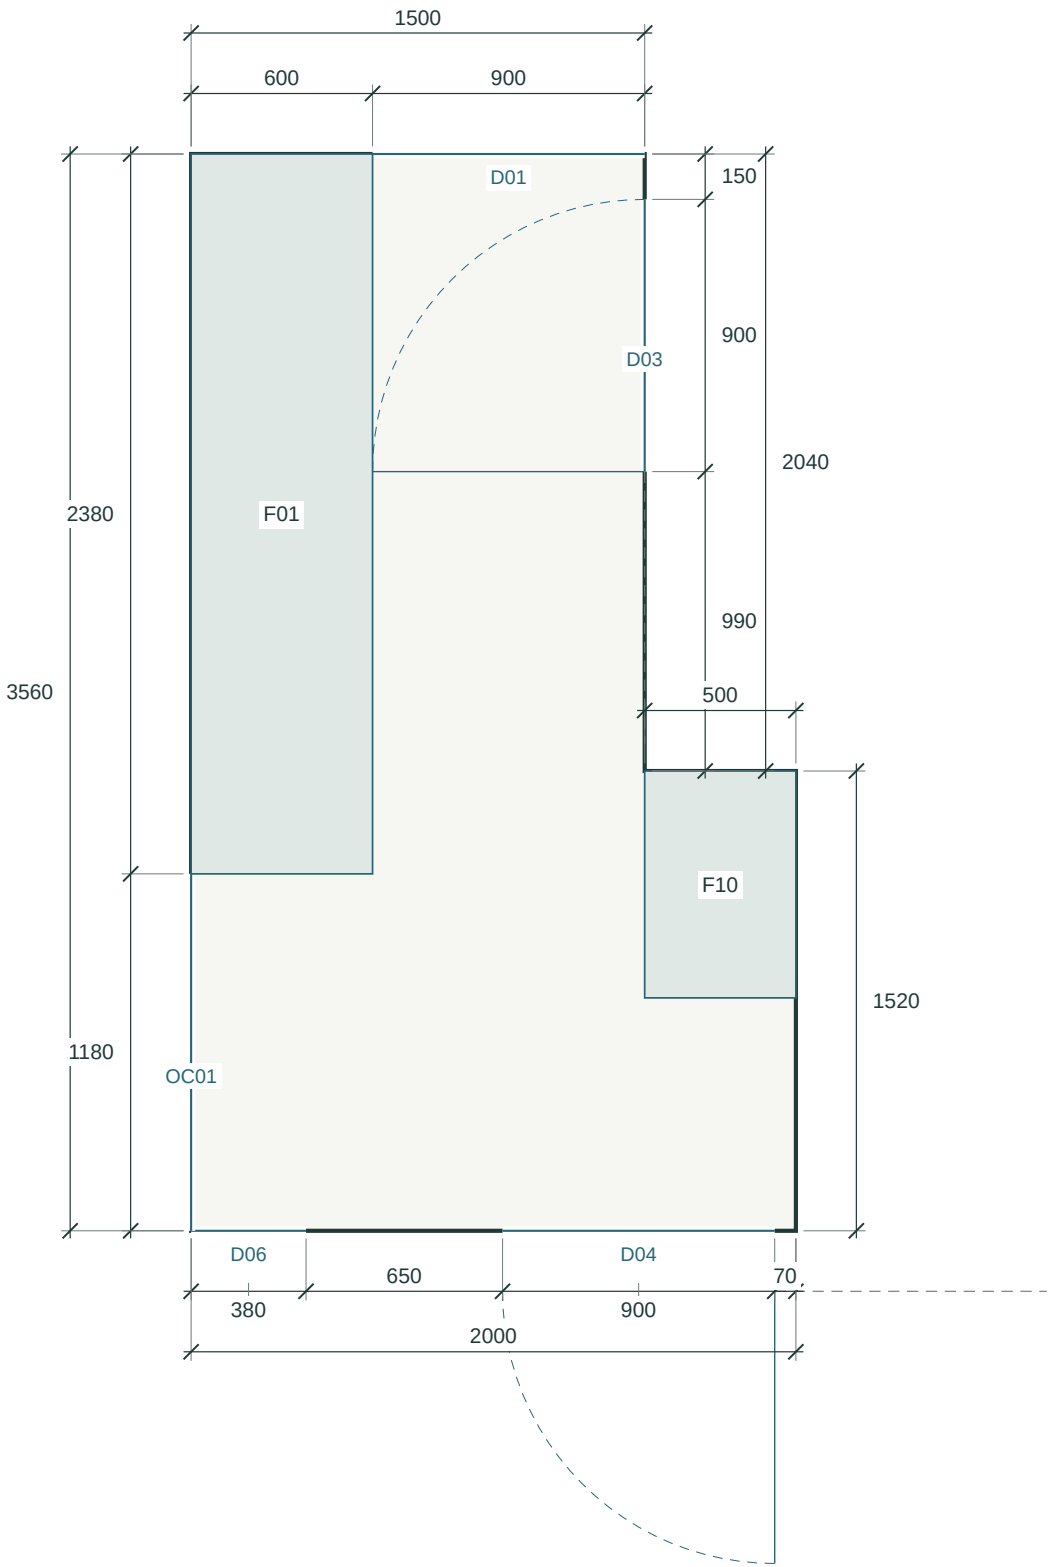

ID · габарит X × Y · ΔX / ΔY

- F01 · 600 × 2380 · 0 / 0**
ШКАФ ПРИХОЖЕЙ 2380
- F10 · 500 × 750 · 1500 / 2040**
ТЕХНИЧЕСКИЙ / ХОЗ. ШКАФ 750 × 500

Полная ведомость всех предметов: A302–A304 и CSV. ΔX/ΔY — от верхнего левого угла контура комнаты до верхнего левого угла предмета. Это привязки, не нормативные проходы.

D01: номинальный восточный простенок 0. Наличник и коробка не решены. Робот у P19 пока без выбранной ниши.

Гостевой санузел и постирочная: стены и мебель

Размеры новой геометрии. Номинальные контрольные грани; не монтажный чертёж.



ID · габарит X × Y · ΔX / ΔY

F15 · 1000 × 1000 · 2200 / 840

Душ 1000×1000

F16 · 650 × 650 · 0 / 1190

Стиральная + сушильная в колонне

F17 · 400 × 550 · 1025 / 1290

Чаша условная 400×550; смотрит на север

F18 · 700 × 400 · 300 / 0


Умывальник 700×400

F20 · 150 × 100 · 1740 / 1740

Узкий ПС: общий резерв 150 × 100


Полная ведомость всех предметов: A302–A304 и CSV. ΔX/ΔY — от верхнего левого угла контура комнаты до верхнего левого угла предмета. Это привязки, не нормативные проходы.

T1 на 250 л: корпус не выбран. Навесные приборы — лист A305. У W03 северный простенок 20 мм; монтаж требует проверки.

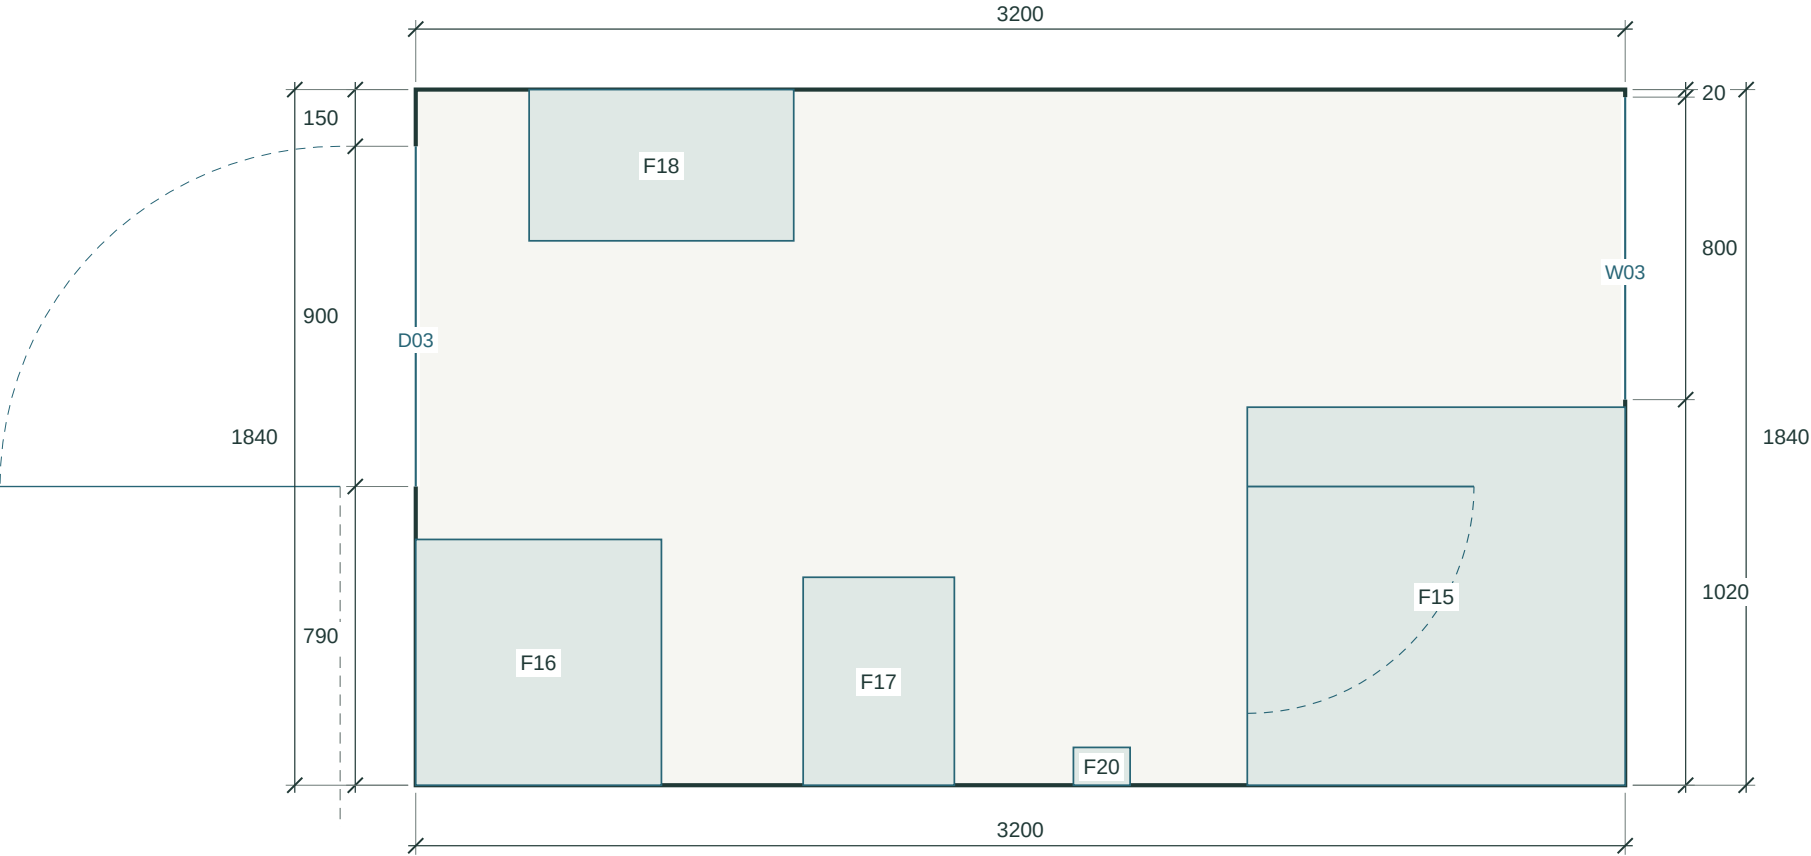

Основной санузел: стены и мебель

Размеры новой геометрии. Номинальные контрольные грани; не монтажный чертёж.

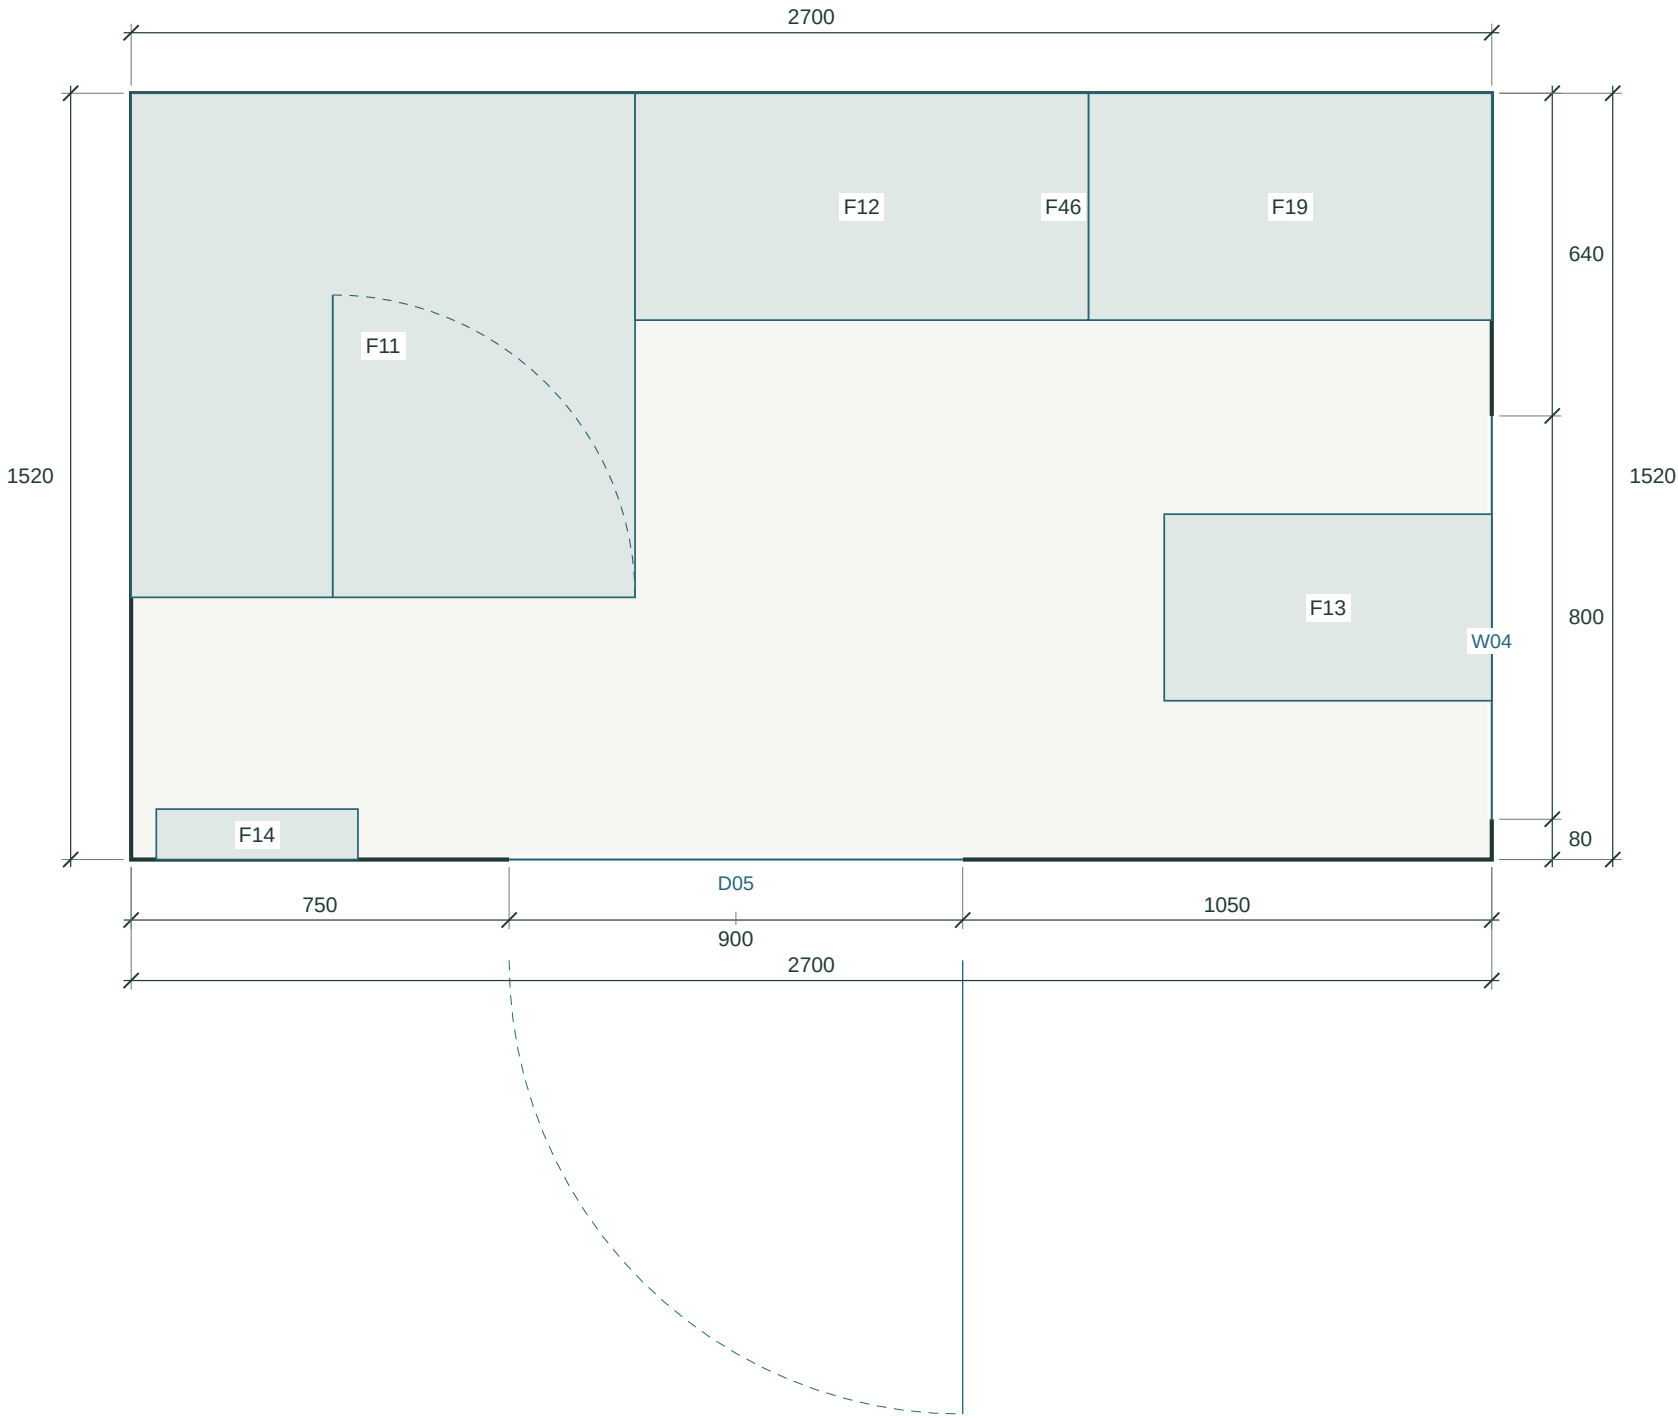

ID · габарит X × Y · ΔX / ΔY


- F11 · 1000 × 1000 · 0 / 0**
ДУШ 1000 × 1000
- F12 · 900 × 450 · 1000 / 0**
РАКОВИНА 900
- F13 · 650 × 370 · 2050 / 835**
WC · КОРПУС УСЛОВНЫЙ
- F14 · 400 × 100 · 50 / 1420**
ПОЛОТЕНЦЕСУШИТЕЛЬ
- F19 · 800 × 450 · 1900 / 0**
Тумба 800 × 450 до восточной стены
- F46 · 1700 × 450 · 1000 / 0**
Столешница 1700 × 450: раковина 900 + тумба 800

Полная ведомость всех предметов: A302–A304 и CSV. ΔX/ΔY — от верхнего левого угла контура комнаты до верхнего левого угла предмета. Это привязки, не нормативные проходы.

Столешница 1700 × 450; тумба хранения 800 × 450. Южный простенок W04 — 80 мм. Инсталляция: не утверждённый монтаж.

Основная спальня: стены и мебель

Размеры новой геометрии. Номинальные контрольные грани; не монтажный чертёж.

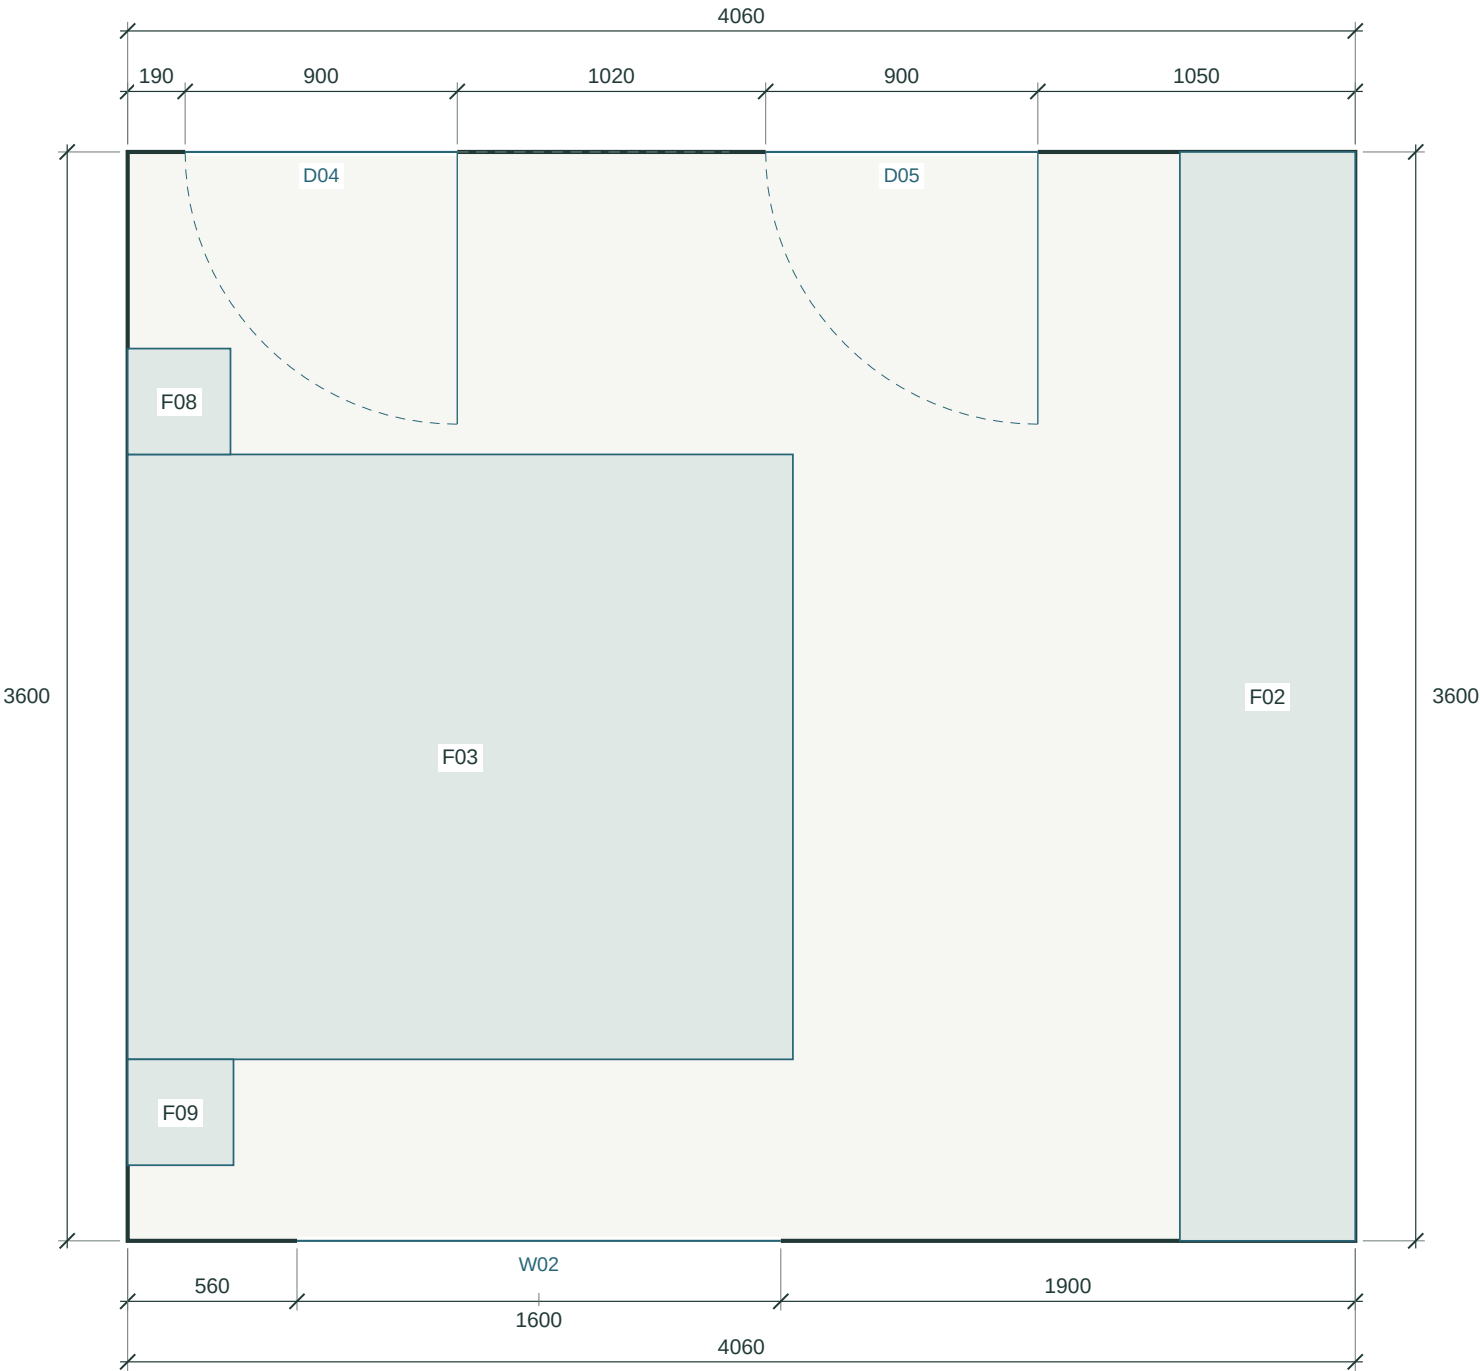

ID · габарит X × Y · ΔX / ΔY

F02 · 580 × 3600 · 3480 / 0
ГАРДЕРОБ MASTER · ВСЯ СТЕНА

F03 · 2200 × 2000 · 0 / 1000
КРОВАТЬ 2000×2200 · У СТЕНЫ

F08 · 340 × 350 · 0 / 650
ТУМБА MASTER NORTH 340 · ROUTE ADJUSTED


F09 · 350 × 350 · 0 / 3000
ТУМБА MASTER SOUTH 350

Полная ведомость всех предметов: A302–A304 и CSV. ΔX/ΔY — от верхнего левого угла контура комнаты до верхнего левого угла предмета. Это привязки, не нормативные проходы.

Гардероб следует новой восточной стене. Кровать и остальные предметы сохраняют прежние координаты.

Вторая спальня: стены и мебель

Размеры новой геометрии. Номинальные контрольные грани; не монтажный чертёж.

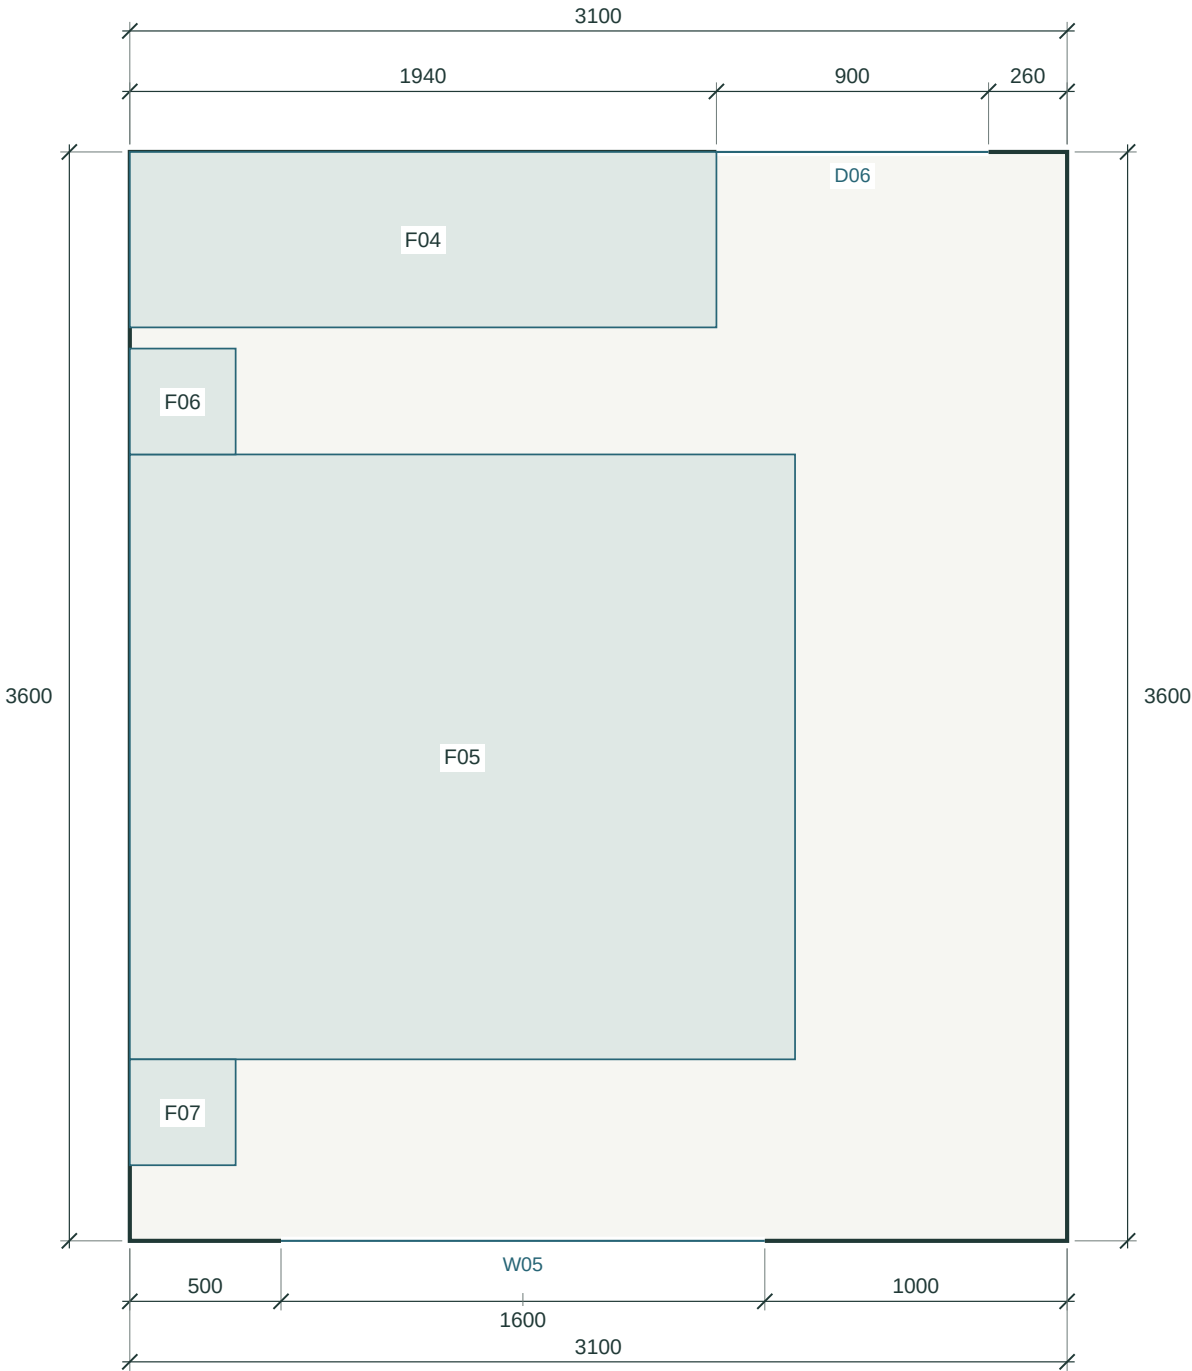

ID · габарит X × Y · ΔX / ΔY

F04 · 1940 × 580 · 0 / 0
ШКАФ СПАЛЬНИ 2 · NORTH · 1940×580

F05 · 2200 × 2000 · 0 / 1000
КРОВАТЬ 2000×2200

F06 · 350 × 350 · 0 / 650
ТУМБА BED 2 NORTH 350

F07 · 350 × 350 · 0 / 3000
ТУМБА BED 2 SOUTH 350

Полная ведомость всех предметов: A302–A304 и CSV. ΔX/ΔY — от
верхнего левого угла контура комнаты до верхнего левого угла предмета.
Это привязки, не нормативные проходы.

Проём D06 начинается у торца шкафа. Между шкафом и кроватью 420
мм в сохранённой модели; пользование не подтверждено.

Лаундж: длинный диван вместо северного ряда

Север сверху, озеро на западе. Номинальная закрытая расстановка; не проверка открытых створок.



Проёмы: координаты, ширины и графические уровни

Размеры новой геометрии. Номинальные контрольные грани; не монтажный чертёж.

ID	Грань / ось	Начало X / Y	Ширина	Низ / верх*	До заказа уточнить
D02	север / X	1200 / 0	1200	0 / 2400	коробка, монтаж, чистый
W06	север / X	4200 / 0	1200	1000 / 2200	коробка, монтаж, чистый
D01	север / X	6560 / 0	900	0 / 2400	коробка, монтаж, чистый
W03	восток / Y	11260 / 420	800	2000 / 2900	коробка, монтаж, чистый
W04	восток / Y	11260 / 3080	800	2000 / 2900	коробка, монтаж, чистый
W05	юг / X	4000 / 8160	1600	0 / 2400	коробка, монтаж, чистый
W02	юг / X	7360 / 8160	1600	0 / 2400	коробка, монтаж, чистый
W01	запад / Y	-300 / 650	6700	0 / 3000	коробка, монтаж, чистый
OC01	внутренняя / Y	5860 / 2780	1180	0 / 3000	коробка, монтаж, чистый
D03	внутренняя / Y	7560 / 550	900	0 / 2100	коробка, монтаж, чистый
D04	внутренняя / X	6990 / 4060	900	0 / 2100	коробка, монтаж, чистый
D05	внутренняя / X	8910 / 4060	900	0 / 2100	коробка, монтаж, чистый
D06	внутренняя / X	5440 / 4060	900	0 / 2100	коробка, монтаж, чистый

* Низ и верх сохранены из графической модели P73, не являются утверждёнными монтажными отметками. Отсчёт от условного чистого пола ±0.000. Ширина номинальная; начало — западный либо северный конец проёма. Конструктивные перемычки, коробки и чистый проход: ТВС.



Мебель и оборудование · 1 / 3

Размеры новой геометрии. Номинальные контрольные грани; не монтажный чертёж.

ID	Предмет / постоянный ID	X × Y, мм	X / Y, мм	Н, мм	Класс
F01	ШКАФ ПРИХОЖЕЙ 2380 P26-A-HALL · P26-A-HALL-ST	600 × 2380	5960 / 400	TBC	корпус
F02	ГАРДЕРОБ MASTER · ВСЯ СТЕНА P26-A-R04 · P26-A-MW	580 × 3600	10280 / 4160	TBC	корпус
F03	КРОВАТЬ 2000×2200 · У СТЕНЫ P26-A-R04 · P26-A-MBED	2200 × 2000	6800 / 5160	TBC	корпус
F04	ШКАФ СПАЛЬНИ 2 · NORTH · 1940×580 P26-A-R05 · P26-A-B2W	1940 × 580	3500 / 4160	TBC	корпус
F05	КРОВАТЬ 2000×2200 P26-A-R05 · P26-A-B2BED	2200 × 2000	3500 / 5160	TBC	корпус
F06	ТУМБА BED 2 NORTH 350 P26-A-R05 · P26-A-B2-NS-N	350 × 350	3500 / 4810	TBC	корпус
F07	ТУМБА BED 2 SOUTH 350 P26-A-R05 · P26-A-B2-NS-S	350 × 350	3500 / 7160	TBC	корпус
F08	ТУМБА MASTER NORTH 340 · ROUTE ADJUSTED P26-A-R04 · P26-A-M-NS-N	340 × 350	6800 / 4810	TBC	корпус
F09	ТУМБА MASTER SOUTH 350 P26-A-R04 · P26-A-M-NS-S	350 × 350	6800 / 7160	TBC	корпус
F10	ТЕХНИЧЕСКИЙ / ХОЗ. ШКАФ 750 × 500 P26-A-HALL · P49-HALL-LINEN-01	500 × 750	7460 / 2440	1800	корпус
F11	ДУШ 1000 × 1000 P26-A-R03 · P50-M-SH	1000 × 1000	8160 / 2440	TBC	корпус
F12	РАКОВИНА 900 P26-A-R03 · P50-M-BASIN	900 × 450	9160 / 2440	TBC	корпус
F13	УС · КОРПУС УСЛОВНЫЙ P26-A-R03 · P50-M-WC-BODY	650 × 370	10210 / 3275	TBC	корпус
F14	ПОЛОТЕНЦЕСУШИТЕЛЬ P26-A-R03 · P51-M-TW	400 × 100	8210 / 3860	1000	корпус
F15	Душ 1000×1000 P26-A-R02 · P50-G-SH	1000 × 1000	9860 / 1240	2100	корпус
F16	Стиральная + сушильная в колонне P26-A-R02 · P50-G-WD	650 × 650	7660 / 1590	1800	корпус
F17	Чаша условная 400×550; смотрит на север P26-A-R02 · P50-G-WC	400 × 550	8685 / 1690	TBC	корпус
F18	Умывальник 700×400 P26-A-R02 · P50-G-BASIN	700 × 400	7960 / 400	850	корпус
F19	Тумба 800 × 450 до восточной стены P26-A-R03 · P53-M-JOINERY	800 × 450	10060 / 2440	850	корпус
F20	Узкий ПС: общий резерв 150 × 100 P26-A-R02 · P53-G-TW	150 × 100	9400 / 2140	1000	корпус

57 позиций инвентаря: F61 заменяет четыре северных стула. Все значения — номинальные проектные габариты, не заказные размеры. Полные названия, координаты, высоты и источники — в CSV/JSON. Печная ниша Н показана отдельно на A207.

Мебель и оборудование · 2 / 3

Размеры новой геометрии. Номинальные контрольные грани; не монтажный чертёж.

ID	Предмет / постоянный ID	X × Y, мм	X / Y, мм	Н, мм	Класс
F21	ПОСУДОМОЙКА 600 P26-A-R01 · P26-A-DW	600 × 600	2500 / 400	TBC	корпус
F22	СОРТИРОВКА 300 P26-A-R01 · P26-A-WASTE	300 × 600	3100 / 400	TBC	корпус
F23	МОЙКА 700 P26-A-R01 · P26-A-SINK	700 × 600	3400 / 400	TBC	корпус
F24	ПОДГОТОВКА 1060 P26-A-R01 · P26-A-PREP	1060 × 600	4100 / 400	TBC	корпус
F25	УГОЛ 600 P26-A-R01 · P26-A-CORNER	600 × 600	5160 / 400	TBC	корпус
F26	ВАРОЧНАЯ 600 P26-A-R01 · P26-A-HOB	600 × 600	5160 / 1000	TBC	поверхность
F27	ДУХОВКА ПОД ВАРОЧНОЙ P26-A-R01 · P26-A-OVEN	600 × 600	5160 / 1000	600	корпус
F28	ХОЛОДИЛЬНИК 600 P26-A-R01 · P26-A-FR	600 × 580	5160 / 2200	TBC	корпус
F29	ДИВАН 1700 P26-A-R01 · P26-A-S01	1700 × 900	850 / 4660	TBC	корпус
F30	Шкаф 2700×300 · раздвижные фасады P26-A-R01 · P26-A-LIV-ST	300 × 2700	3000 / 4560	TBC	корпус
F31	ЖУРН. СТОЛ P26-A-R01 · P26-A-CT	900 × 500	1250 / 5960	TBC	корпус
F32	TV 86in · VISIBLE 1904×1071 NOMINAL P26-A-R01 · P26-A-TV	1904 × 100	748 / 7660	TBC	верхняя проекция
F33	PREP-ОСТРОВ 660×1050 P26-A-R01 · P26-A-ISL01	660 × 1050	3600 / 1900	TBC	корпус
F34	БАРНЫЙ СТУЛ 1 P26-A-R01 · P26-A-BAR01	400 × 400	3200 / 1950	TBC	корпус
F35	БАРНЫЙ СТУЛ 2 P26-A-R01 · P26-A-BAR02	400 × 400	3200 / 2500	TBC	корпус
F36	СТОЛ 1800×900 · 6 P26-A-R01 · P26-A-T01	1800 × 900	800 / 2400	TBC	корпус
F37	Тумба под ТВ 2400×400 P26-A-R01 · P60-MEDIA-BASE	2400 × 400	600 / 7360	TBC	корпус
F38	Угловое завершение 500×300 P26-A-R01 · P60-CORNER-BASE	300 × 500	3000 / 7260	TBC	корпус
F39	ВЫТЯЖКА — МОДЕЛЬ / ЗАЗОР TBC P26-A-R01 · P68-K-HOOD	450 × 600	5310 / 1000	80	верхняя проекция
F40	Обеденный стул — графическая примерка P26-A-R01 · P58-GRAPHIC-DINING-N1	450 × 500	875 / 1900	800	корпус

57 позиций инвентаря: F61 заменяет четыре северных стула. Все значения — номинальные проектные габариты, не заказные размеры. Полные названия, координаты, высоты и источники — в CSV/JSON. Печная ниша Н показана отдельно на A207.

Мебель и оборудование · 3 / 3

Размеры новой геометрии. Номинальные контрольные грани; не монтажный чертёж.

ID	Предмет / постоянный ID	X × Y, мм	X / Y, мм	H, мм	Класс
F41	Обеденный стул — графическая примерка P26-A-R01 · P58-GRAPHIC-DINING-N2	450 × 500	1475 / 1900	800	корпус
F42	Обеденный стул — графическая примерка P26-A-R01 · P58-GRAPHIC-DINING-N3	450 × 500	2075 / 1900	800	корпус
F43	Обеденный стул — графическая примерка P26-A-R01 · P58-GRAPHIC-DINING-S1	450 × 500	875 / 3300	800	корпус
F44	Обеденный стул — графическая примерка P26-A-R01 · P58-GRAPHIC-DINING-S2	450 × 500	1475 / 3300	800	корпус
F45	Обеденный стул — графическая примерка P26-A-R01 · P58-GRAPHIC-DINING-S3	450 × 500	2075 / 3300	800	корпус
F46	Столешница 1700 × 450: раковина 900 + тумба 800 P26-A-R03 · P53-M-COUNTERTOP	1700 × 450	9160 / 2440	TBC	поверхность
F47	Обеденный стол 2800 × 1000: 4 + 4 боковых места, без торцевых P73-LOUNGE · P53-OUT-B-TABLE	2800 × 1000	1500 / -3600	TBC	корпус
F48	Моечная столешница 2000 × 700 P73-LOUNGE · P53-OUT-B-WORKTOP	2000 × 700	4300 / -700	TBC	корпус
F49	Нержавеющая мойка 800 × 600: пробный общий габарит, чаша неизвестна P73-LOUNGE · P53-OUT-B-SINK	800 × 600	5450 / -650	TBC	поверхность
F54	Стул 520 × 550: условный корпус P73-LOUNGE · P53-OUT-B-SEAT-S1	520 × 550	1590 / -2500	TBC	корпус
F55	Стул 520 × 550: условный корпус P73-LOUNGE · P53-OUT-B-SEAT-S2	520 × 550	2290 / -2500	TBC	корпус
F56	Стул 520 × 550: условный корпус P73-LOUNGE · P53-OUT-B-SEAT-S3	520 × 550	2990 / -2500	TBC	корпус
F57	Стул 520 × 550: условный корпус P73-LOUNGE · P53-OUT-B-SEAT-S4	520 × 550	3690 / -2500	TBC	корпус
F58	Печь-камин — визуальный резерв P73-LOUNGE · P62-MASONRY-01	1100 × 600	2800 / -700	2100	корпус
F59	МОРОЗИЛЬНИК ОТДЕЛЬНЫЙ ПОД СТОЛЕШНИЦЕЙ P26-A-R01 · P78-K-FREEZER	600 × 580	5160 / 1600	850	корпус
F60	СТОЛЕШНИЦА НАД МОРОЗИЛЬНИКОМ P26-A-R01 · P78-K-FREEZER-TOP	600 × 600	5160 / 1600	30	поверхность
F61	Длинный обеденный диван у северного стекла P73-LOUNGE · P81-L-SOFA	3000 × 650	1400 / -4300	880	корпус

57 позиций инвентаря: F61 заменяет четыре северных стула. Все значения — номинальные проектные габариты, не заказные размеры. Полные названия, координаты, высоты и источники — в CSV/JSON. Печная ниша H показана отдельно на A207.

ДЛЯ СОГЛАСОВАНИЯ / НЕ ДЛЯ СТРОИТЕЛЬСТВА

P82-A304


P82: P81 интерьер + сохранённые технические задания. Изделия, расчёты и монтаж: TBC.

M NTS / мм / A3

Подготовка: Codex / AI. Проверяющий и утверждающий специалист: не назначены.

План потолков: свод гостиной и плоская кухня

План сверху. X — восток, Y — юг. Не план несущих балок.

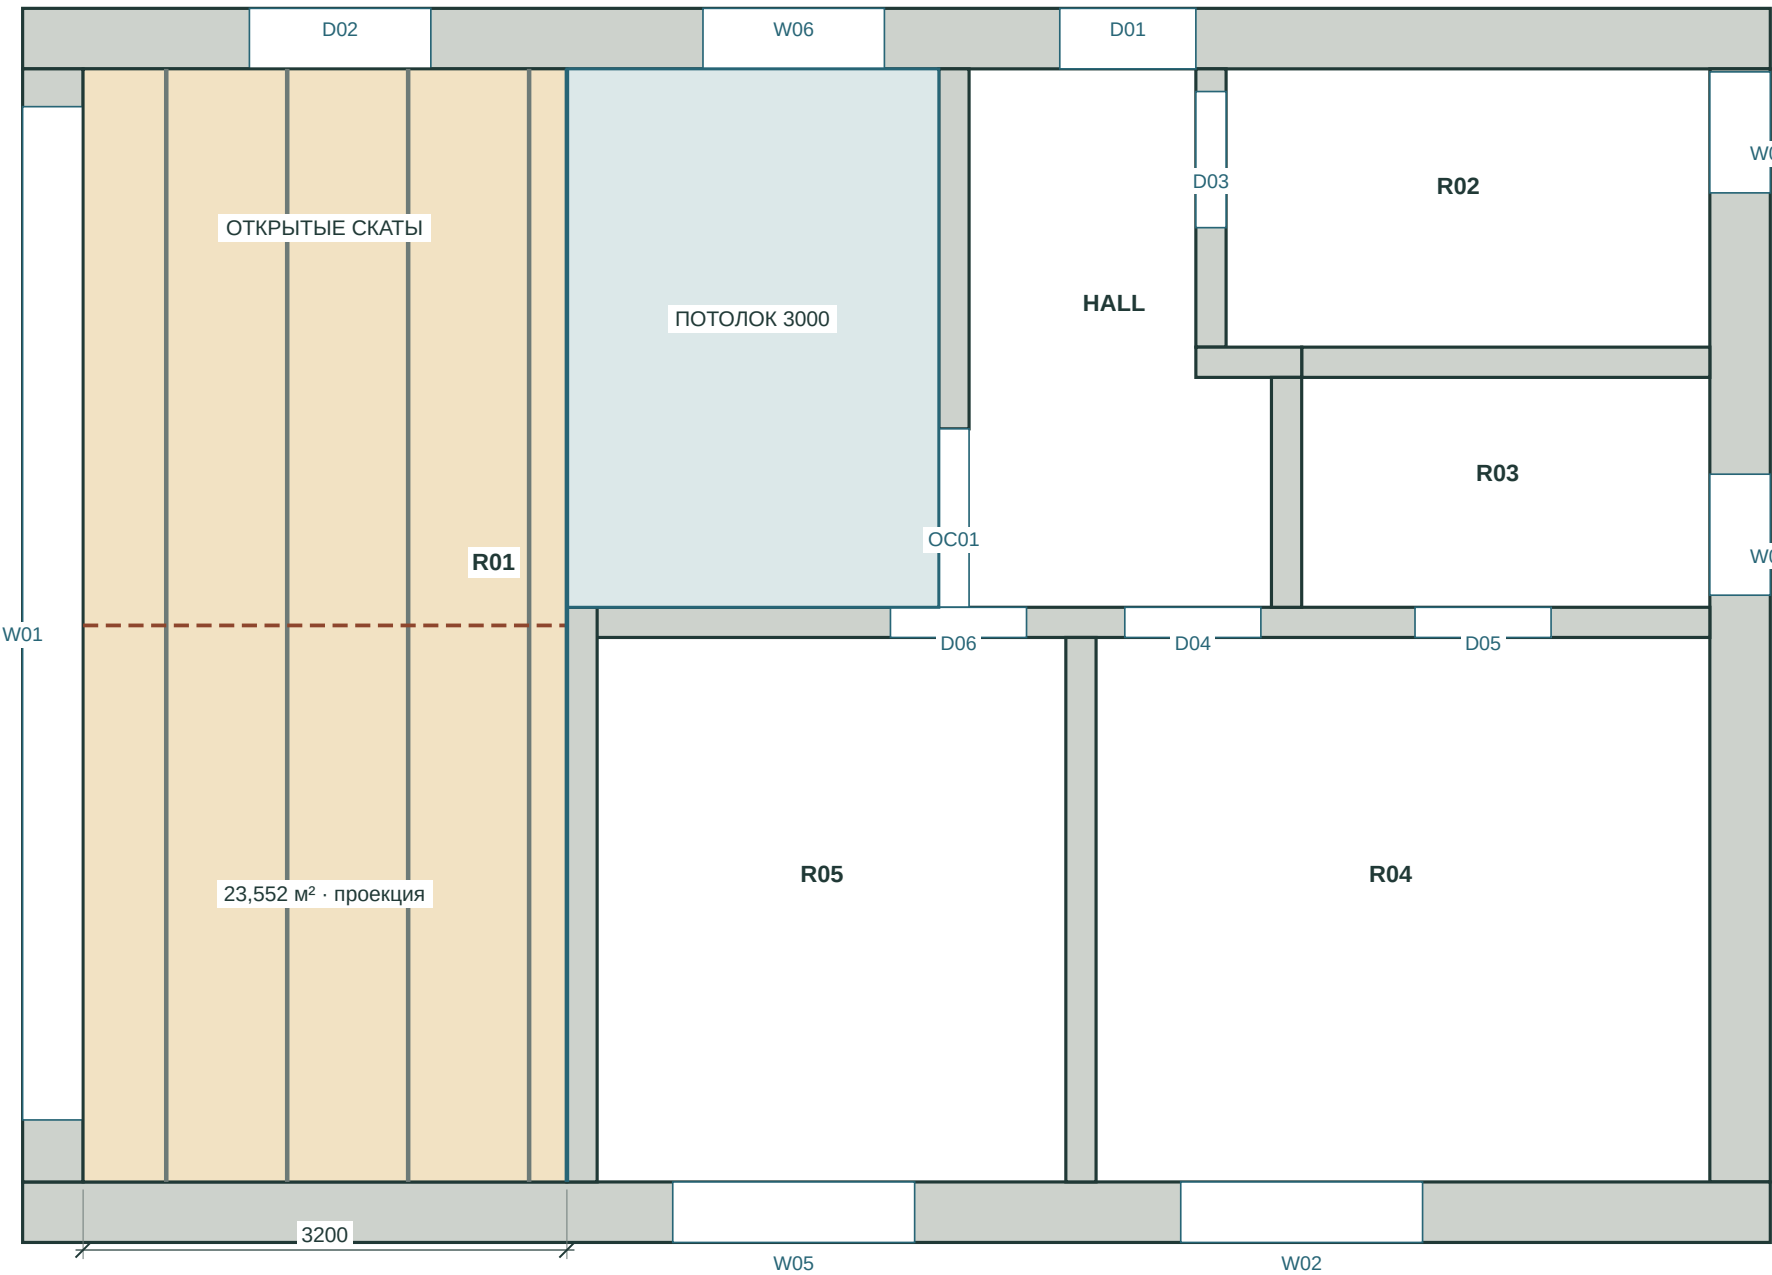

Граница X=3300

Продолжает линию западной стены спальни. Над кухней нет новой стены до пола: только верхняя плоскость перехода.

Пробные отметки

Края подшивки +3.117; конёк +4.650. Кровля снаружи не поднята. Видимые элементы на 100 ниже подшивки — графика, не полное сечение.

Остальные комнаты


Прихожая, спальни и санузлы — плоский потолок +3.000. Наружные проёмы не увеличены по высоте.

Вечерний свет

Скрытая линия вдоль перехода X=3300. Тип профиля, драйвер, световой поток и монтажная ниша ТВС.

Разрез гостиной по скатам: север — юг

X=1700, взгляд на восток. Север слева, юг справа. Высоты от условного чистого пола.

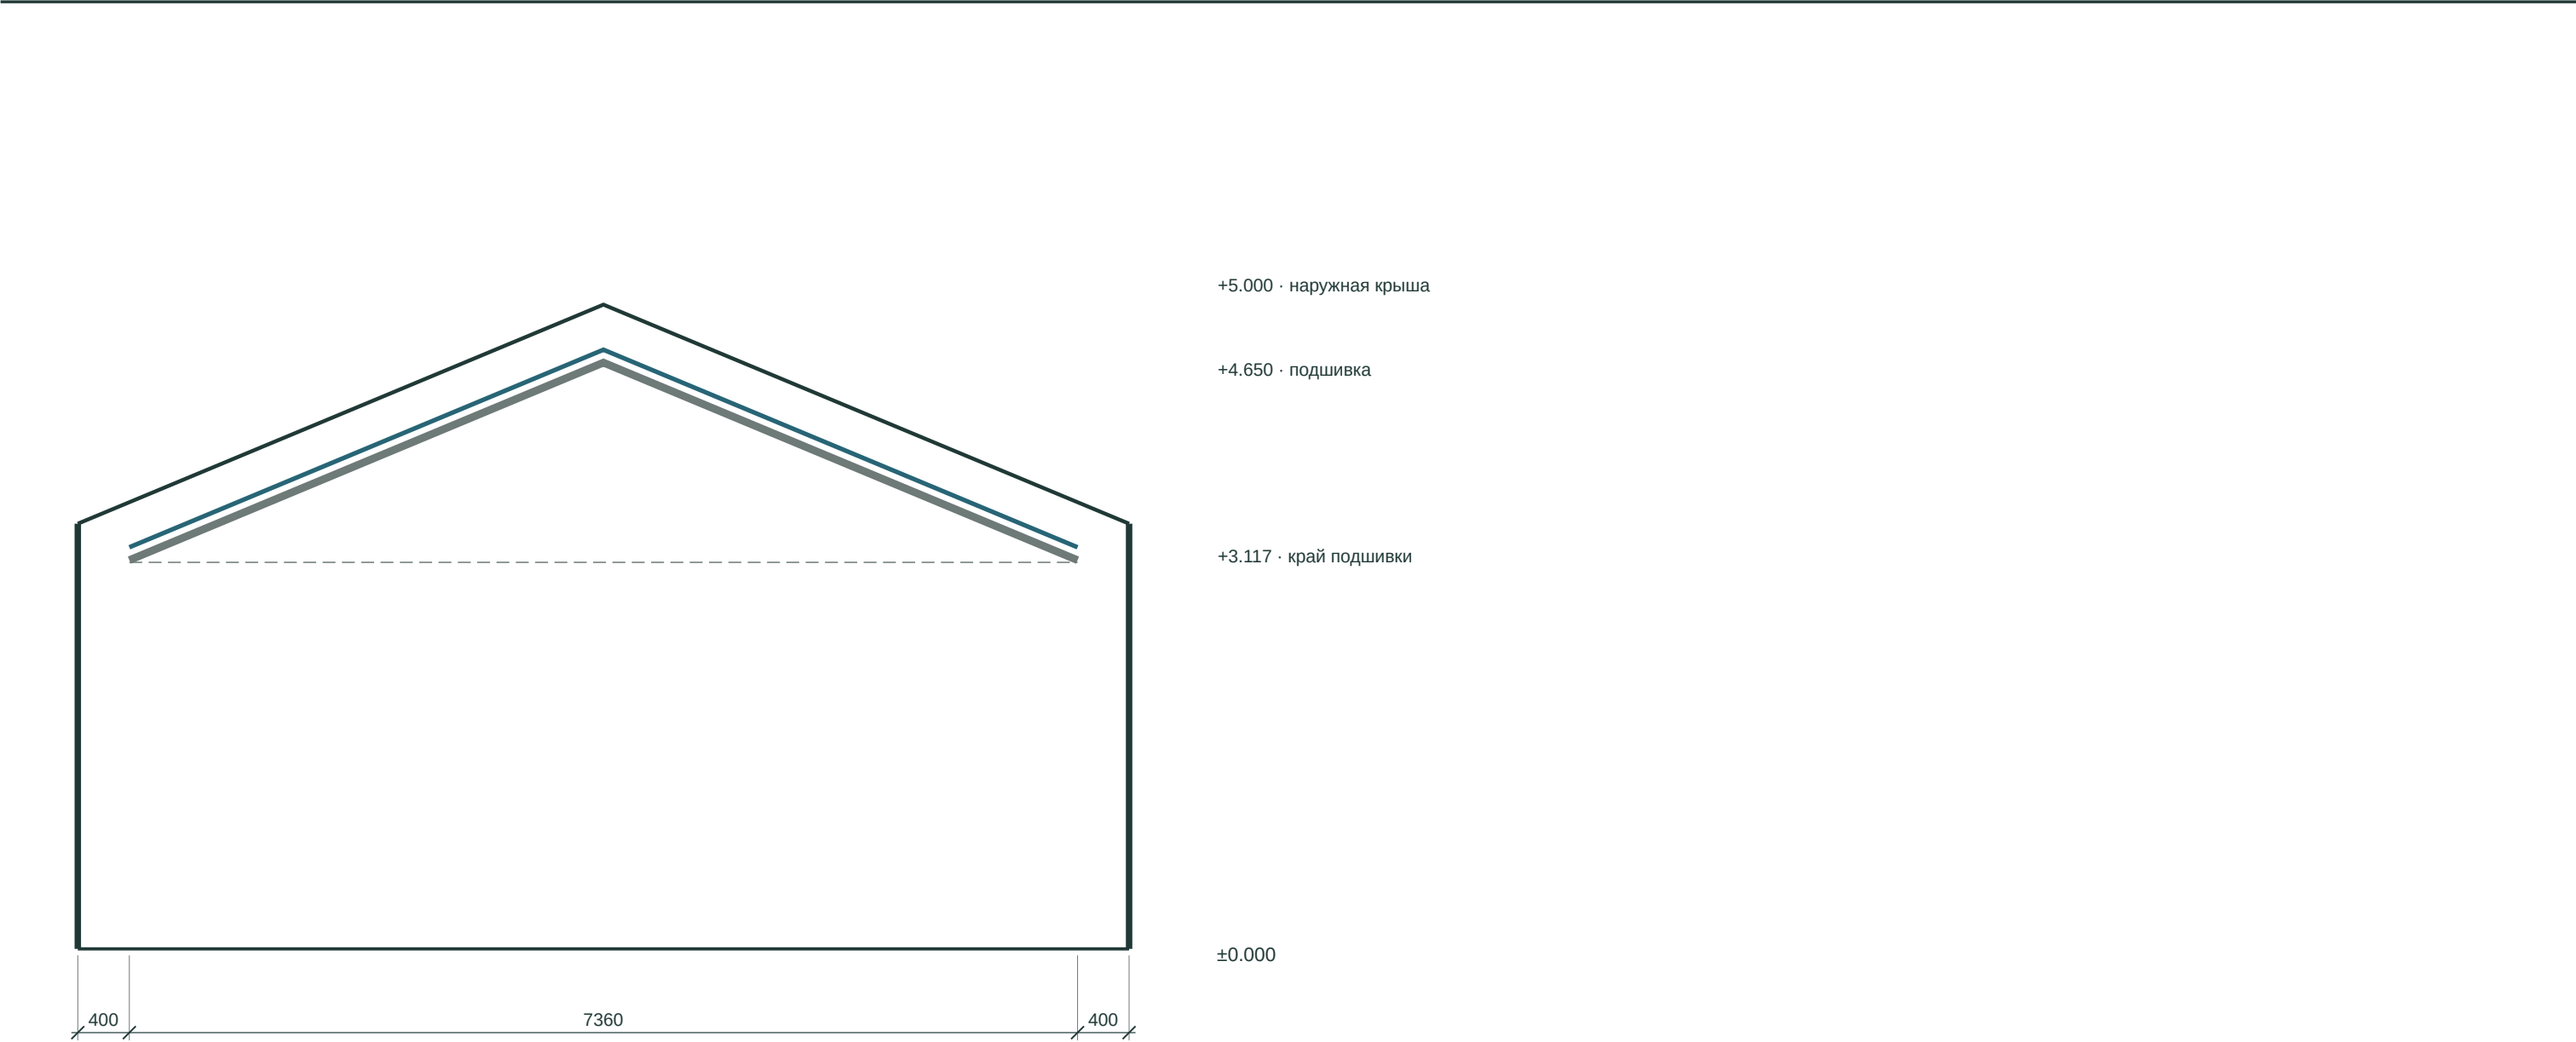

350 мм — вертикальное расстояние между условной наружной крышей и пробной подшивкой. Это НЕ толщина утеплителя. После расчёта конструкций и кровельного пирога внутренние отметки могут измениться.

Не удалять затяжки/фермы ради этого вида. Несущую схему, опоры, прогибы, распор и узлы назначает конструктор. Верхняя поверхность перехода к плоскому потолку должна замыкать тепловой и воздушный контуры.

Кухня: отдельный морозильник и сохранённый проход


Примерка отдельного подстольного прибора. Не заказ кухни или техники.

Север слева; юг справа. Вид из кухни на восточную стену.

F59: пробный модуль 600 × 580 × 850, фронт обращён на запад. F60: рабочая поверхность на 900. Это не паспорт выбранного морозильника.

Высокий морозильник в прежнем ряду либо примыкает к варочной, либо перекрывает проход. Для двух высоких приборов нужна отдельная перекомпоновка кухни.


Проход у острова с закрытой техникой 900. При условной дверце580 остаётся320 до острова: это не доказанный сервисный/пользовательский проход.

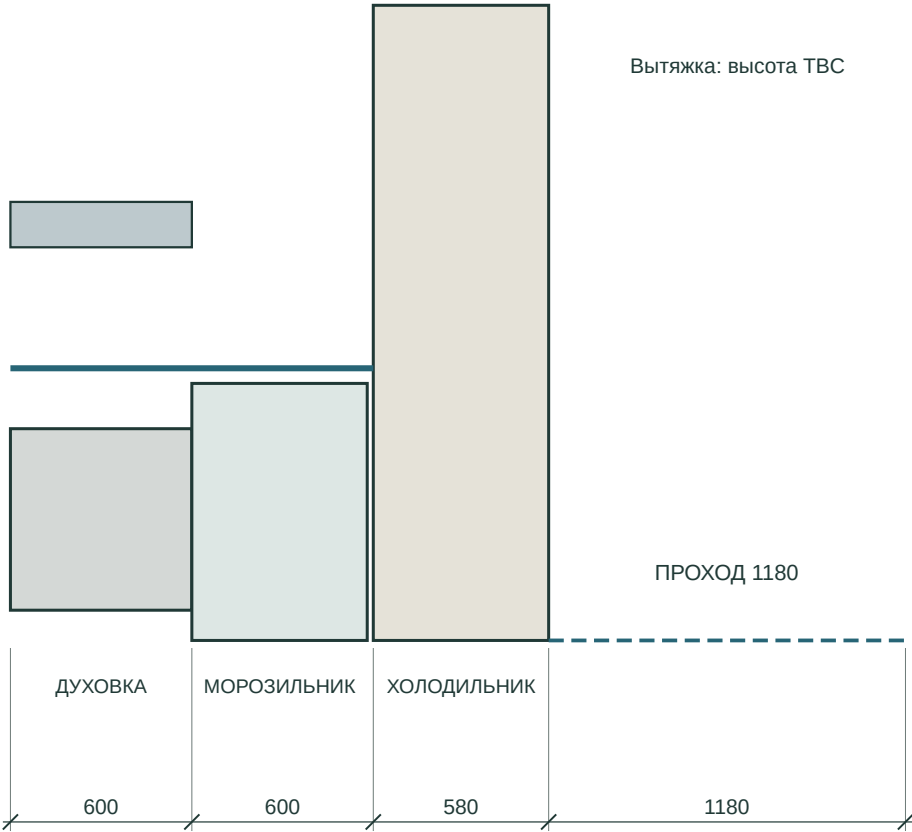

Проверить конкретные модели: тепло от варочной, вентиляция, полный выкат ящиков, место человеку, доступ к розетке и замена прибора. Электрическая точка F59 отдельная; цепь и монтажная высота ТВС.

Полы: паркет в жилых зонах, плитка в остальных

Север сверху; озеро на западе. Граница покрытий Х=3300. Чистые толщины ещё не подобраны.

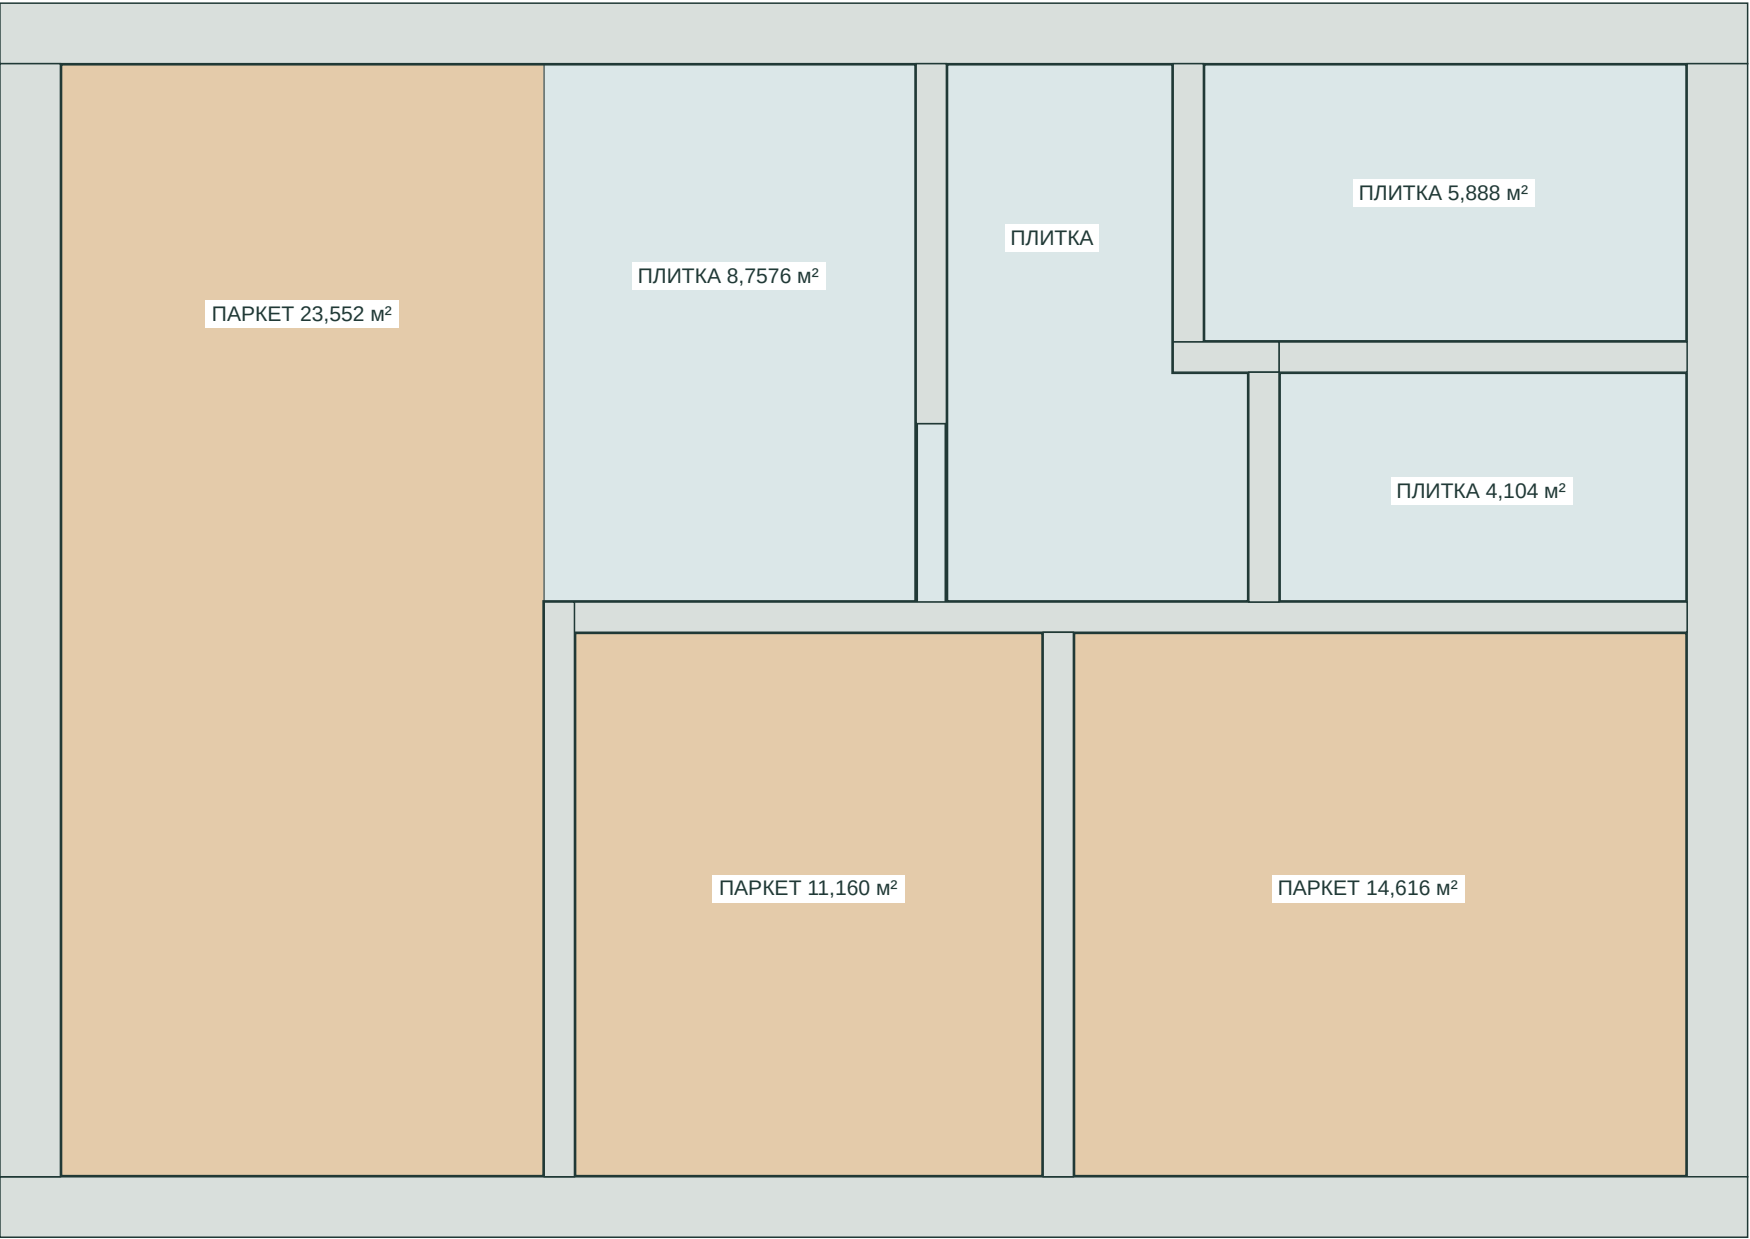

Паркет

Гостиная и столовая западнее Х3300; обе спальни. Светлый дуб, прямая укладка - вариант палитры, не заказ изделия.

Плитка

Кухня, прихожая, два санузла; проход кухня-прихожая и закрытый лаундж отдельно.

Переходы

Стремимся к одному уровню чистого пола. Перепады компенсировать проектом основания, не предположением одинаковой толщины паркета и плитки.

Терраса

Открытая деревянная терраса сохранена. Зона холодной примерки мангала и казана - А407, без разрешения растопки.

Площади по границам зон модели, включая места под мебелью. Пороги/монтажные зазоры/раскрой/запас и фактические толщины считаются отдельно. Не закупочная ведомость.

Отделка и площади: что можно передать для сметы

Координационная примерка. Не инструкция для монтажа.

Полы по помещениям

Паркет: 49,328 м². Плитка в границах комнат дома: 24,8496 м². Открытый проход кухня-прихожая отдельно: 0,236 м². Закрытый лаундж: 41,160 м². Это границы поверхностей, не количество для закупки.

Потолки дома

Вагонка: скаты 25,514667 м²; плоские зоны без санузлов 40,6336 м²; портал отдельно 0,236 м². Натяжные потолки санузлов: 9,992 м². Видимые грани балок, ниши, доборы, зазоры и раскрой считаются отдельно.

Навес

Подшивка в горизонтальной пробной плоскости: 71,834 м² до вычета проходки/зазоров. В том числе закрытый лаундж 41,160 м². Фактическая поверхность после решения уклона и деталей изменится.

Паркет и плитка

Точные толщина, основание, клей/подложка, температурные ограничения и влажность - по выбранным изделиям. Стык покрытий на X3300 и пороги увязать с чистым полом без случайного перепада.

Дерево и натяжной потолок

Утвердить образцы при дневном и вечернем свете. Вагонку и основание проверить для режима помещения. В санузлах приборы крепятся к отдельному основанию/платформе, не к полотну; ревизии коммуникаций сохранить.

Не включено

Запас, отходы, нахлёсты, плинтусы, раскладка, крепления, инженерные материалы и цены не назначены. Площади старых листов обмера геометрии не являются выбранным составом пирогов.

Навес: высота и защита от летнего нагрева

Координационная примерка. Не инструкция для монтажа.

Факт текущей модели

Условный пол ±0.000. Стекло +2.940. Прежняя плоскость навеса +3.100, без установленного уклона, толщины и опор. Абсолютная отметка пола над участком неизвестна.

Предлагаемая чистая высота

Цель примерки +3.000 до подшивки. Между +3.000 и прежней плоскостью только 100 мм: это НЕ резерв, в котором доказан полный пирог. Поднимать крышу или опускать стекло без координации нельзя.

Концепция слоёв, не монтажный узел

Фальцевая кровля и водозащитная система → проветриваемая кровельная полость → тепловой контур → согласованное воздухопароограничение → сервисная зона → светлая деревянная подшивка. Порядок конкретных мембран и толщины определить по выбранной системе и расчёту.

Почему не просто фольга

Обычный утеплитель уменьшает передачу тепла; отражающий слой работает иначе и требует воздушного пространства. Его нельзя считать заменой полноценного утепления или гарантией прохлады. Источник P79-S01: DOE, Types of Insulation, раздел How.

Периодическое отопление


Лаундж то холодный, то прогревается. Нужны теплотехническая и влажностная проверки, непрерывность контура, вентиляция и влагостойкость покрытия. Толщина утеплителя и время прогрева пока неизвестны.

Проверка до изготовления

Архитектор + конструктор + специалист по оболочке: односкатный уклон, примыкание к основной крыше, опоры, вода/перелив, верх стекла и проходка дымохода. Эта картинка не подтверждает летнюю температуру потолка.

Мангал 1000 и казан 20 л: северная открытая часть

Показаны холодные приборы. Это не разрешённое место эксплуатации и не готовое огнезащитное основание.

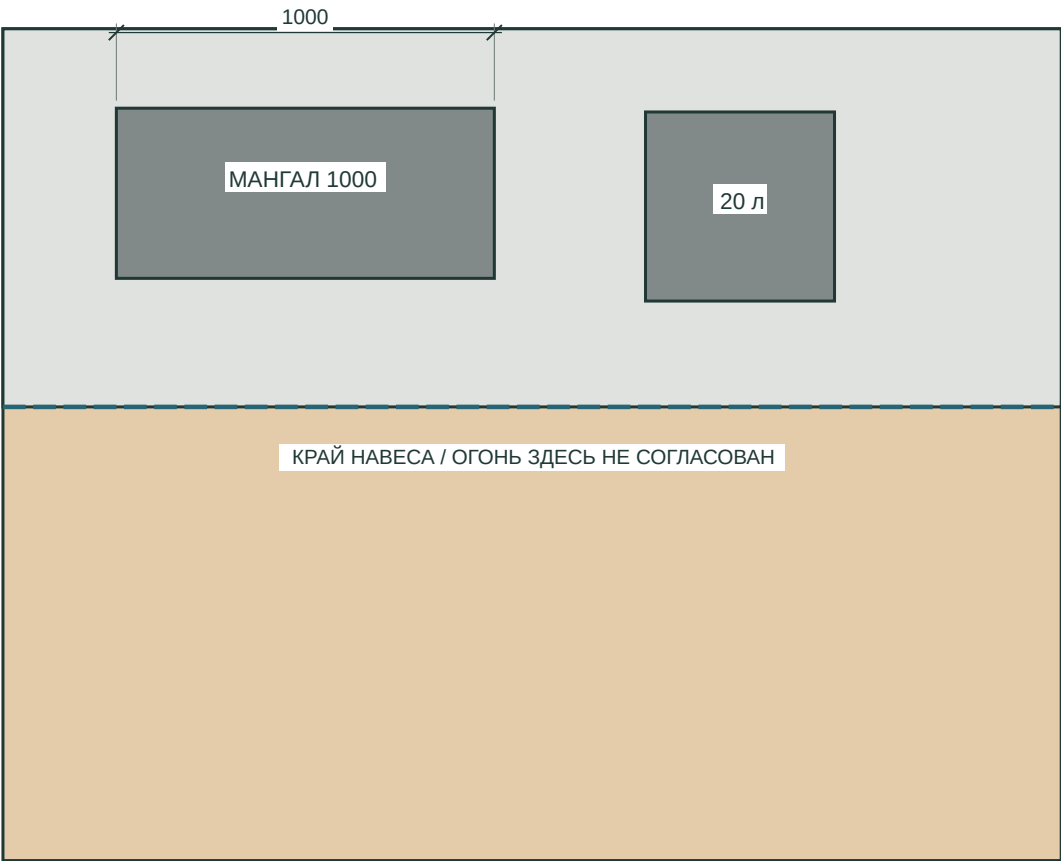

Пожарный стоп

Открытая полоска глубиной 1000 мм не доказывает нужного удаления от кромки крыши. После выбора приборов расположение может потребовать выноса дальше от террасы.

Основание

Серая вставка - только область поиска негорючей защиты. Толщина, теплопередача вниз, опоры и дистанции до дерева неизвестны. Плитка на досках не считается защитой.

Приборы


1000 мм мангала и 20 л казана заданы клиентом. Остальные размеры примерочные; паспорт и посадка казана нужны до закупки.

Дым

Южный ветер - наблюдение клиента. Завихрения вокруг навеса и попадание дыма в открытые створки не проверены. Визуал без пламени и топлива.


Палитра стен: один профиль, два цвета

Цвета на экране ориентировочные. Утверждать физические выкрасы на выбранной древесине.

 

ОТД-W01 / Молочный - основа

Гостиная и фронтоны, кухня, прихожая, спальни и глухая восточная стена лаунджа. Дерево у печи и в мокрых зонах исключено.

 

ОТД-W02 / Серо-оливковый - акцент

Вся доступная южная стена гостиной за ТВ и западная стена мастер-спальни за изголовьем. Светлые шкафы не перекрашивать.



C01 / Светлое дерево - потолок

Светлая потолочная вагонка P79 сохраняется. Балки немного натуральнее, без тёмно-коричневого контраста. Санузлы - белый натяжной потолок.


Укладка стен горизонтальная; малая фаска. Ориентир видимой ширины 180–200 мм, шаг рендера 200 мм. Шов и рельеф на картинке условные, не размер крепежа или усушки.

Смена цвета по углам целой стены. Без отдельного цветного треугольника фронтона, реечных вставок, микроцемента и дополнительного камня. Простые прямые наличники и плинтусы - намерение, не рабочий узел.

Выкрасы рядом с паркетом и вагонкой: дневной свет, вечер и выбранные светильники. Товарный код краски, порода, сорт, влажность и система нанесения ещё не выбраны.

Стены: молочная основа и две акцентные плоскости

Север сверху; озеро слева. Полосы показывают цвет существующей стены, не новую перегородку.

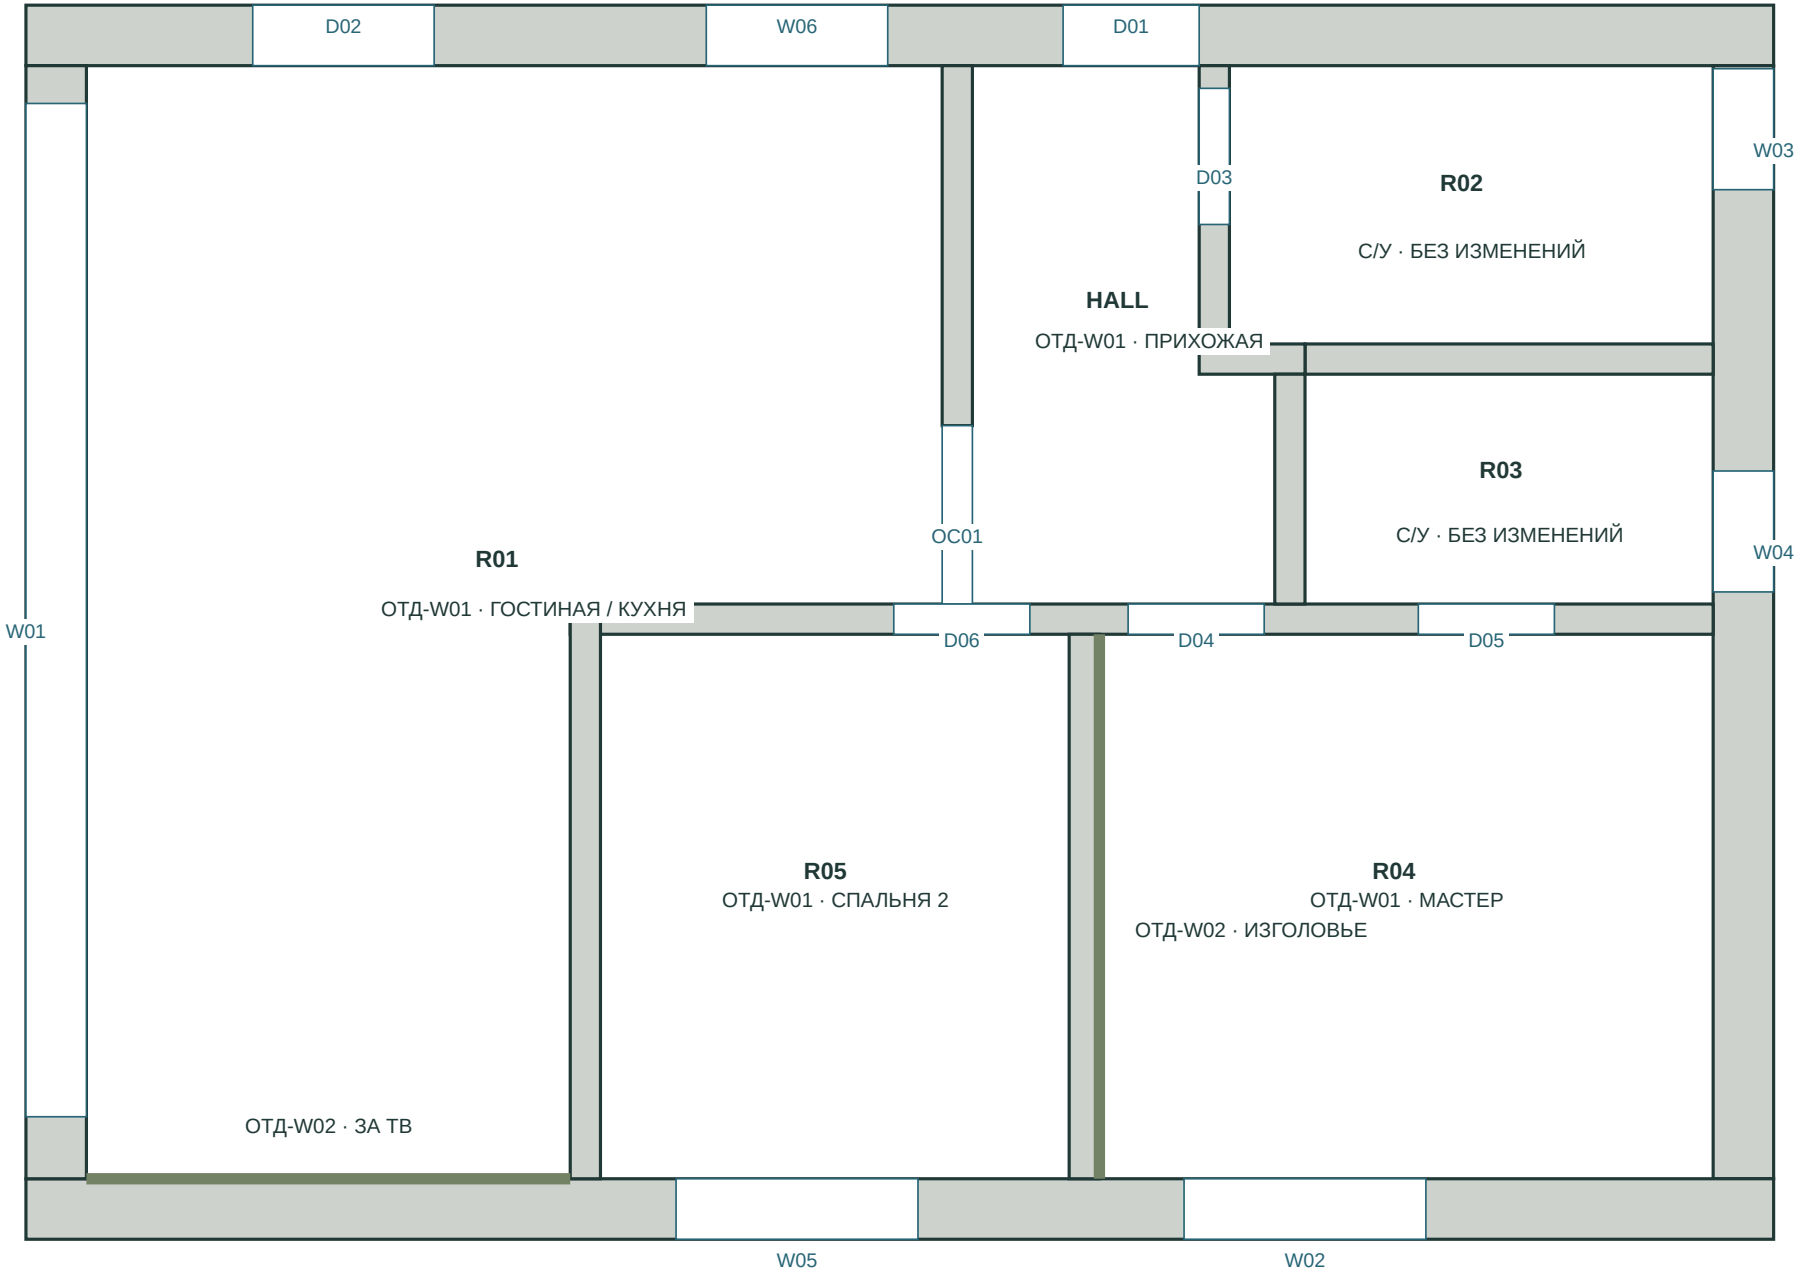

W01 / основа

Все сухие стены, кроме W02. На фронтонах до скатов продолжают тот же цвет и горизонтальный рисунок.

W02 / акценты

Южная стена гостиной X100–3300, Y7760. Западная стена мастер-спальни X6800, Y4160–7760. Только доступные поверхности, без мебели и проёмов.

Лаундж

Внутренняя сторона глухой восточной стены X8400. Стена дома у печи и её защитная зона остаются отдельной нерешённой системой.

Без дерева

Санузлы; кухонный рабочий фартук; защитные поверхности у печи. Их пригодность и состав требуют отдельных выбранных систем.

Отделка показана на существующей границе чистых поверхностей. Толщина доски и обрешётки не назначена; фактический монтажный резерв в стенах не подтверждён. Перепроверить до раскроя и заказа дверей.

Обшивка: простая сборка и обязательные проверки

Координационная примерка. Не инструкция для монтажа.

Один набор деталей

Один профиль по сухим помещениям; прямые наличники и плинтусы. Профиль углов, стыков, откосов и сопряжения со скатом выбрать на одном макете, затем повторять.

Не потерять размеры

Визуальная поверхность совпадает с исходной чистовой границей. Фактические доска + обрешётка + необходимые слои пока не помещены в стеновой резерв. Не уменьшать комнаты и не передвигать мебель без согласованного изменения модели.

Слои перегородок

Имитация бруса - декоративная облицовка, не замена согласуемому акустическому и противопожарному составу. Не убирать листовые слои, герметизацию и развязку ради сохранения номинальных 200 мм.

Электрика и обслуживание

Лицевую плоскость розеток, выключателей, решёток и люков привязать к реальной отделке. Сохранить доступ к соединениям и драйверам. Дерево и скрытая проводка требуют согласования электриком, крепёж - по основанию.

Влажность, кухня и печь


В санузлах и рабочем фартуке дерево не назначено. В лаундже покрытие и материал выбираются под периодическое отопление. Печь, дымоход и их защитные зоны - отдельное техническое решение; никаких новых разрешённых отступов здесь нет.

До закупки

Утвердить образцы, производителя, породу/сорт, рабочую ширину, длины, толщину, влажность, покрытие и узлы. Затем развертки с раскроем, вычетами и запасом. По графическому шагу 200 мм закупку не считать.

Диван: высоты и логика отделки стен

Габариты мебели — проектное предложение, не выбранная модель. Развёртка дивана: взгляд с юга на север.

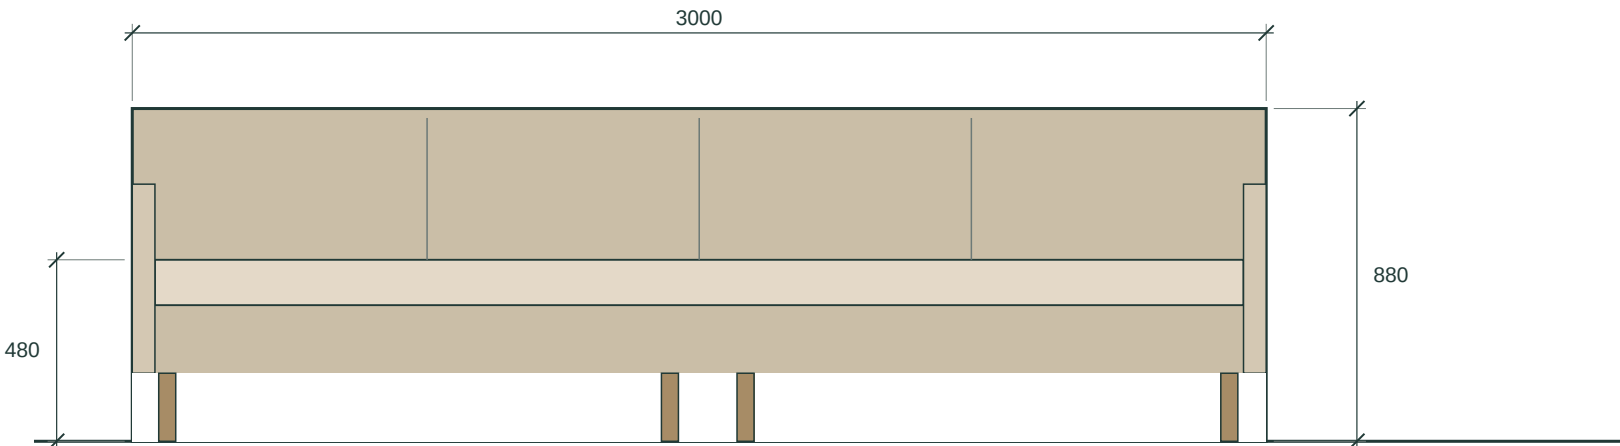

2 модуля по 1500 · 4 места по 720 между подлокотниками

Глубина корпуса 650; подушка сиденья 500. Подушка спинки выступает над ней на 40: на её уровне остаётся 460. Низкая спинка 880. Модули для уборки отодвигаются; массу и проход доставки проверить при выборе.

В модели: сиденье 480, верх стола 770, разность 290. Между передней гранью дивана и столешницей в плане 50. Это не доказанная эргономика: нужны реальные подушки, опоры и пространство для коленей.

Стены: что показываем

Широкая горизонтальная имитация бруса. Графический шаг 200. Молочная основа; серо-оливковая стена ТВ и стена за изголовьем мастер-спальни.

Что стало заметнее

Фаска, тень горизонтального стыка и продольный рисунок древесины. Цвета P80 сохранены; потолочная вагонка — другой, более узкий рисунок.

Исключения

Фартук кухни остаётся гладким. Санузлы, фасад и непроверенная теплозащита у печи не покрываются новым материалом автоматически.


Для образца

Профиль, порода, толщина, покрытие и точный цвет ещё не выбраны. Фактура процедурная: не каталог изделия и не узел крепления. Утвердить физический образец при вашем свете.

Отделка показана материалом на сохранённых гранях модели. Толщина доски/обрешётки, акустическое основание и чистые размеры после выбора системы требуют отдельной координации.

Крыша: размерная основа раскладки фальца

Размеры новой геометрии. Номинальные контрольные грани; не монтажный чертёж.

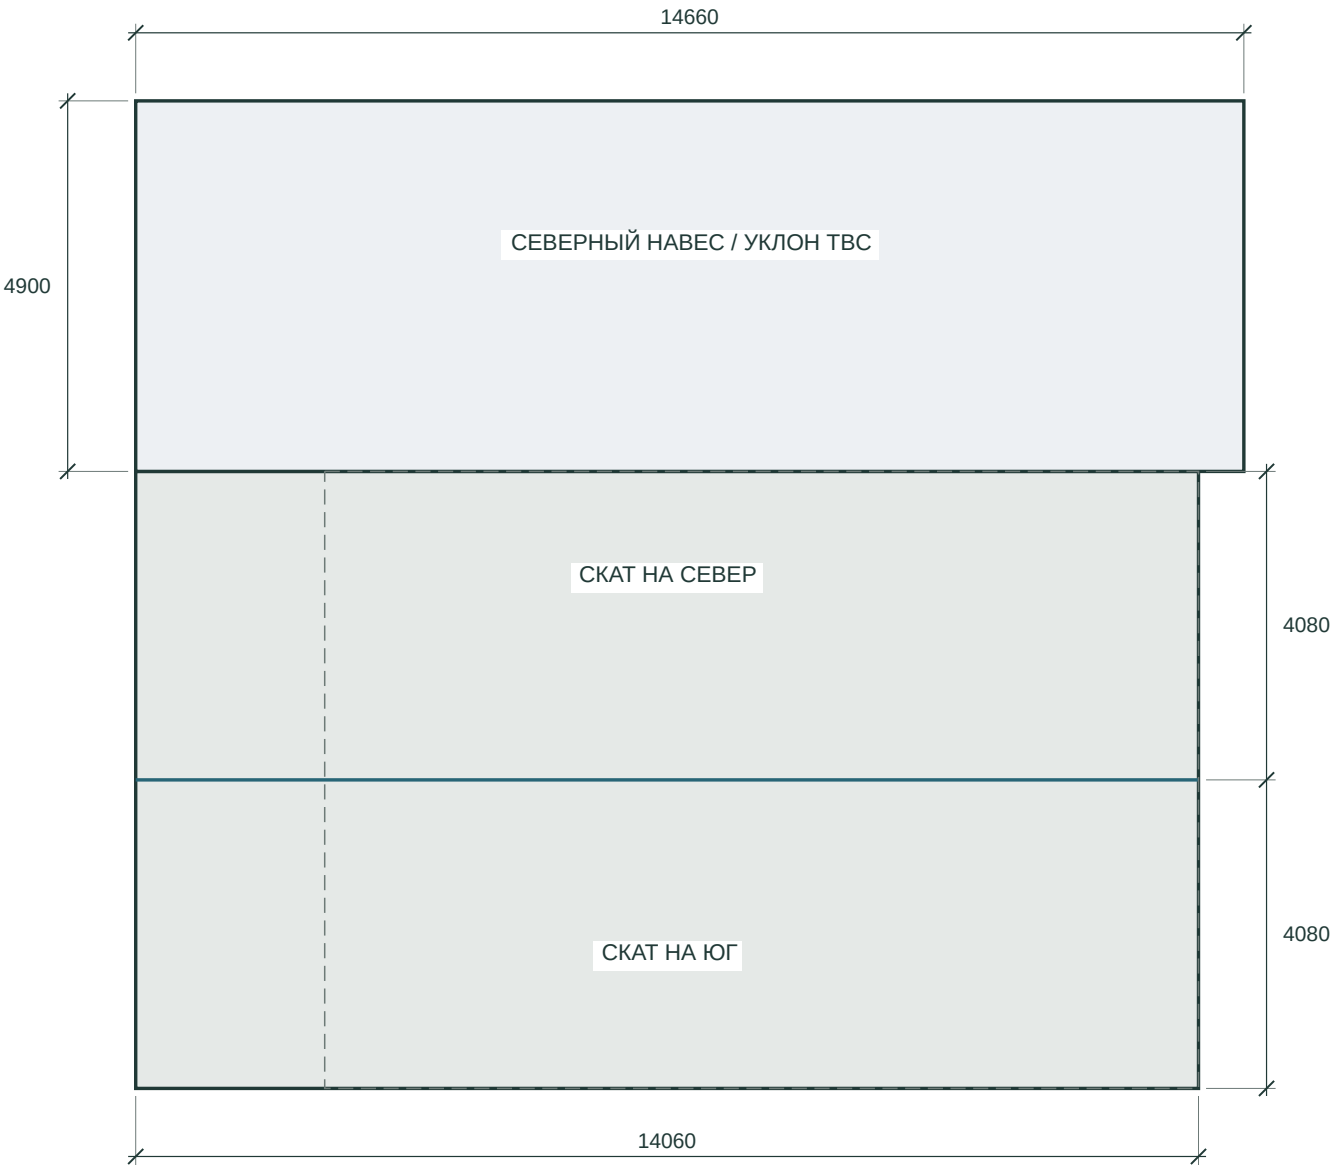

Поверхности

Два ската основной крыши: по 62,1452 м² в графической модели.
Длина каждого ската 4420 мм при подъёме 1700. Проходки и раскрой отдельно.

Кромки


Конёк 14060; две нижние кромки по 14060; четыре торца по 4420. Это длины границ, не готовая спецификация доборов.

Навес

Односкатное намерение, но фактические уклон и водосток не определены. Проекция 71,834 м² — не заказная площадь.

Каркас и проходки


Нет назначения опор, сечений, снегозадержателей, вырезов или крепежа. Дымоход координируется отдельным листом М107.

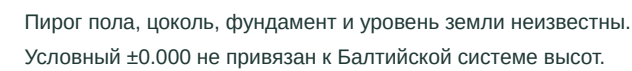

M 1:50 / MM / A3

Северный фасад

Взгляд с севера на юг: ВОСТОК слева; ЗАПАД справа.

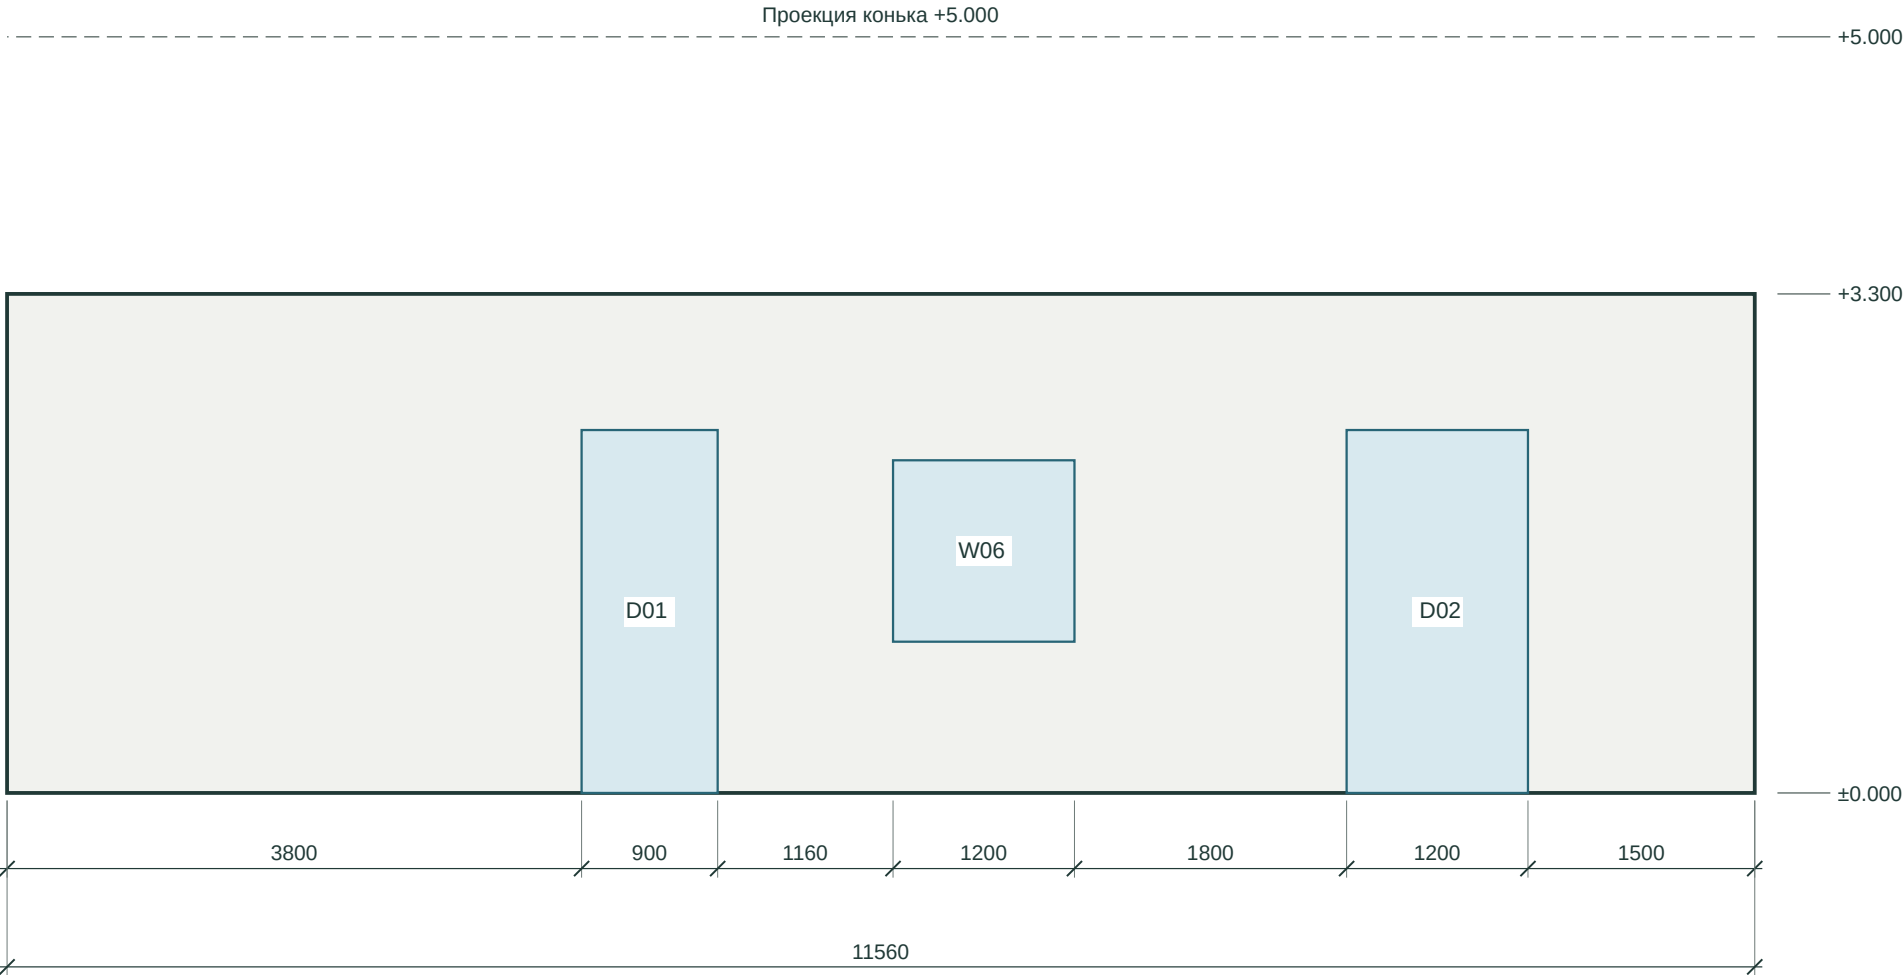

Оболочка дома

Показан основной дом без перекрывающего его лаунджа/навеса, чтобы видеть все проёмы. Общий облик — в 3D и плане оболочки.

Уровни — графические

Низ/верх проёмов и 3300/5000 сохранены из модели. Абсолютная посадка на участок и монтажные отметки неизвестны.

Отделка

Фальцевая кровля; часть фасадов — окрашенная ЦСП с вентиляционным зазором. Границы ЦСП, другая отделка, раскладка и цвет не выбраны.


До производства

Требуются перемычки, простенки, монтажные зазоры, опоры W01, стеклопакеты, открывание и допуски. Эти листы не заказ окон.

Высотные и площадные обмеры этой оболочки — сценарий графической модели, не спецификация изделий. Северный фасад специально развёрнут как реальный вид снаружи: D01 расположен левее D02.

Южный фасад

Взгляд с юга на север: ЗАПАД слева; ВОСТОК справа.

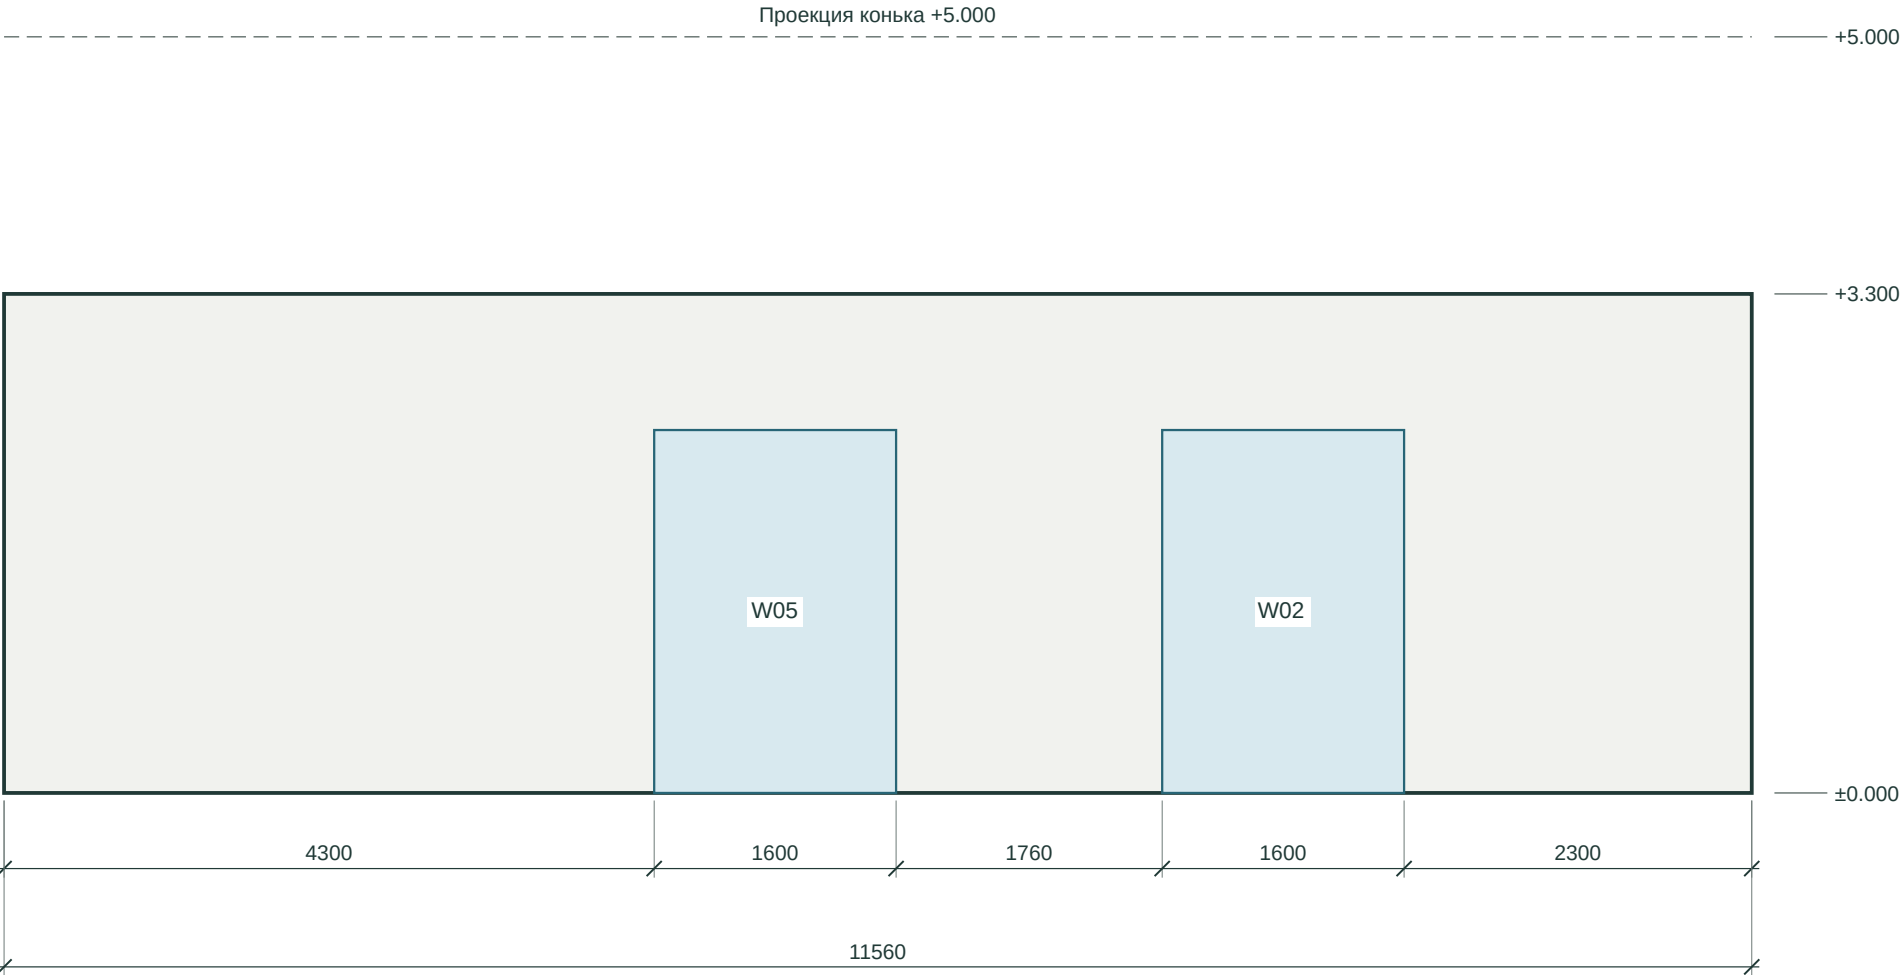

Оболочка дома

Показан основной дом без перекрывающего его лаунджа/навеса, чтобы видеть все проёмы. Общий облик — в 3D и плане оболочки.

Уровни — графические

Низ/верх проёмов и 3300/5000 сохранены из модели. Абсолютная посадка на участок и монтажные отметки неизвестны.

Отделка

Фальцевая кровля; часть фасадов — окрашенная ЦСП с вентиляционным зазором. Границы ЦСП, другая отделка, раскладка и цвет не выбраны.


До производства

Требуются перемычки, простенки, монтажные зазоры, опоры W01, стеклопакеты, открывание и допуски. Эти листы не заказ окон.

Высотные и площадные обмеры этой оболочки — сценарий графической модели, не спецификация изделий. Северный фасад специально развёрнут как реальный вид снаружи: D01 расположен левее D02.

Западный фасад · озеро

Взгляд с запада на восток: СЕВЕР слева; ЮГ справа.

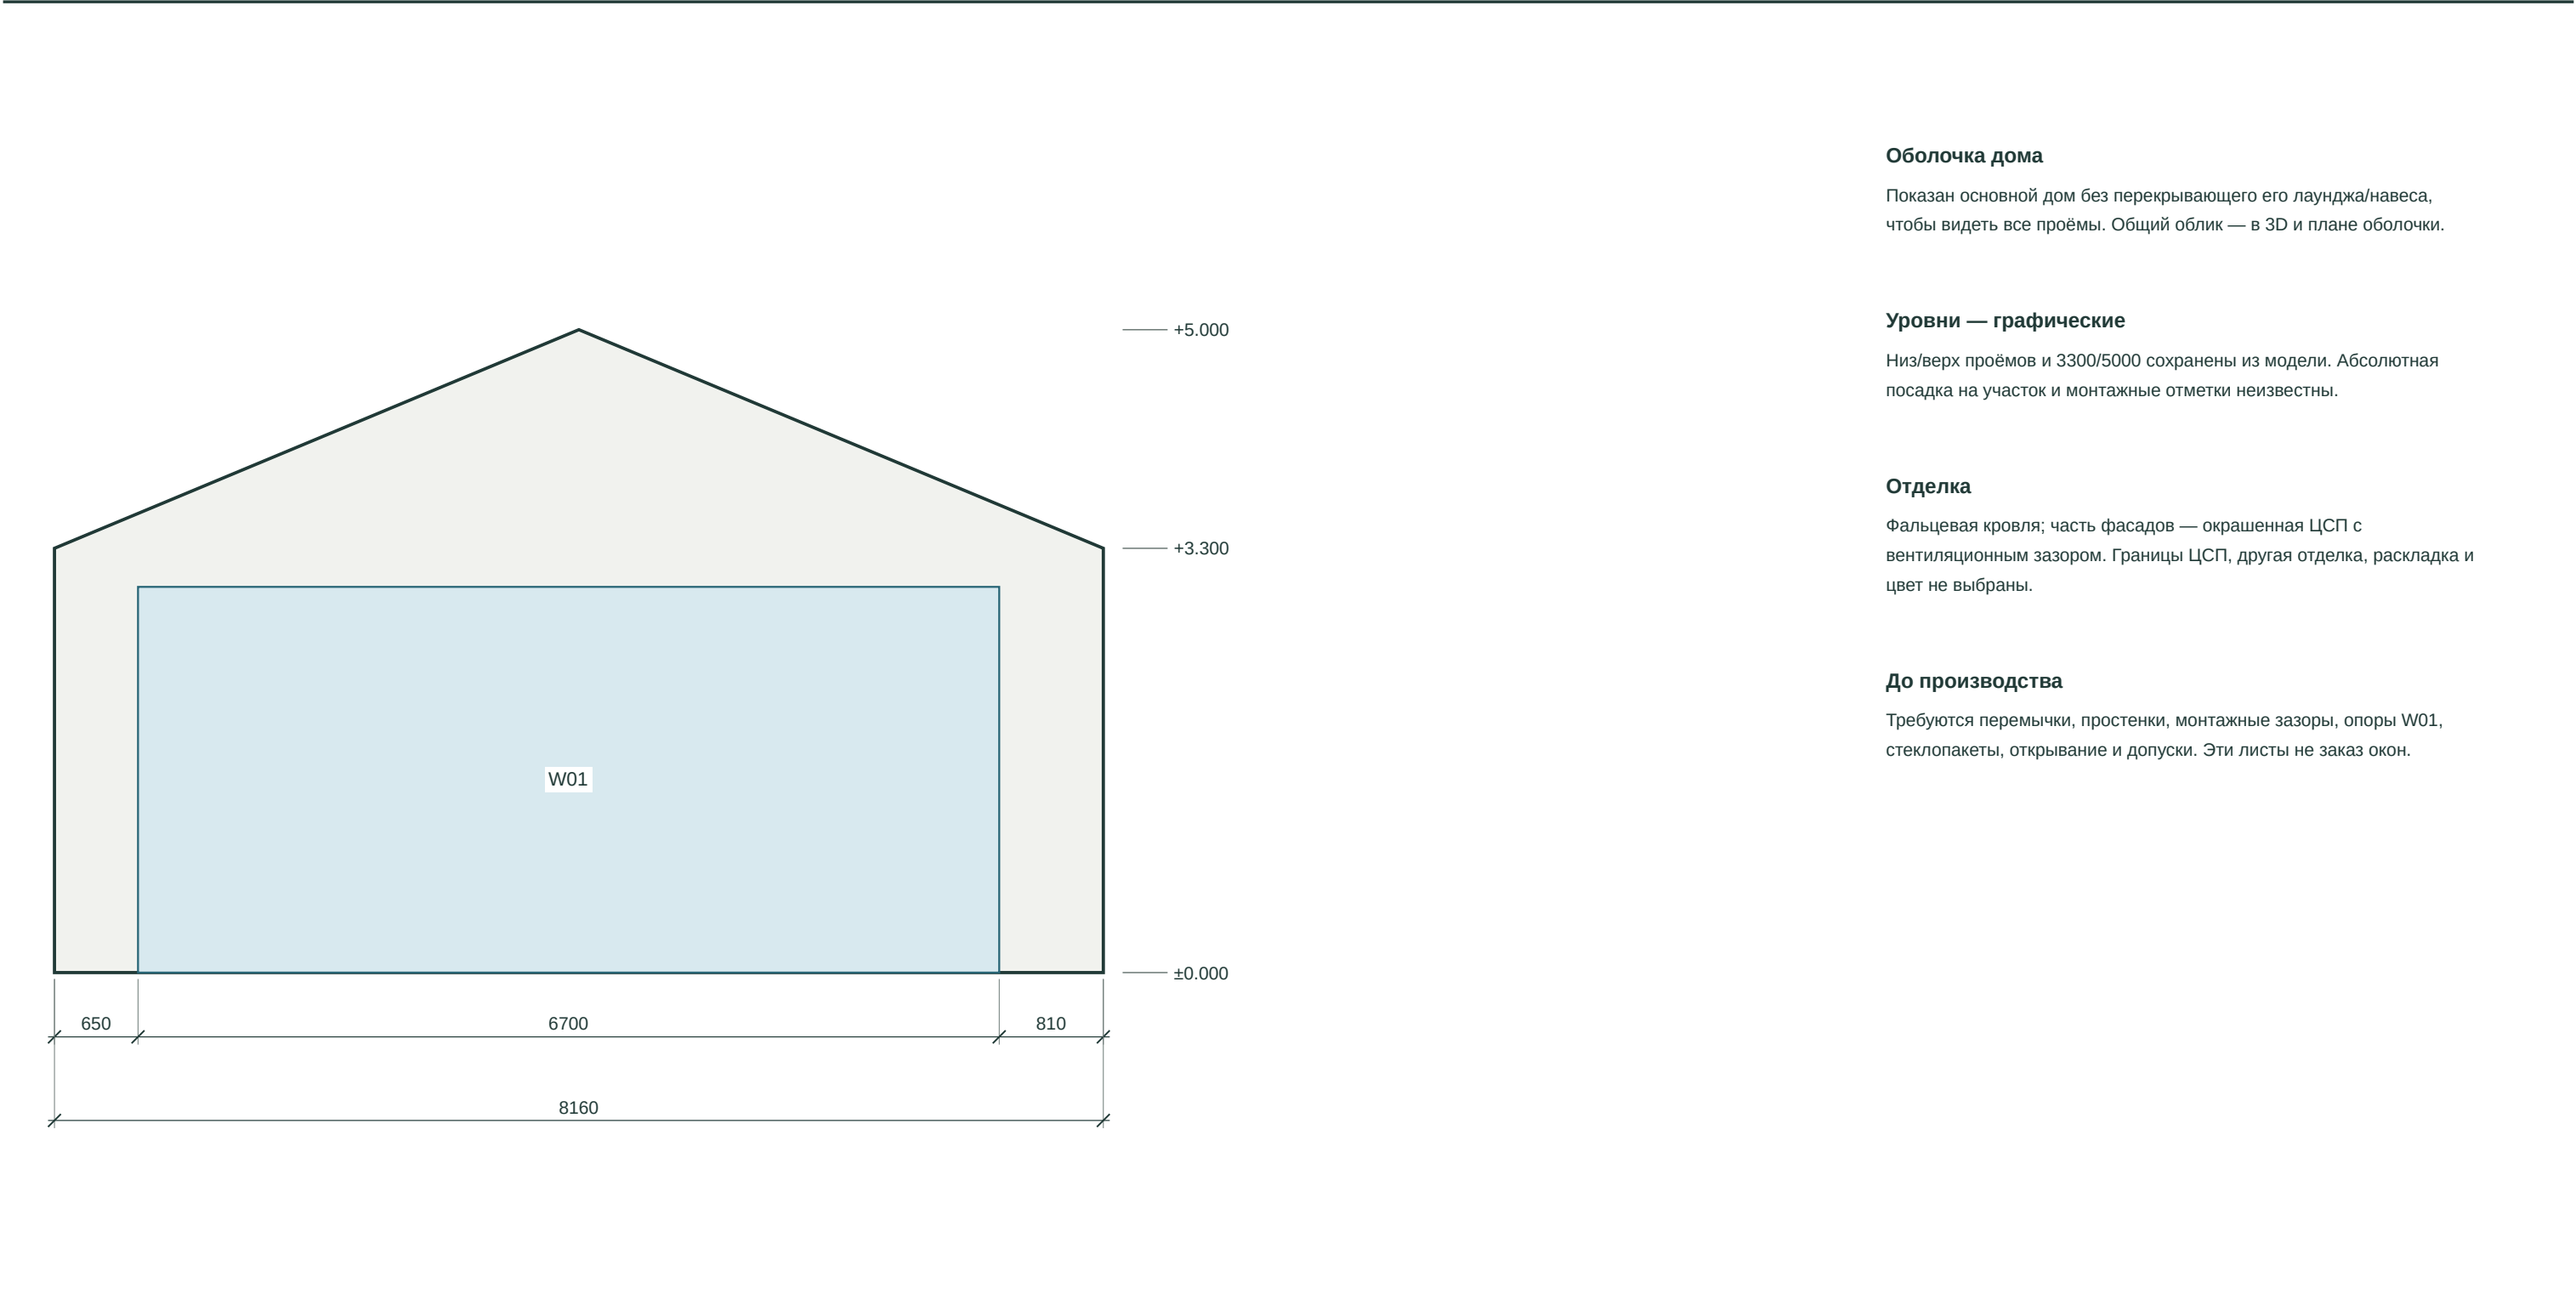

Оболочка дома

Показан основной дом без перекрывающего его лаунджа/навеса, чтобы видеть все проёмы. Общий облик — в 3D и плане оболочки.

Уровни — графические

Низ/верх проёмов и 3300/5000 сохранены из модели. Абсолютная посадка на участок и монтажные отметки неизвестны.

Отделка

Фальцевая кровля; часть фасадов — окрашенная ЦСП с вентиляционным зазором. Границы ЦСП, другая отделка, раскладка и цвет не выбраны.


До производства

Требуются перемычки, простенки, монтажные зазоры, опоры W01, стеклопакеты, открывание и допуски. Эти листы не заказ окон.

Высотные и площадные обмеры этой оболочки — сценарий графической модели, не спецификация изделий. Северный фасад специально развёрнут как реальный вид снаружи: D01 расположен левее D02.

Восточный фасад

Взгляд с востока на запад: ЮГ слева; СЕВЕР справа.

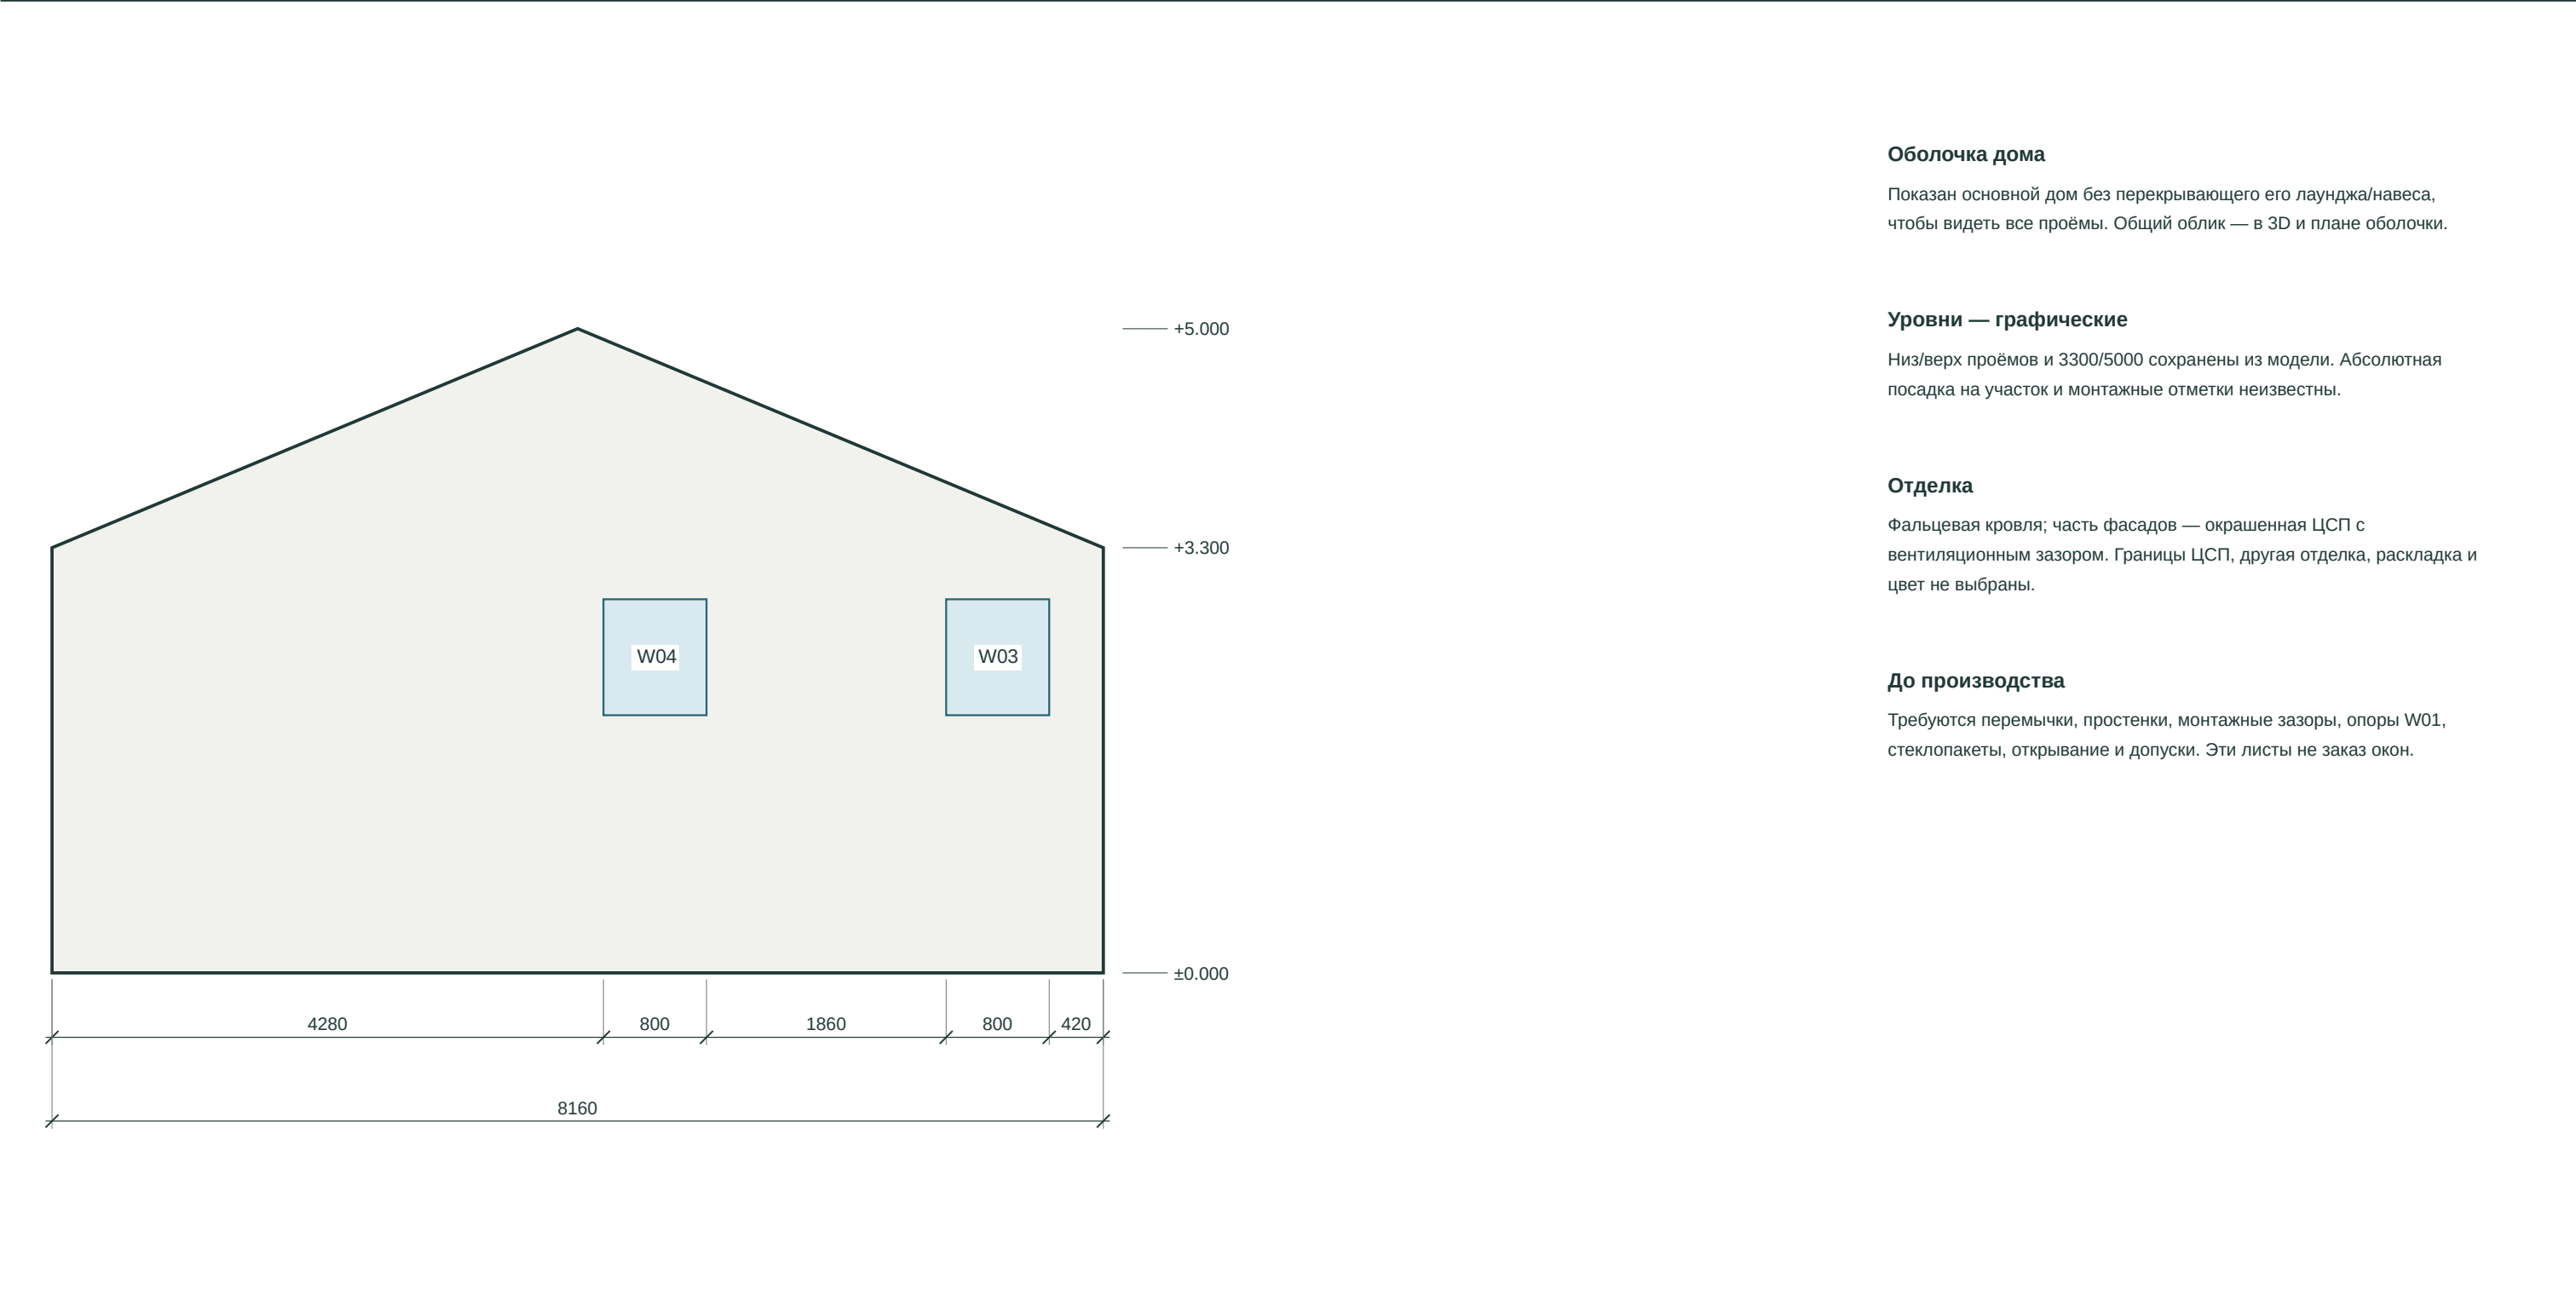

Оболочка дома

Показан основной дом без перекрывающего его лаунджа/навеса, чтобы видеть все проёмы. Общий облик — в 3D и плане оболочки.

Уровни — графические

Низ/верх проёмов и 3300/5000 сохранены из модели. Абсолютная посадка на участок и монтажные отметки неизвестны.

Отделка

Фальцевая кровля; часть фасадов — окрашенная ЦСП с вентиляционным зазором. Границы ЦСП, другая отделка, раскладка и цвет не выбраны.

До производства

Требуются перемычки, простенки, монтажные зазоры, опоры W01, стеклопакеты, открывание и допуски. Эти листы не заказ окон.

Высотные и площадные обмеры этой оболочки — сценарий графической модели, не спецификация изделий. Северный фасад специально развёрнут как реальный вид снаружи: D01 расположен левее D02.

Фундамент: геометрические исходные данные

Контуры назначения, НЕ план фундаментных элементов. Геология не привязана к текущему пятну.



Исходный контур

Дом 11560 × 8160. Периметр 39,44 м. Это контур наружных граней стен, не край плиты, оси свай или разбивочные оси.

Разные основания


Дом, периодически тёплый лаундж, открытые террасы, навес и тяжёлая печь имеют разные нагрузки и температурные режимы. Совместность/разделение решает конструктор.

Нужны реакции

Стены и опоры крыши, W01, навес, печь/дымоход, бак с водой, эксплуатационные и климатические воздействия. Сечения и сетка опор не назначены.

Стоп до расчёта

Тип, глубина, сваи, толщина плиты, армирование и земляные работы остаются ТВС. Запас материала не заменяет расчёт осадок и прочности.

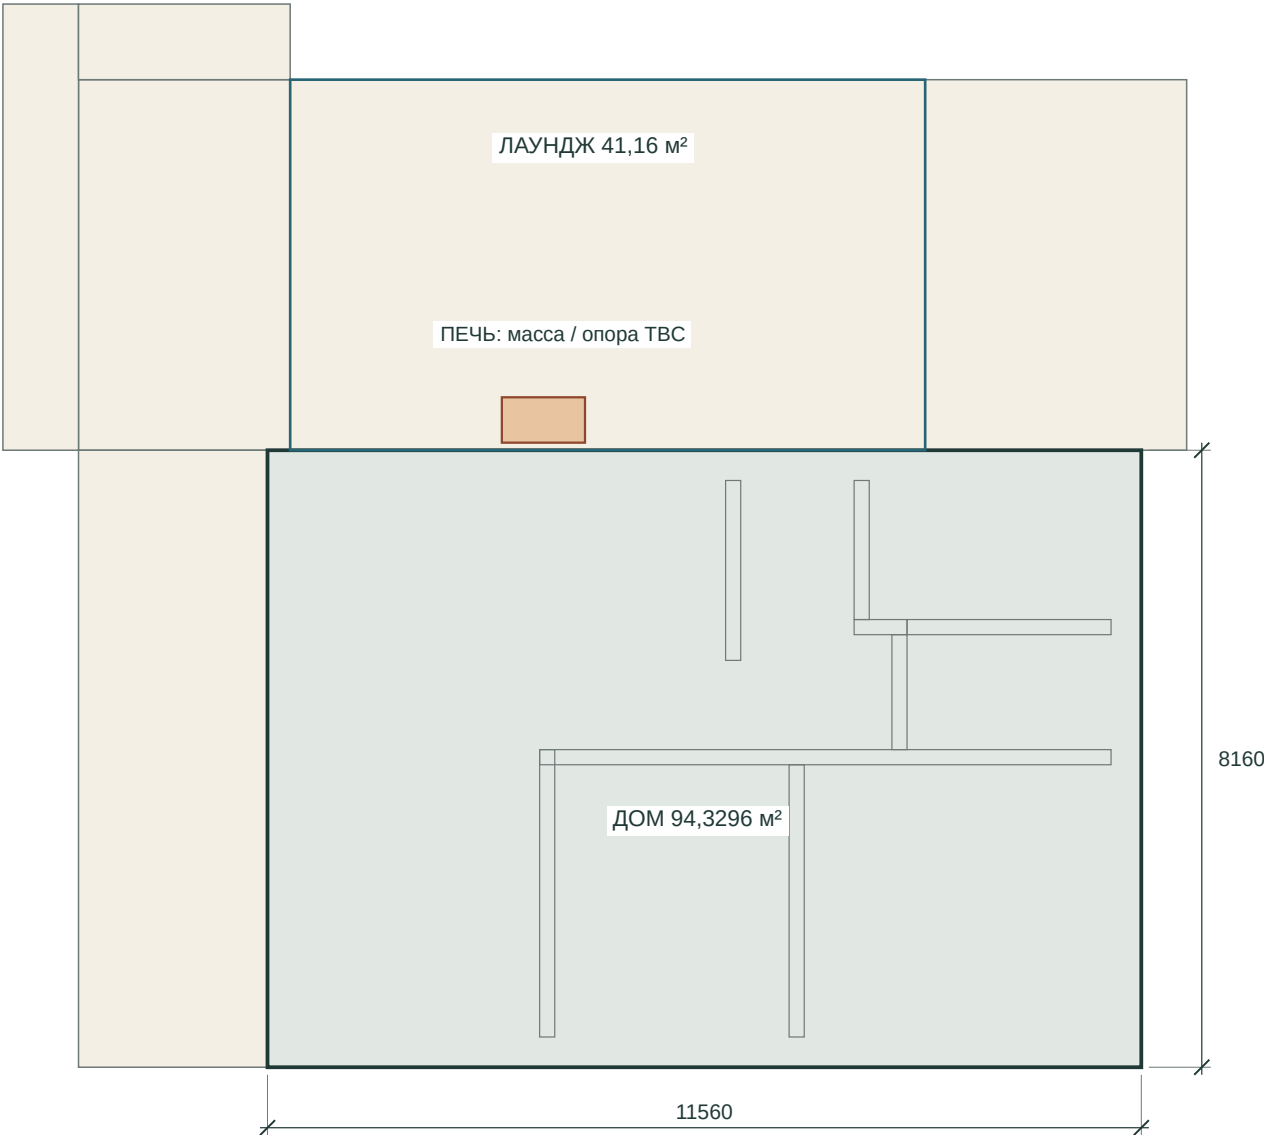

Геология и геодезия: что действительно имеется

Задание для предложения подрядчика. Не разрешение на изготовление или строительство.

Получено, но не принято для расчёта

В архиве есть А3 топоплан 1:500 для Исаи 7/8: СК1963, зона 2; Балтийская система высот, штамп 10.25. Есть 14 фотографий отчёта 55-04-24-ИГ, апрель 2024: скважины 1—4 до 5 м, схема и разрез, физические/химические таблицы и выводы.

Критическая недостающая связь

Скважины показаны в прямоугольнике 10,5 × 13,5 м без доказанной координатной связи с нынешним контуром 11,56 × 8,16 м и всеми опорами навеса/печи. Условный ноль геологии не равен автоматически нулю проекта или отметкам топоплана. Наложение «на глаз» не выполнялось.

Факты отчёта, не принятые расчётные параметры

Насыпной неоднородный грунт до 1,3—1,8 м не рекомендован как естественное основание. Вода вскрыта на 2,3—3,5 м; описаны напор, верховодка и затруднённый сток. Расчёт должен учитывать сезонность, пучение и возможную разность деформаций.

Что передать геотехнику

Полный подписанный отчёт и приложения; исходный топоплан/DWG/DXF и его актуальность; точный контур Р76 с посадкой в одной системе координат; отметки чистого пола/земли; реакции конструкций. Нужна письменная оценка покрытия изысканий нынешним домом.

Почему нет готового армирования

Табличное R0 отчёта нельзя подставить вместо расчётной несущей способности или получить фундамент делением общей массы на это число. Не проверены осадки, пучение, местные опоры, водоотвод, прочность и предельные состояния. Расчёт фундамента остаётся открытым заданием.

Задание конструктору по основанию и каркасу

Задание для предложения подрядчика. Не разрешение на изготовление или строительство.

Расчётная цепочка

Согласованные материалы и узлы → собственный вес и эксплуатационные/климатические нагрузки → каркас/крыша/связи → реакции по каждой опоре и сочетанию → геотехнические и железобетонные проверки → спецификация и рабочие узлы. Числа нагрузок и коэффициенты здесь не назначены.

Сравнить фундаментные решения

Запросить обоснованное сравнение плиты на подготовленном основании, ленточного и свайного решения, где они применимы к принятому грунтовому профилю. Для каждого: земляные работы, несущий слой, вода/пучение, общие и разностные осадки, конструкция пола, сроки, проверяемость и стоимость. Вариант не выбран.

Отдельные сосредоточенные нагрузки

Кирпичная печь/дымоход; бак 250 л с массой корпуса/воды и закладными; опоры W01 шириной 6700; западный вынос крыши 2500; северный навес 14660 × 4900; открываемое остекление лаунджа. Массы, реакции, анкеры и опоры должен задать расчёт.

Обязательный результат КР

Разбивка осей и отметки; схемы фундамента и армирования; все сечения/узлы; спецификации бетона, стали и древесины; несущие стены/балки/перемычки; пути боковых усилий и отрыва; соединения, допуски, временные связи и порядок монтажа; подпись ответственного конструктора.

Геометрия для расчётчика

Дом A=94,3296 м², наружный периметр 39,44 м. Для ещё не выбранной плиты только формула V=A×t: на каждые 10 мм равномерной толщины приходится 0,943296 м³. Это чувствительность геометрии, НЕ рекомендация толщины; рёбра, подошвы и отверстия отдельно.

Стены, утепление и фасады: задание заводу

Задание для предложения подрядчика. Не разрешение на изготовление или строительство.

Наружная стена / 400 мм

400 мм — резерв полного узла, не размер стойки и не толщина утеплителя. Предложить послойный состав от помещения наружу: отделка/сервисная зона, воздушный и парорегулирующий слой, несущая часть, утепление, конструкционная и ветроводозащитная функции, вентзазор, фасад. Толщины и материалы согласовать до выпуска каркаса.

Перегородка / 200 мм

Сохранено намерение Р69: 25 + 150 + 25 = 200 мм сухого номинала. Это не доказанная звукоизоляция. Предложить испытанный узел с эковатой либо обоснованную альтернативу; плотность заполнения, крепление, развязку облицовок и примыкания подтвердить. Мокрые слои и инсталляции не должны незаметно съесть размеры.

ЦСП только на части фасада

Клиентское намерение: окрашенная ЦСП в вентфасаде. Подрядчик предлагает карту зон, толщину/формат листов, раскладку, швы, крепёж, подконструкцию, грунт/краску и обработку кромок. До выбора карты площадь ЦСП не равна площади всех непрозрачных фасадов.

Смета слоями

Каждый слой отдельной строкой: площадь нетто, вычеты, возвраты/откосы, число слоёв, листовой раскрой, нахлёсты, отходы и упаковки. Для эковаты: фактический объём полостей за вычетом дерева × подтверждённая плотность монтажа; не площадь стены × 200 мм.

Контроль до зашивки

Проверить древесину, узлы и закладные; непрерывность воздушного/влаго-/теплового контуров; углы/проёмы/проходки; заполнение утеплителем; фотофиксацию. Критерии испытаний и приёмки назначает проектировщик, не эта ведомость.

Фальцевая крыша, навес и водоотвод

Задание для предложения подрядчика. Не разрешение на изготовление или строительство.

Обмер основной крыши

В графической модели два ската: $2 \times 14,06 \times 4,42 = 124,2904 \text{ м}^2$. Проекция 114,7296 м² не является площадью фальца. Геометрический конёк 14,06 м; две нижние кромки 28,12 м; четыре наклонных торца 17,68 м. Это обмер без раскроя и доборных элементов.

Что требуется для заказа фальца

Выбрать металл/толщину/покрытие, тип фальца, рабочую ширину картины, предельные длины/подвижность, кляммеры, основание/разделительный слой, вентиляцию. Выпустить раскладку картин и все примыкания/карниз/конёк/торцы/проходки. Профиль и ограничения брать по конкретной системе производителя.

Теплоизоляция — один согласованный принцип

P78: над западной гостиной и столовой — тёплые скаты; над кухней, коридором и остальными комнатами — плоский потолок 3 м. Нужны непрерывные тепло-, воздушный и парорегулирующий слои в переходе. Не утеплять дважды одну зону; графические 350 мм не толщина утеплителя.

Северный односкатный навес

Проекция 71,834 м². Уклон и фактическая поверхность пока ТВС; линия +3.100 не готовая крыша. Требуются опоры/связи, примыкание к дому, снеговой мешок/сход снега, водоотвод и безопасный аварийный перелив. Скрытый водосток — не выбранная спецификация.

Печь и открытый огонь

Ось дымохода в плане [3350; −400], до линии конька 4480 мм. Диаметр, отметка устья, опоры, разделки и проходки требуют отдельного расчёта и выбранного дымохода. Мангал/казан вне кровли не получают разрешение на деревянном настиле по картинке.

Как подрядчик должен вернуть смету под ключ

Задание для предложения подрядчика. Не разрешение на изготовление или строительство.

Единая форма предложения

Для каждой позиции: ID/зона, точное изделие или материал, единица, чистое количество, нахлёсты/отходы/запас отдельно, количество к закупке и упаковки, цена материала, работа, доставка/разгрузка, сумма, валюта, дата/срок действия, налоги. Приложить основание количества — лист или спецификацию.

Разделить пакеты

Подготовка участка и временные работы; фундамент/земля/дренаж; каркас/соединения; полы; крыша/фальц/водосток; утепление и мембраны; окна/двери; фасады; перегородки и отделка; лаундж/террасы/печь; инженерия; доставка/монтаж/пусконаладка; проектирование и исполнительные документы.

Неизвестные позиции не прятать

Если изделие или конструкция не выбраны — стоимость отдельным предварительным допущением с его границами. «Включено» должно иметь состав. Не выводить точный итог «под ключ» без согласованного объёма, даты цен и исключений. В нашей ведомости цены намеренно пустые.

Резерв с объяснением

Резерв привязать к риску: грунт, раскрой, замена изделий, доставка, неизвестный узел. Производственный отход не равен запасу прочности. Процент не назначен: подрядчик раскрывает и обосновывает отдельно по материалам.

Что запросить от завода

3D/IFC или согласованный обменный формат, КД панелей/стен с ID, марки деталей, ведомость древесины по сечениям и длинам, крепёж, чертежи соединений и закладных, раскрой листов, упаковочные листы, инструкция/очерёдность сборки, QA и ответственность за расчёт.

Реестр обязательных уточнений перед производством

Задание для предложения подрядчика. Не разрешение на изготовление или строительство.

Участок и основание — конструктор / геотехник

Подписанный полный отчёт; актуальность топо и границ; привязка пятна и скважин; отметки/сток/вода; действующие расчётные нормы; грунтовая модель, нагрузки и реакции. Без них производство фундамента не выпускать.

Архитектура — архитектор / заказчик

Принять наружные составы в резерве 400 мм и внутренние в 200 мм; чистые размеры после мокрых слоёв; монтажные проёмы и открывание; пороги двух входов в лаундж; узкие простенки D01/W03/W04/D04; карта ЦСП/прочей отделки и цвета.

Каркас/кровля — завод / конструктор

Несущая схема, класс и влажность древесины, сечения/шаг, диафрагмы, опоры выносов, узлы и крепёж; раскрой фальца; противопожарные примыкания; теплотехника/влажорежим; допуски крупного остекления.

Инженерия — проектировщики систем

Ввод и выделенная мощность, фазы/заземление, группы и защиты, трассы/высоты; вода/канализация/зимняя мойка; вентиляция/вытяжка; отопление дома и отдельного лаунджа; точные изделия T1/робот/инсталляции, сервис и закладные.

Приёмка и выпуск

После согласования — независимая проверка расчётов и междисциплинарных конфликтов, спецификации с ревизией, перечень скрытых работ, испытания, исполнительные планы и передача паспортов. P78 имеет только статус для согласования/расчёта предложения.

Материалы, которые пока нельзя посчитать честно

Задание для предложения подрядчика. Не разрешение на изготовление или строительство.

Фундамент

Нет количеств бетона, арматуры, свай, земляных работ и подготовки: тип/отметки/несущий слой/реакции не выбраны. Для расчёта передан контур, разные режимы зон и реестр имеющихся изысканий.

Каркас и ограждения

Нет кубатуры древесины, числа стоек, перемычек, крепежа и обшивок: нужен расчётный каркас с соединениями. Обмер поверхностей не определяет раскрой. Утепление требует фактических слоёв и полостей, а не полного резерва стены.

Фасад и кровля

Обмер непрозрачных плоскостей дан, но карта ЦСП и прочих материалов не выбрана. Фальц требует рабочей ширины/замков/раскладки. Навес не имеет принятого уклона. Доборы и водосток рассчитываются по узлам.

Остекление и печь

Площади номинальных проёмов не равны площади стеклопакетов/блоков. Большая доля открывания лаунджа требует конкретной системы. Для печи нужны порядовка/масса, шамотный узел, температурные швы и дымоход; число кирпичей из внешнего габарита не выводится.

Инженерия и смета

Точки на схеме не определяют длину кабеля или трубы. Нужны трассы, узлы, изделия и расчёты. Для незавершённых позиций в CSV стоит пустое количество и BLOCKING_TBC; подрядчик заполняет их после принятия решения, не подменяет нулём.

Обмер модели для сметы · 1

Размеры новой геометрии. Номинальные контрольные грани; не монтажный чертёж.

ID количества	Объект / объём работ	Количество	Ед.	Основание / исключения
HOUSE-GROSS	Контур дома по наружным граням	94.33	m2	План / номинал
HOUSE-PERIMETER	Наружный периметр стен	39.44	m	План / номинал
HOUSE-INNER	Контрольная площадь внутри наружных стен	79.19	m2	План / номинал
FLOOR-R01	Пол / проекция потолка R01	32.31	m2	План / номинал
WALLFACE-R01	Стены до H3000, зона R01	49.49	m2	Графическая высота*
FLOOR-HALL	Пол / проекция потолка HALL	6.1	m2	План / номинал
WALLFACE-HALL	Стены до H3000, зона HALL	23.08	m2	Графическая высота*
FLOOR-R02	Пол / проекция потолка R02	5.89	m2	План / номинал
WALLFACE-R02	Стены до H3000, зона R02	27.63	m2	Графическая высота*
FLOOR-R03	Пол / проекция потолка R03	4.1	m2	План / номинал
WALLFACE-R03	Стены до H3000, зона R03	22.71	m2	Графическая высота*

* Не заказные количества. Формулы, источники, вычеты и ограничения — в CSV/JSON. Отходы, нахлёсты и запас не включены; неизвестное не равно нулю. Не складывать брутто, нетто и их подмножества.

Обмер модели для сметы · 2

Размеры новой геометрии. Номинальные контрольные грани; не монтажный чертёж.

ID количества	Объект / объём работ	Количество	Ед.	Основание / исключения
FLOOR-R04	Пол / проекция потолка R04	14.62	m2	План / номинал
WALLFACE-R04	Стены до Н3000, зона R04	38.34	m2	Графическая высота*
FLOOR-R05	Пол / проекция потолка R05	11.16	m2	План / номинал
WALLFACE-R05	Стены до Н3000, зона R05	34.47	m2	Графическая высота*
FACADE-NORTH	Непрозрачная площадь фасада north	31.67	m2	Графическая высота*
FACADE-SOUTH	Непрозрачная площадь фасада south	30.47	m2	Графическая высота*
FACADE-WEST	Непрозрачная площадь фасада west	13.76	m2	Графическая высота*
FACADE-EAST	Непрозрачная площадь фасада east	32.42	m2	Графическая высота*
OPEN-D02	Номинальная площадь проёма D02	2.88	m2	Графическая высота*
OPEN-W06	Номинальная площадь проёма W06	1.44	m2	Графическая высота*
OPEN-D01	Номинальная площадь проёма D01	2.16	m2	Графическая высота*

* Не заказные количества. Формулы, источники, вычеты и ограничения — в CSV/JSON. Отходы, нахлёсты и запас не включены; неизвестное не равно нулю. Не складывать брутто, нетто и их подмножества.

Обмер модели для сметы · 3

Размеры новой геометрии. Номинальные контрольные грани; не монтажный чертёж.

ID количества	Объект / объём работ	Количество	Ед.	Основание / исключения
OPEN-W03	Номинальная площадь проёма W03	0.72	m2	Графическая высота*
OPEN-W04	Номинальная площадь проёма W04	0.72	m2	Графическая высота*
OPEN-W05	Номинальная площадь проёма W05	3.84	m2	Графическая высота*
OPEN-W02	Номинальная площадь проёма W02	3.84	m2	Графическая высота*
OPEN-W01	Номинальная площадь проёма W01	20.1	m2	Графическая высота*
ROOF-PLAN	Основная крыша: горизонтальная проекция	114.73	m2	План / номинал
ROOF-SLOPES	Основная крыша: два графических ската	124.29	m2	Графическая высота*
ROOF-SLOPE-LENGTH	Длина графического ската	4.42	m	Графическая высота*
ROOF-RIDGE	Конёк геометрический	14.06	m	План / номинал
ROOF-EAVES	Сумма двух нижних кромок	28.12	m	План / номинал
ROOF-VERGES	Четыре наклонные торцевые кромки	17.68	m	Графическая высота*

* Не заказные количества. Формулы, источники, вычеты и ограничения — в CSV/JSON. Отходы, нахлёсты и запас не включены; неизвестное не равно нулю. Не складывать брутто, нетто и их подмножества.

Обмер модели для сметы · 4

Размеры новой геометрии. Номинальные контрольные грани; не монтажный чертёж.

ID количества	Объект / объём работ	Количество	Ед.	Основание / исключения
CANOPY-PLAN	Навес: проекция	71.83	m2	План / номинал
LOUNGE-FLOOR	Лаундж: граница плиточного пола	41.16	m2	План / номинал
TERRACE-TOTAL	Все контуры террас, включая лаундж	100.93	m2	План / номинал
TERRACE-OPEN	Открытая часть террас вне лаунджа	59.77	m2	План / номинал
SOUTH-CHEEK	Южная щека террасы, одна плоскость	8.25	m2	Графическая высота*
LOUNGE-GLASS	Северная и западная границы остекления	39.1	m2	Графическая высота*
LOUNGE-EAST	Глухая восточная плоскость лаунджа	14.41	m2	Графическая высота*
CEIL-VAULT	Подшивка скатов гостиной	25.51	m2	Графическая высота*
CEIL-FLAT	Плоские потолки: зоны комнат	50.63	m2	Графическая высота*
WALL-VAULT-HIGH	Верхние плоскости свода >3 м	13.75	m2	Графическая высота*

* Не заказные количества. Формулы, источники, вычеты и ограничения — в CSV/JSON. Отходы, нахлёсты и запас не включены; неизвестное не равно нулю. Не складывать брутто, нетто и их подмножества.

Ведомость уточнений материалов · 1 / 2

Размеры новой геометрии. Номинальные контрольные грани; не монтажный чертёж.

ID количества	Пакет / позиция	Ед.	Кол-во	Что представить
SITE-EARTH	Земляные работы / вывоз / замена грунта	m3	TBC	Решение + обмер / спецификация
FOUND-CONCRETE	Бетон фундамента и подбетонка	m3	TBC	Решение + обмер / спецификация
FOUND-REBAR	Арматура / анкеры фундамента	kg	TBC	Решение + обмер / спецификация
FOUND-PILES	Сваи, длины и оголовки	pcs	TBC	Решение + обмер / спецификация
FLOOR-BUILDUP	Пирог пола / утепление / гидроизоляция	m3	TBC	Решение + обмер / спецификация
FRAME-TIMBER	Каркас: стойки, обвязки, перемычки, балки	m3	TBC	Решение + обмер / спецификация
FRAME-CONNECT	Соединители, крепёж, hold-down и анкеры	pcs	TBC	Решение + обмер / спецификация
FRAME-SHEATH	Конструкционная обшивка / диафрагмы	m2	TBC	Решение + обмер / спецификация
WALL-INSUL	Утепление наружной стены по каждому слою	m3	TBC	Решение + обмер / спецификация
PART-ECOWOOL	Эковата перегородок: объём / масса	kg	TBC	Решение + обмер / спецификация
PART-LINING	Облицовки перегородок по слоям / мокрые добавки	m2	TBC	Решение + обмер / спецификация
AIR-VAPOUR	Воздушный и парорегулирующий слои, ленты	m2	TBC	Решение + обмер / спецификация
FACADE-CSP	Окрашенная ЦСП: листы, толщина, раскрой	m2	TBC	Решение + обмер / спецификация
FACADE-PAINT	Грунт / краска / кромки ЦСП	l	TBC	Решение + обмер / спецификация
FACADE-SUBFRAME	Вентфасад: подконструкция, зазор, крепёж	m	TBC	Решение + обмер / спецификация

Подрядчик заполняет количество после принятия расчёта / изделия. TBC не равно нулю. Работы, цены, дата, валюта, налоги, нахлёсты и отходы — отдельно по форме B106; электронные строки с теми же ID в CSV.

Ведомость уточнений материалов · 2 / 2

Размеры новой геометрии. Номинальные контрольные грани; не монтажный чертёж.

ID количества	Пакет / позиция	Ед.	Кол-во	Что представить
FACADE-OTHER	Остальные фасадные зоны и доборы	m2	TBC	Решение + обмер / спецификация
ROOF-TIMBER	Стропила / фермы / балки / связи крыши	m3	TBC	Решение + обмер / спецификация
ROOF-FALZ	Картины фальца с замками и раскром	m2	TBC	Решение + обмер / спецификация
ROOF-BASE	Основание фальца / обрешётка / подкладка	m2	TBC	Решение + обмер / спецификация
ROOF-INSUL	Утепление: плоские зоны + скаты гостиной	m3	TBC	Решение + обмер / спецификация
ROOF-ACCESS	Кляммеры / снегозадержатели / проходки	pcs	TBC	Решение + обмер / спецификация
ROOF-DRAIN	Основной и аварийный водоотвод	m	TBC	Решение + обмер / спецификация
CANOPY-FINISH	Навес: реальный скат, конструкция, водоотвод	m2	TBC	Решение + обмер / спецификация
WINDOW-ORDER	Окна/двери: изделия, монтаж, подоконники	pcs	TBC	Решение + обмер / спецификация
LOUNGE-GLAZING	Открываемое остекление лаунджа с профилем	m2	TBC	Решение + обмер / спецификация
STOVE-MASONRY	Печь: кирпич, шамот, растворы, дверца, дымоход	pcs	TBC	Решение + обмер / спецификация
LOUNGE-HEAT	Контуры, трубы, узел теплоносителя, автоматика	m	TBC	Решение + обмер / спецификация
MEP-CABLES	Кабели, щит, защиты, трассы, освещение	m	TBC	Решение + обмер / спецификация
MEP-PIPES	Вода, канализация, отопление, вентиляция	m	TBC	Решение + обмер / спецификация
TEMP-WORKS	Леса, временные связи, доставка, подъём, защита	set	TBC	Решение + обмер / спецификация

Подрядчик заполняет количество после принятия расчёта / изделия. TBC не равно нулю. Работы, цены, дата, валюта, налоги, нахлёсты и отходы — отдельно по форме B106; электронные строки с теми же ID в CSV.