


Свес и скрытый водосток

Предлагаемый принцип: закрытая деревянная подшивка, объёмная лобовая часть и обслуживаемый скрытый жёлоб.

Принцип карнизного узла

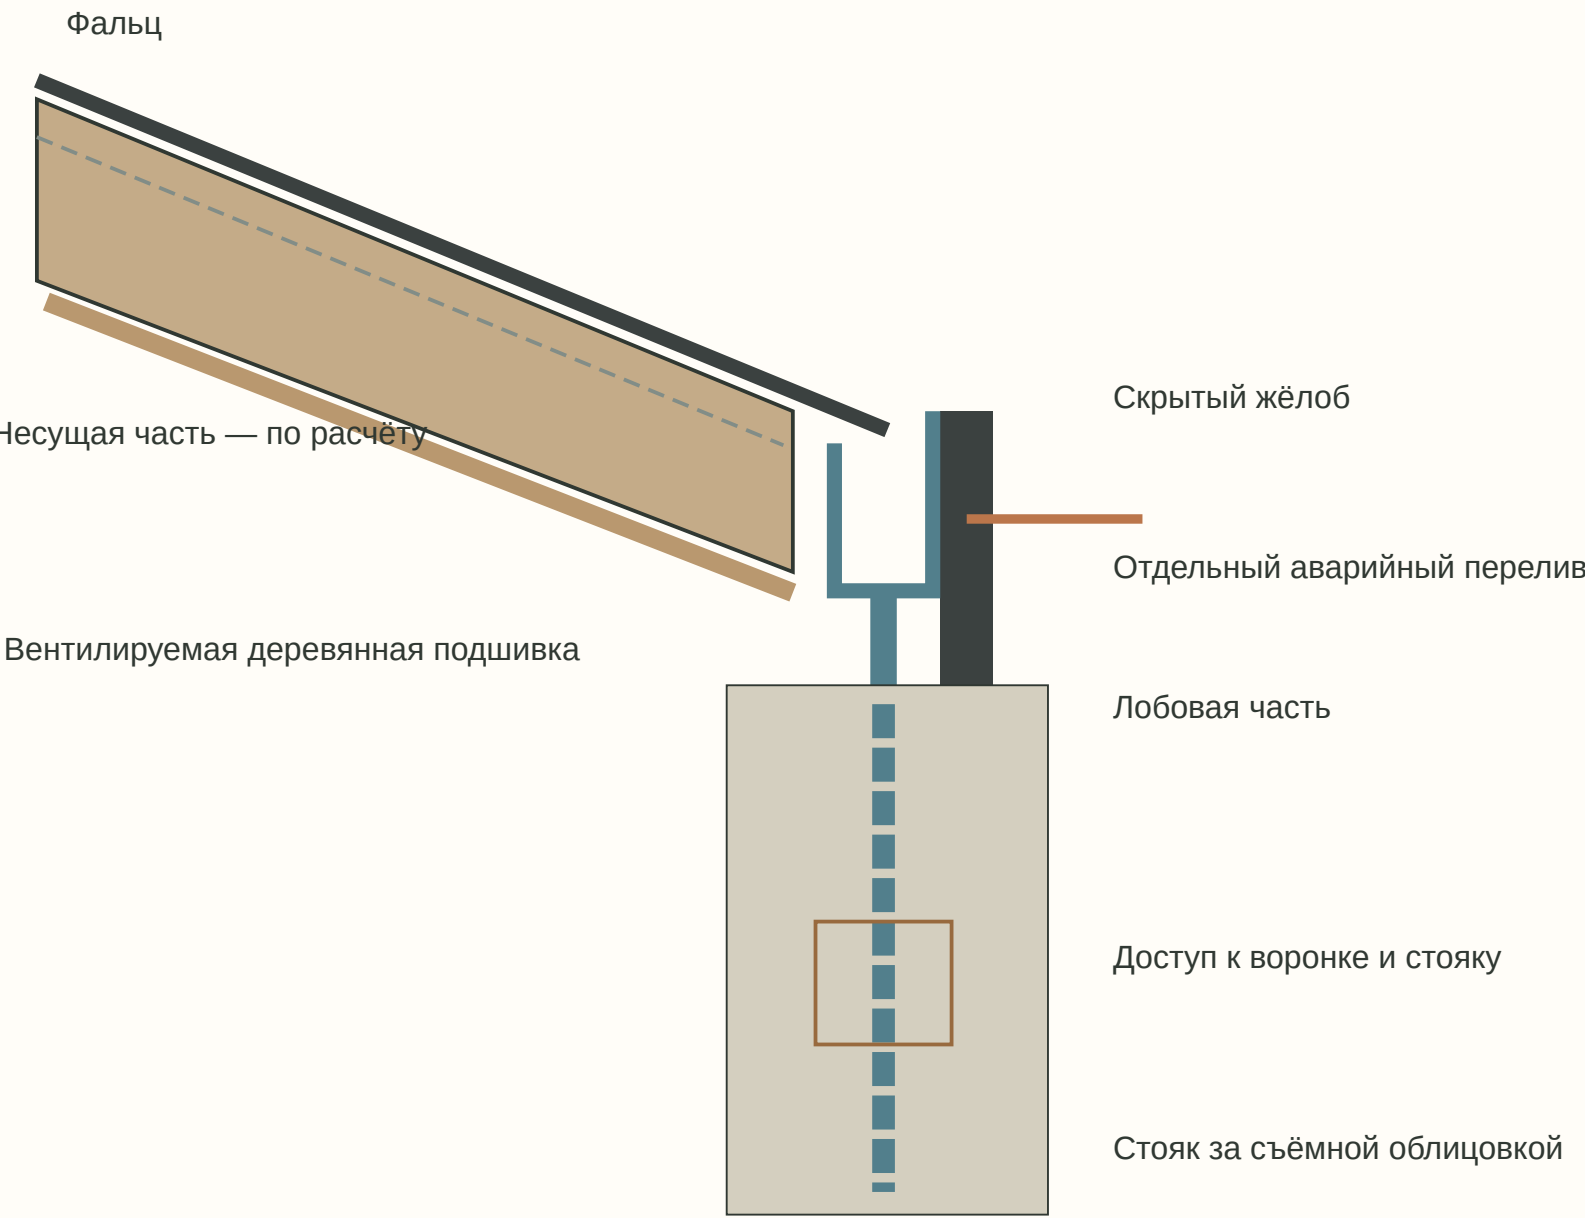

Открытый фронтонный вынос над западным стеклом — 2 500 мм по модели.

Подшивка закрывает конструкцию, но не является несущей опорой.

Сечения, опоры, крепёж и прогиб выноса должен рассчитать конструктор.

ГДЕ СОБИРАТЬ ВОДУ

Конёк дома идёт запад—восток.
Жёлоба — по северному и южному карнизам, у нижних кромок скатов.
Западная кромка над стеклом — фронтон: жёлоб вдоль ската не ставим.

Обслуживание и выпуск


Доступ сверху к жёлобу и воронке.
Ревизия стояка за съёмной панелью.
Аварийный перелив видимый, отдельный от основного стояка.
Выпуск воды — по проекту участка; не назначен на соседний участок и не направлен автоматически в озеро.

Расчётные входные данные

Осадки, снег, обледенение, водосбор.
Размеры жёлоба и труб не назначены.
Уклон навеса и сбор с него уточнить.
Конструкция и гидравлика не утверждены.

Душ · стекло и открывание

Хозяйский санузел 2 700 × 1 520 мм. Модель душа 1 000 × 1 000 мм; размеры стекла ещё не заказные.

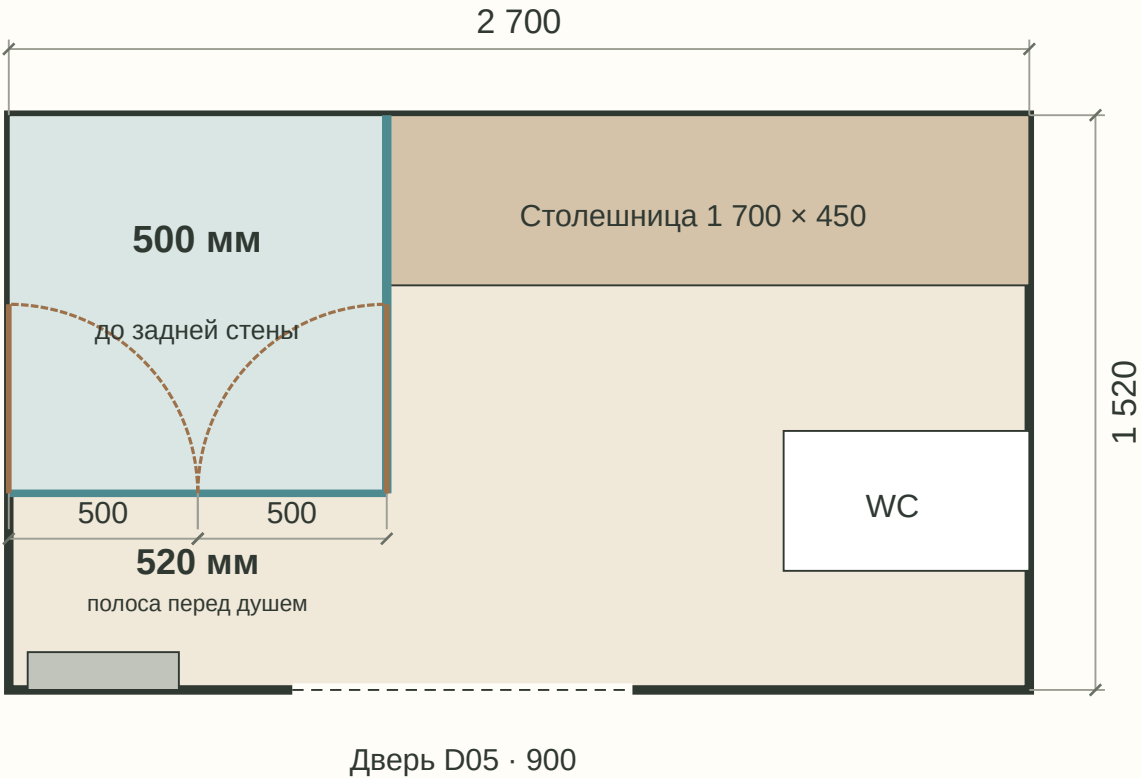

С ↑ · габариты сантехники условные

Пунктирная дверь помещения: навеска D05 ещё не выбрана.

520 мм — расстояние до стены, без полотенцесушителя.

В зоне полотенцесушителя глубиной 100 мм остаётся 420 мм.

Тёплая песочная плитка А и светлый greige В сохранены как варианты отделки.

РЕКОМЕНДУЮ ДВЕ СТВОРКИ

Два равных полотна: номинально 500 + 500 мм.

Оба открываются внутрь душа; боковая панель неподвижна.

Радиус движения каждой створки — 500 мм.

При 90° остаётся 1000 – 500 = 500 мм до задней стены.

Перед душем полотно не занимает узкую полосу прохода.

Вариант с одной створкой

800 мм дверь + 200 мм неподвижный участок.

Радиус 800 мм; до задней стены остаётся 200 мм.

Одна створка на все 1000 мм достигает задней стены:

запаса под ручку и арматуру в номинальной схеме нет.

Поэтому широкую цельную створку здесь не выбираю.

Что проверяем перед заказом

Ширина чистого входа после вычета петель и уплотнений.

Фактические выступы смесителя, ручек и лейки.

Петли: рабочее открывание внутрь и аварийный доступ.

Стекло, крепление к боковой панели, уплотнения, порог.

Навеска D05 и перенос полотенцесушителя при коллизии.

Это геометрическая проверка номинальных полотен.

Изделие и безопасные рабочие зазоры пока не выбраны.