


Посадка на топосъёмке

Исай · нижний зелёный контур. Север координатной сетки сверху, озеро — с западной стороны.

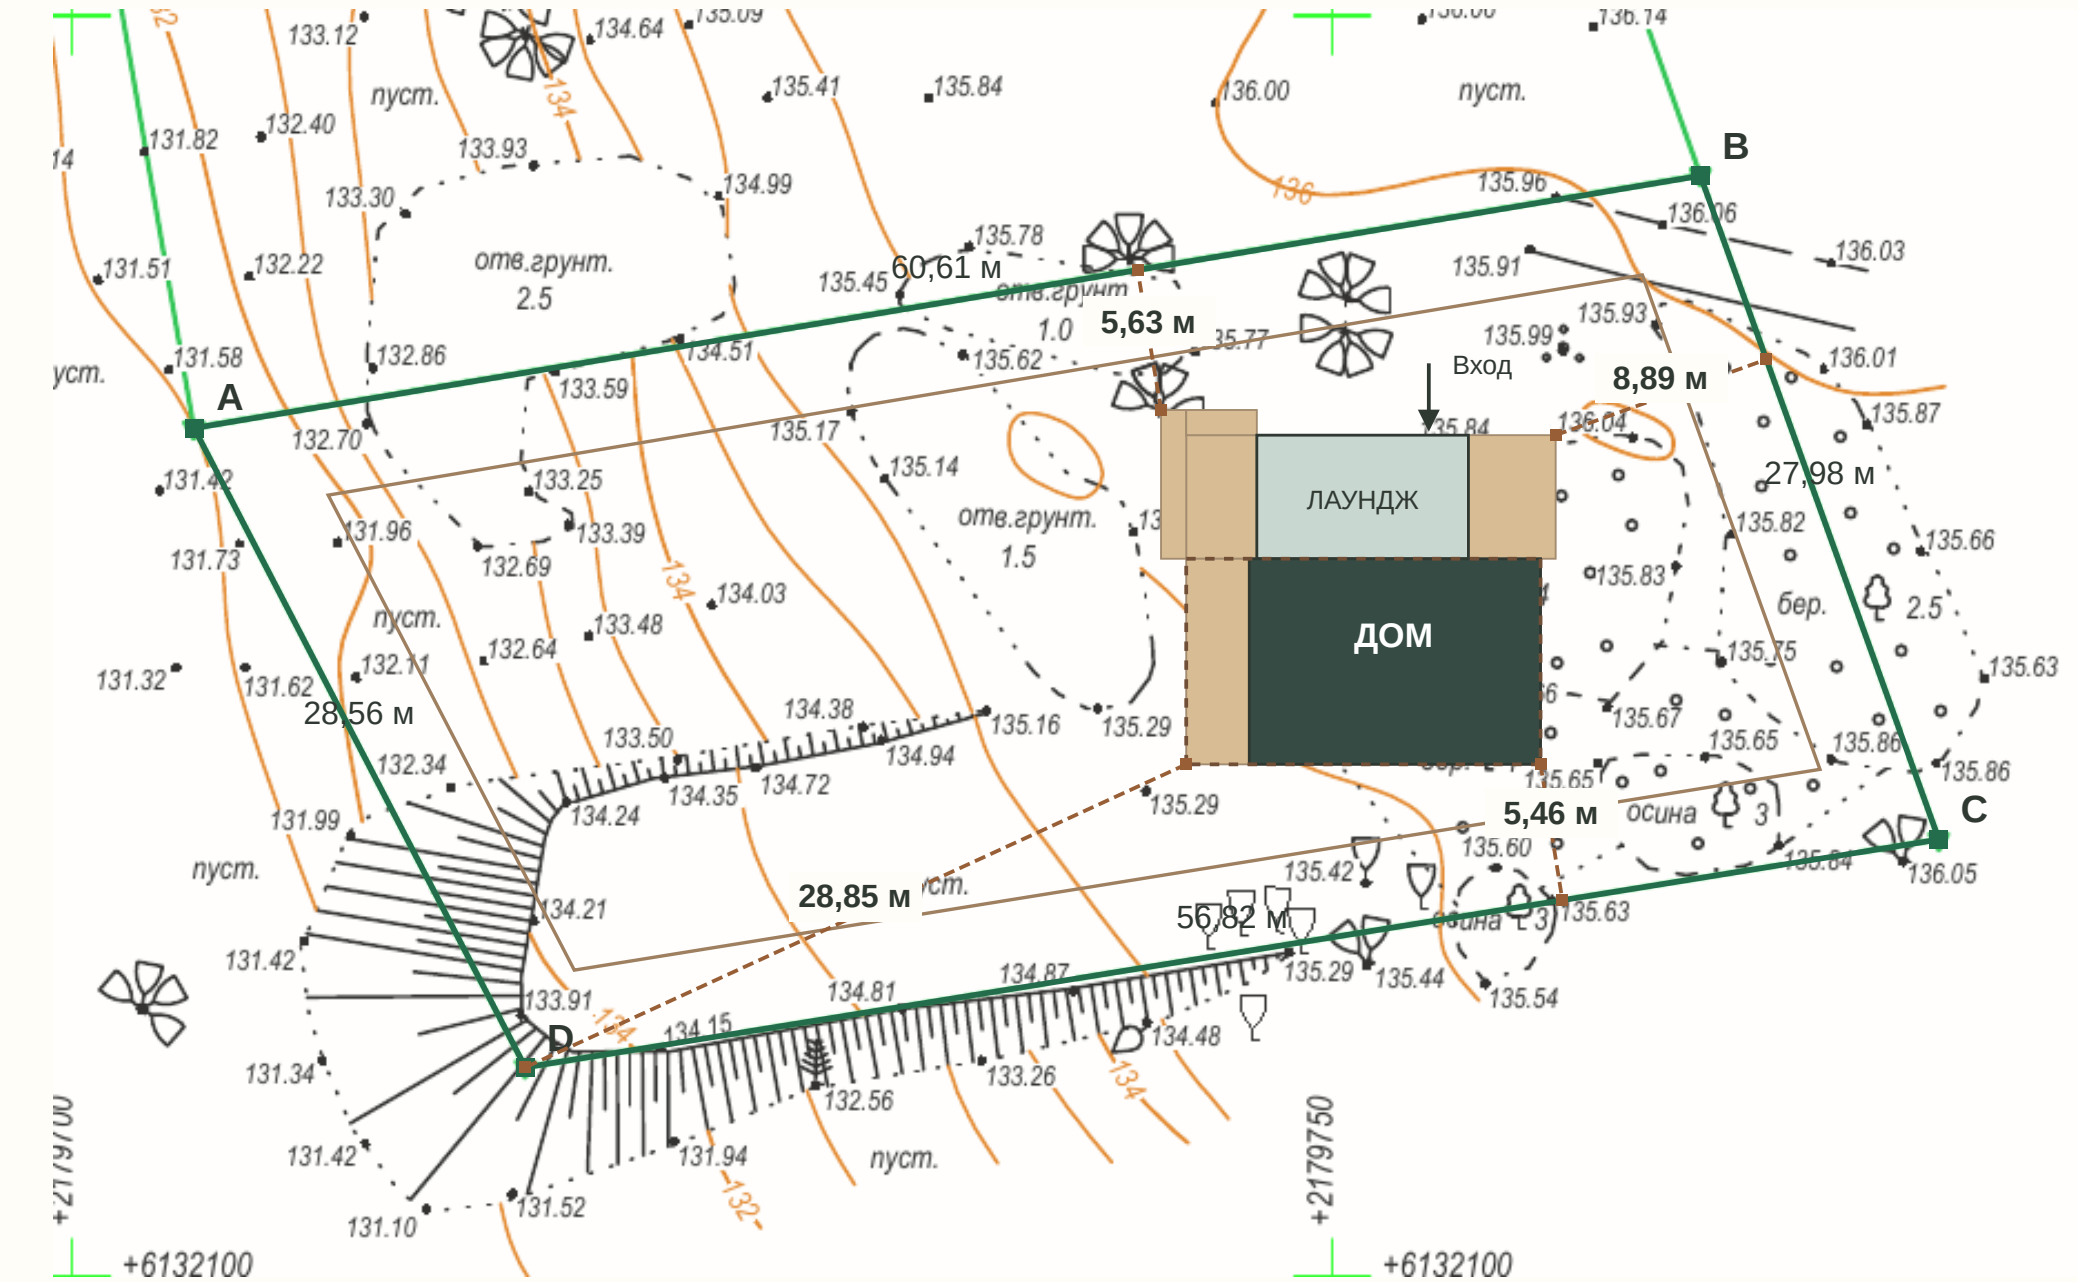

← ОЗЕРО / ЗАПАД

Пятно смещено к восточной части участка, вдали от западного перепада.
Подъезд, деревья и отметка пола требуют отдельной привязки к съёмке.

ОТ ГРАНИЦ

Требование: $\geq 3,50$ м

A—B / северная

5,63 м

B—C / восточная

8,89 м

C—D / южная

5,46 м

D—A / западная

28,85 м

Отступы до ближайшего элемента:
дом + лаундж + кровля + настилы.
Минимум по всему контуру: 5,46 м.
Запас к 3,50 м: 1,96 м.


ОПОРА ДЛЯ ПРОВЕРКИ

Ноль модели, предложение:
E 2179747,00 / N 6132128,50 м
СЗ угол дома:
E 2179746,70 / N 6132128,50 м
Без поворота / X восток, Y юг.
Площадь контура: $\approx 1605,19$ м².
Сетка: 50 м = 2362 CAD единицы.
Юридические вершины не заверены.
Абсолютная отметка пола не задана.

Координаты — эскиз, не вынос в натуру.

Посадка · размеры и привязки

Исай · нижний зелёный контур. Север координатной сетки сверху, озеро — с западной стороны.

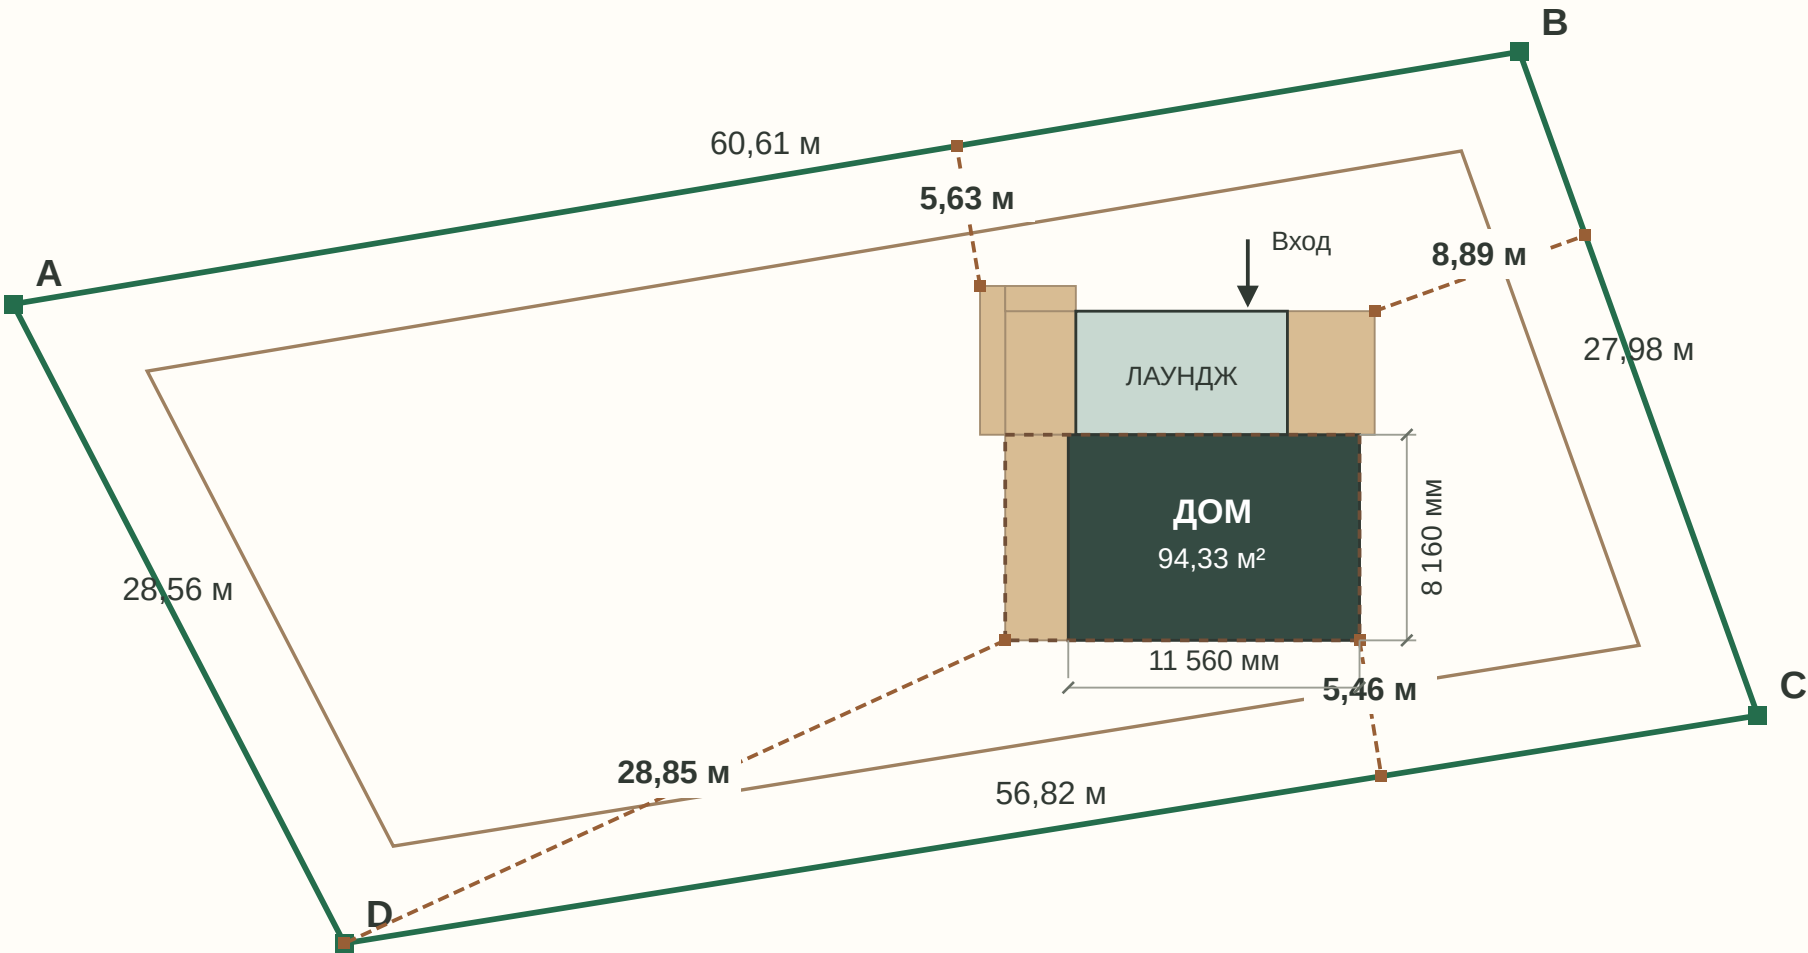

ОТ ГРАНИЦ

Требование: $\geq 3,50$ м

A—B / северная

5,63 м

B—C / восточная

8,89 м

C—D / южная

5,46 м

D—A / западная

28,85 м

Отступы до ближайшего элемента:
дом + лаундж + кровля + настилы.
Минимум по всему контуру: 5,46 м.
Запас к 3,50 м: 1,96 м.

ОПОРА ДЛЯ ПРОВЕРКИ

Ноль модели, предложение:
E 2179747,00 / N 6132128,50 м
СЗ угол дома:
E 2179746,70 / N 6132128,50 м
Без поворота / X восток, Y юг.
Площадь контура: $\approx 1605,19$ м².
Сетка: 50 м = 2362 CAD единицы.
Юридические вершины не заверены.
Абсолютная отметка пола не задана.

← ОЗЕРО / ЗАПАД

Пятно смещено к восточной части участка, вдали от западного перепада.
Подъезд, деревья и отметка пола требуют отдельной привязки к съёмке.

Координаты — эскиз, не вынос в натуру.