


Общий план · дом, тёплый лаундж и навес

Вариант А. Две связанные тёплые зоны; открытый навес и настилы показаны отдельно.

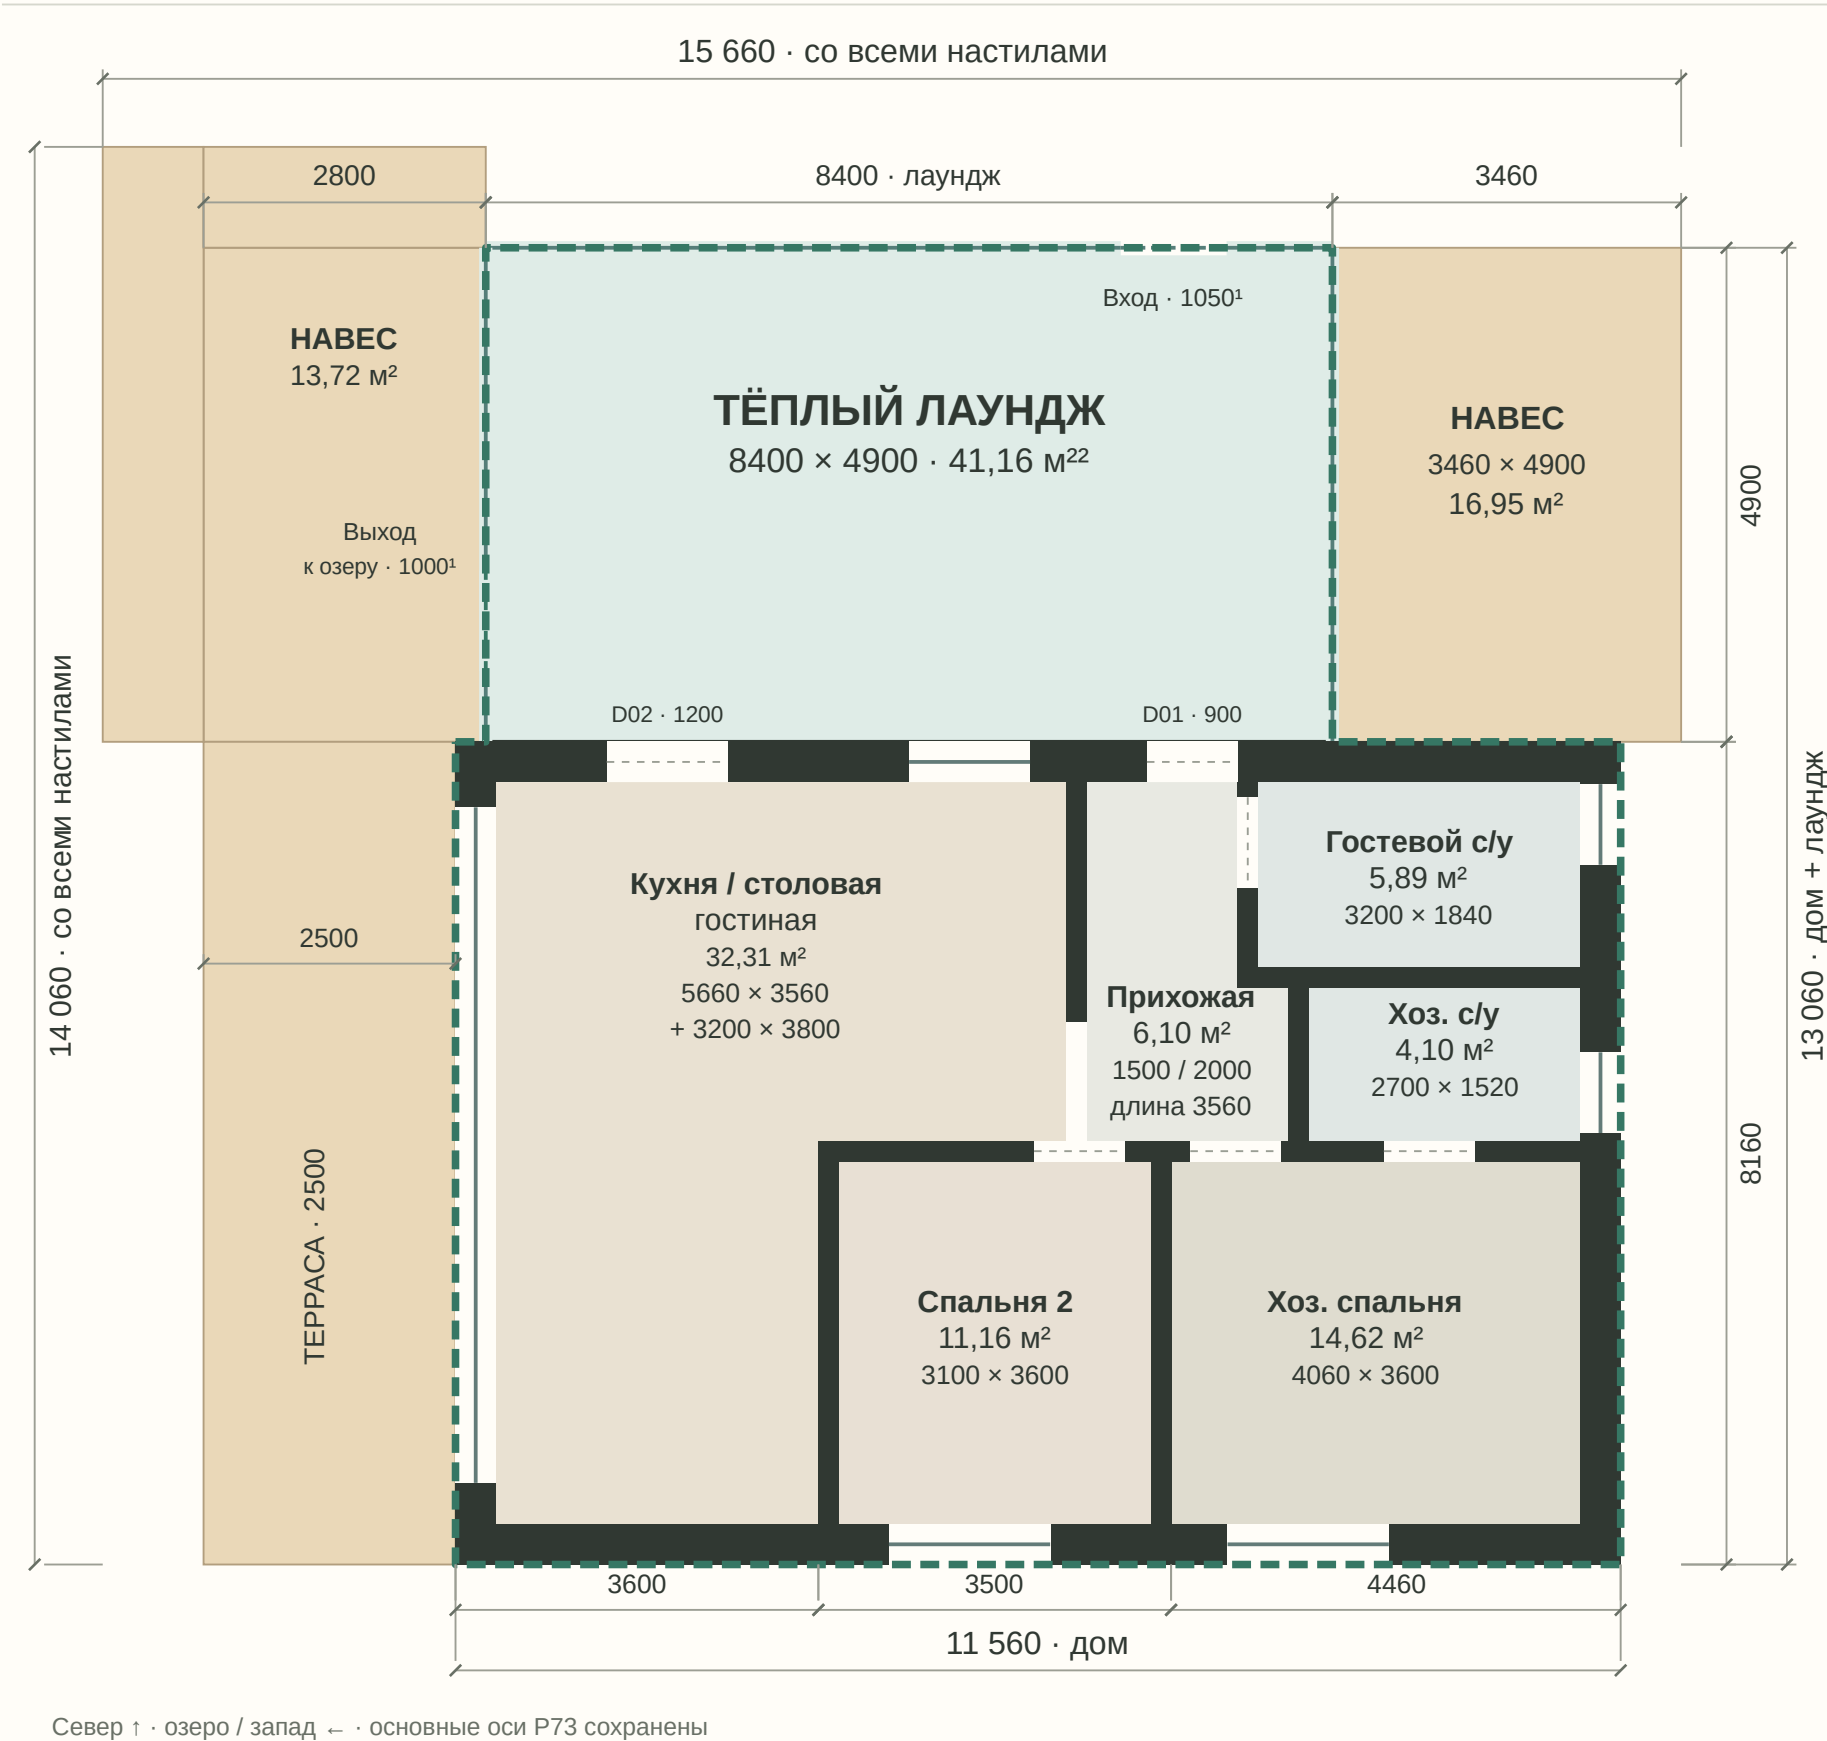

ПЛОЩАДИ ПО КОНТУРАМ

Дом · 11 560 × 8160	94,33 м ²
Лаундж · 8400 × 4900	41,16 м ²
Тёплый контур А	135,49 м ²
Открытая часть северного навеса	30,67 м ²
Все открытые настилы	59,77 м ²

Зелёный пунктир = тёплый контур по заданию.


Вход с севера через лаундж; двери D01/D02 связаны с прихожей и общей зоной дома. Озеро и выход на запад сохранены. Лаундж + навес: один общий односкатный объём кровли. Крыша дома остаётся двускатной. Стены дома: резерв 400 мм, перегородки 200 мм.

¹ Номинальный проём / габарит ячейки; чистый проход и изделия уточняются.

² Контур лаунджа до толщин ограждения. Площади тёплого контура включают стены дома и резервы; это не чистая площадь пола.

Вариант В · техпомещение под навесом


Предложение для электрокотла и ГВС. Габариты оборудования показаны резервами, изделия не выбраны.

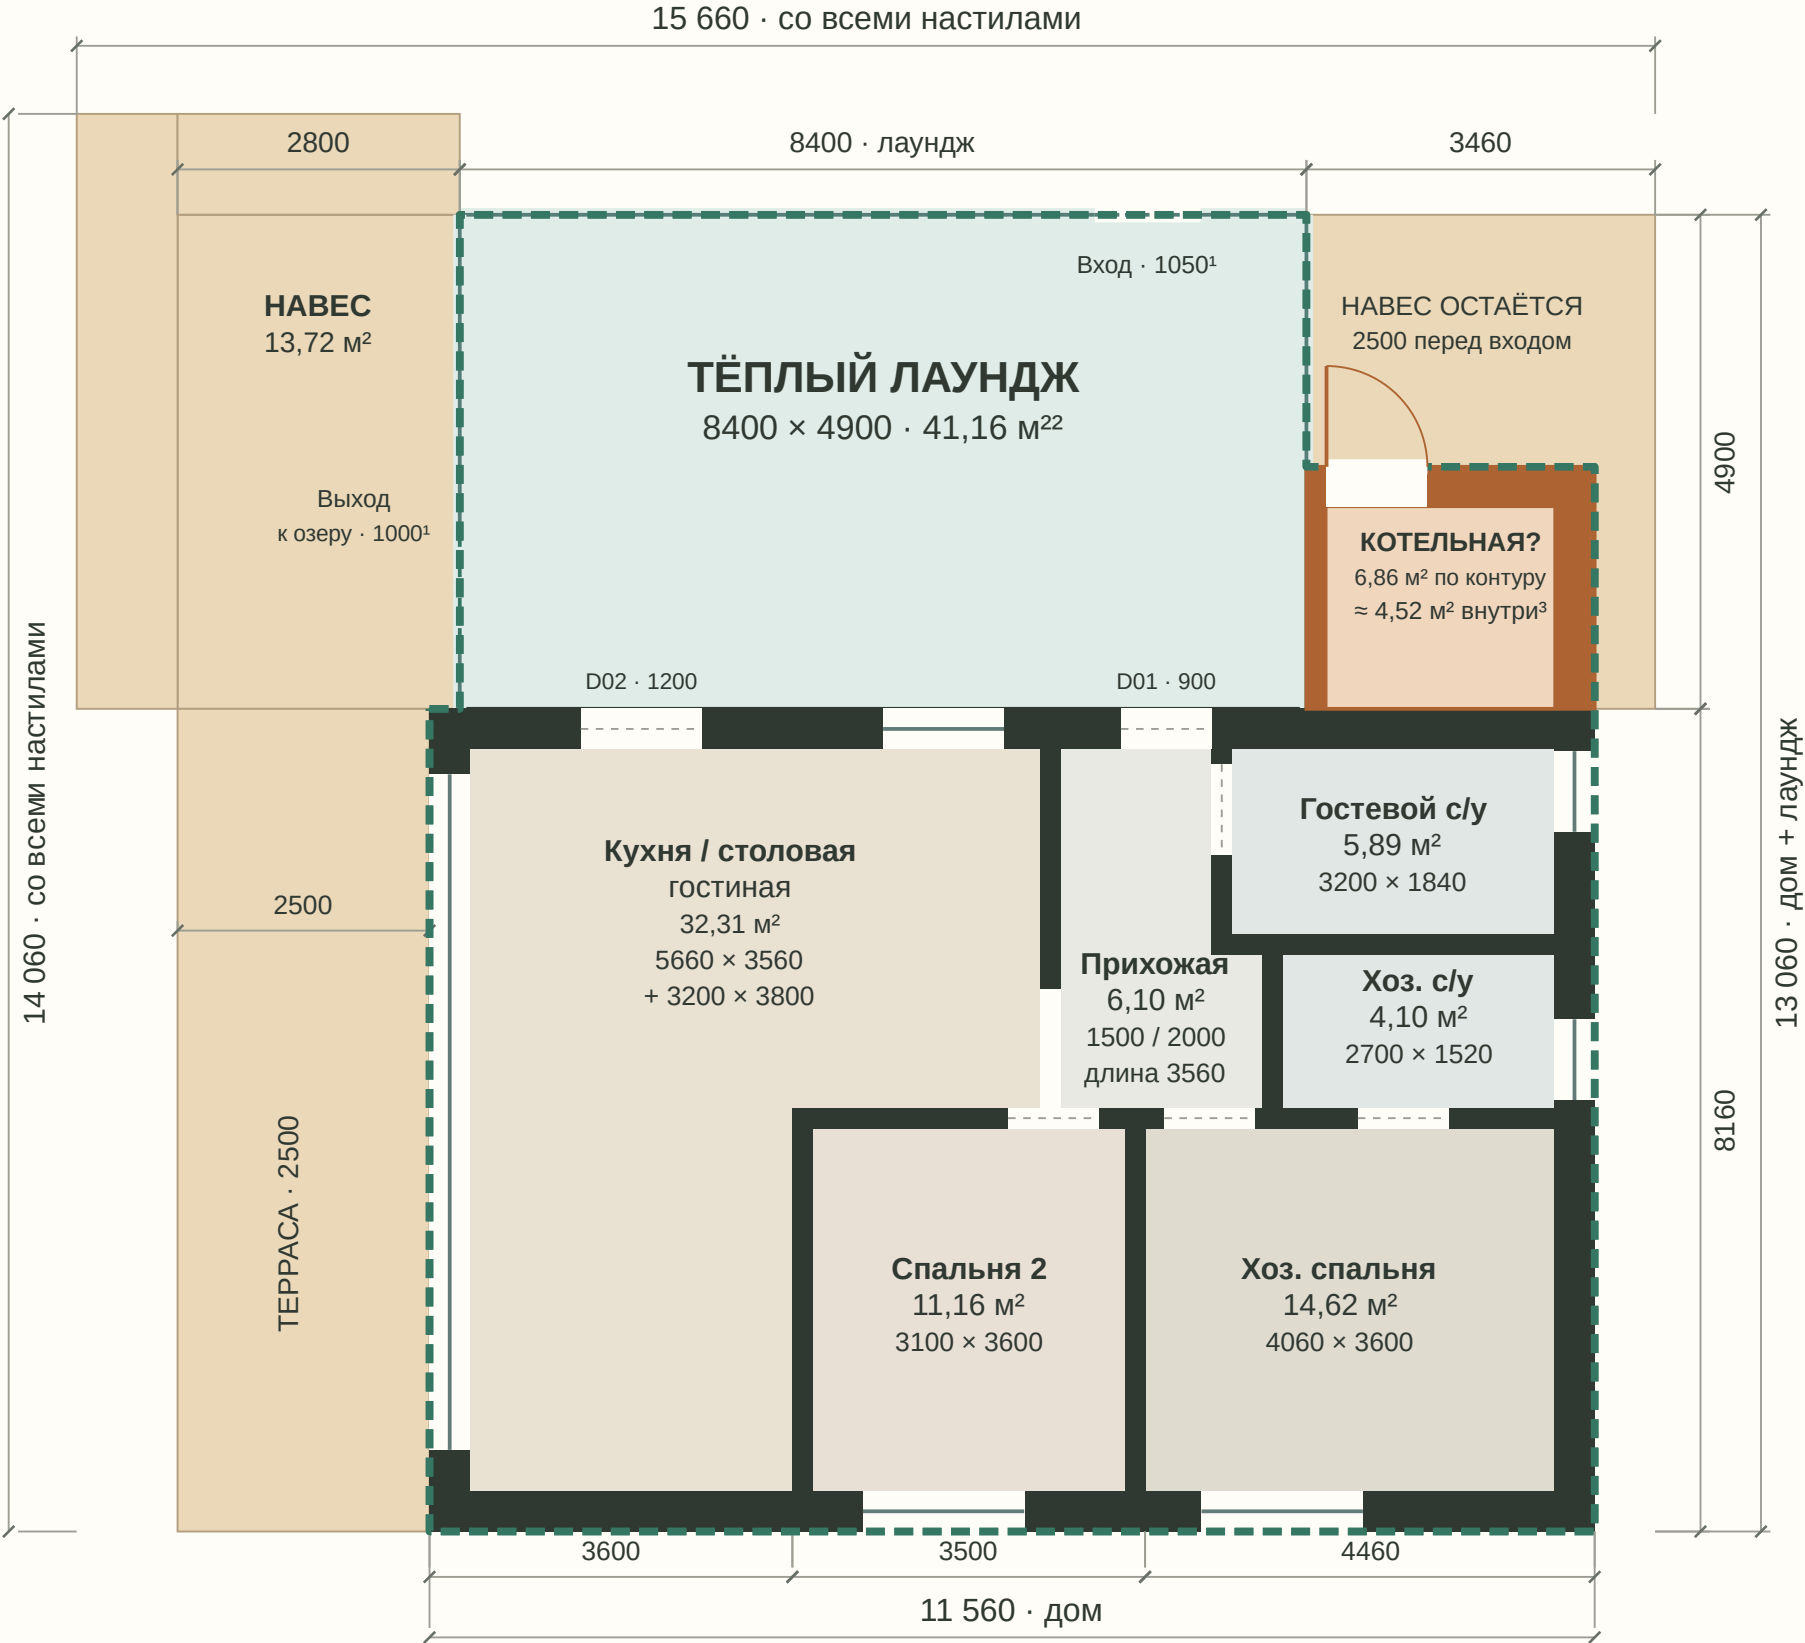

Север ↑ · озеро / запад ← · основные оси P73 сохранены

ТЕХПОМЕЩЕНИЕ · УВЕЛИЧЕННАЯ СХЕМА

Контур 2860 × 2400 мм · схема без масштаба.

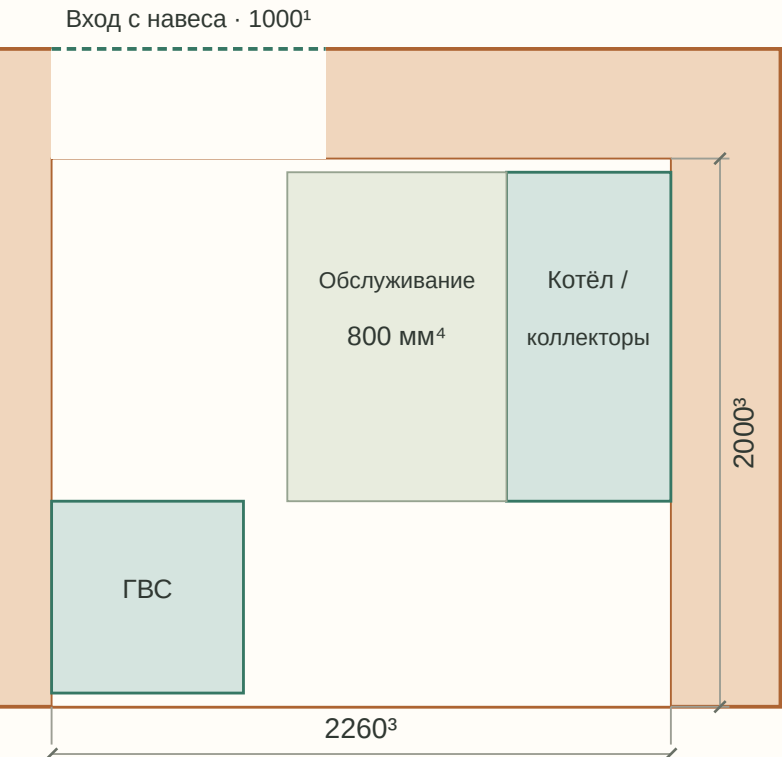

Тёплый контур В: 142,35 м²

Открытый северный навес: 23,81 м²

Все открытые настилы: 52,91 м²

Вход отдельный с навеса · проём 1000¹.

Близко к гостевому с/у и водяным системам.

Западный навес и лаундж сохраняются.

³ Расчёт с резервом стен 400 / 200 мм.

⁴ Рабочий резерв, не норма и не паспорт котла.

Состав стен, высота, вентиляция, шум,
трассы и замена оборудования требуют проверки.

¹ Номинальный проём / габарит ячейки;
чистый проход и изделия уточняются.

² Контур лаунджа до толщин ограждения.
Площади тёплого контура включают стены
дома и резервы; это не чистая площадь пола.